


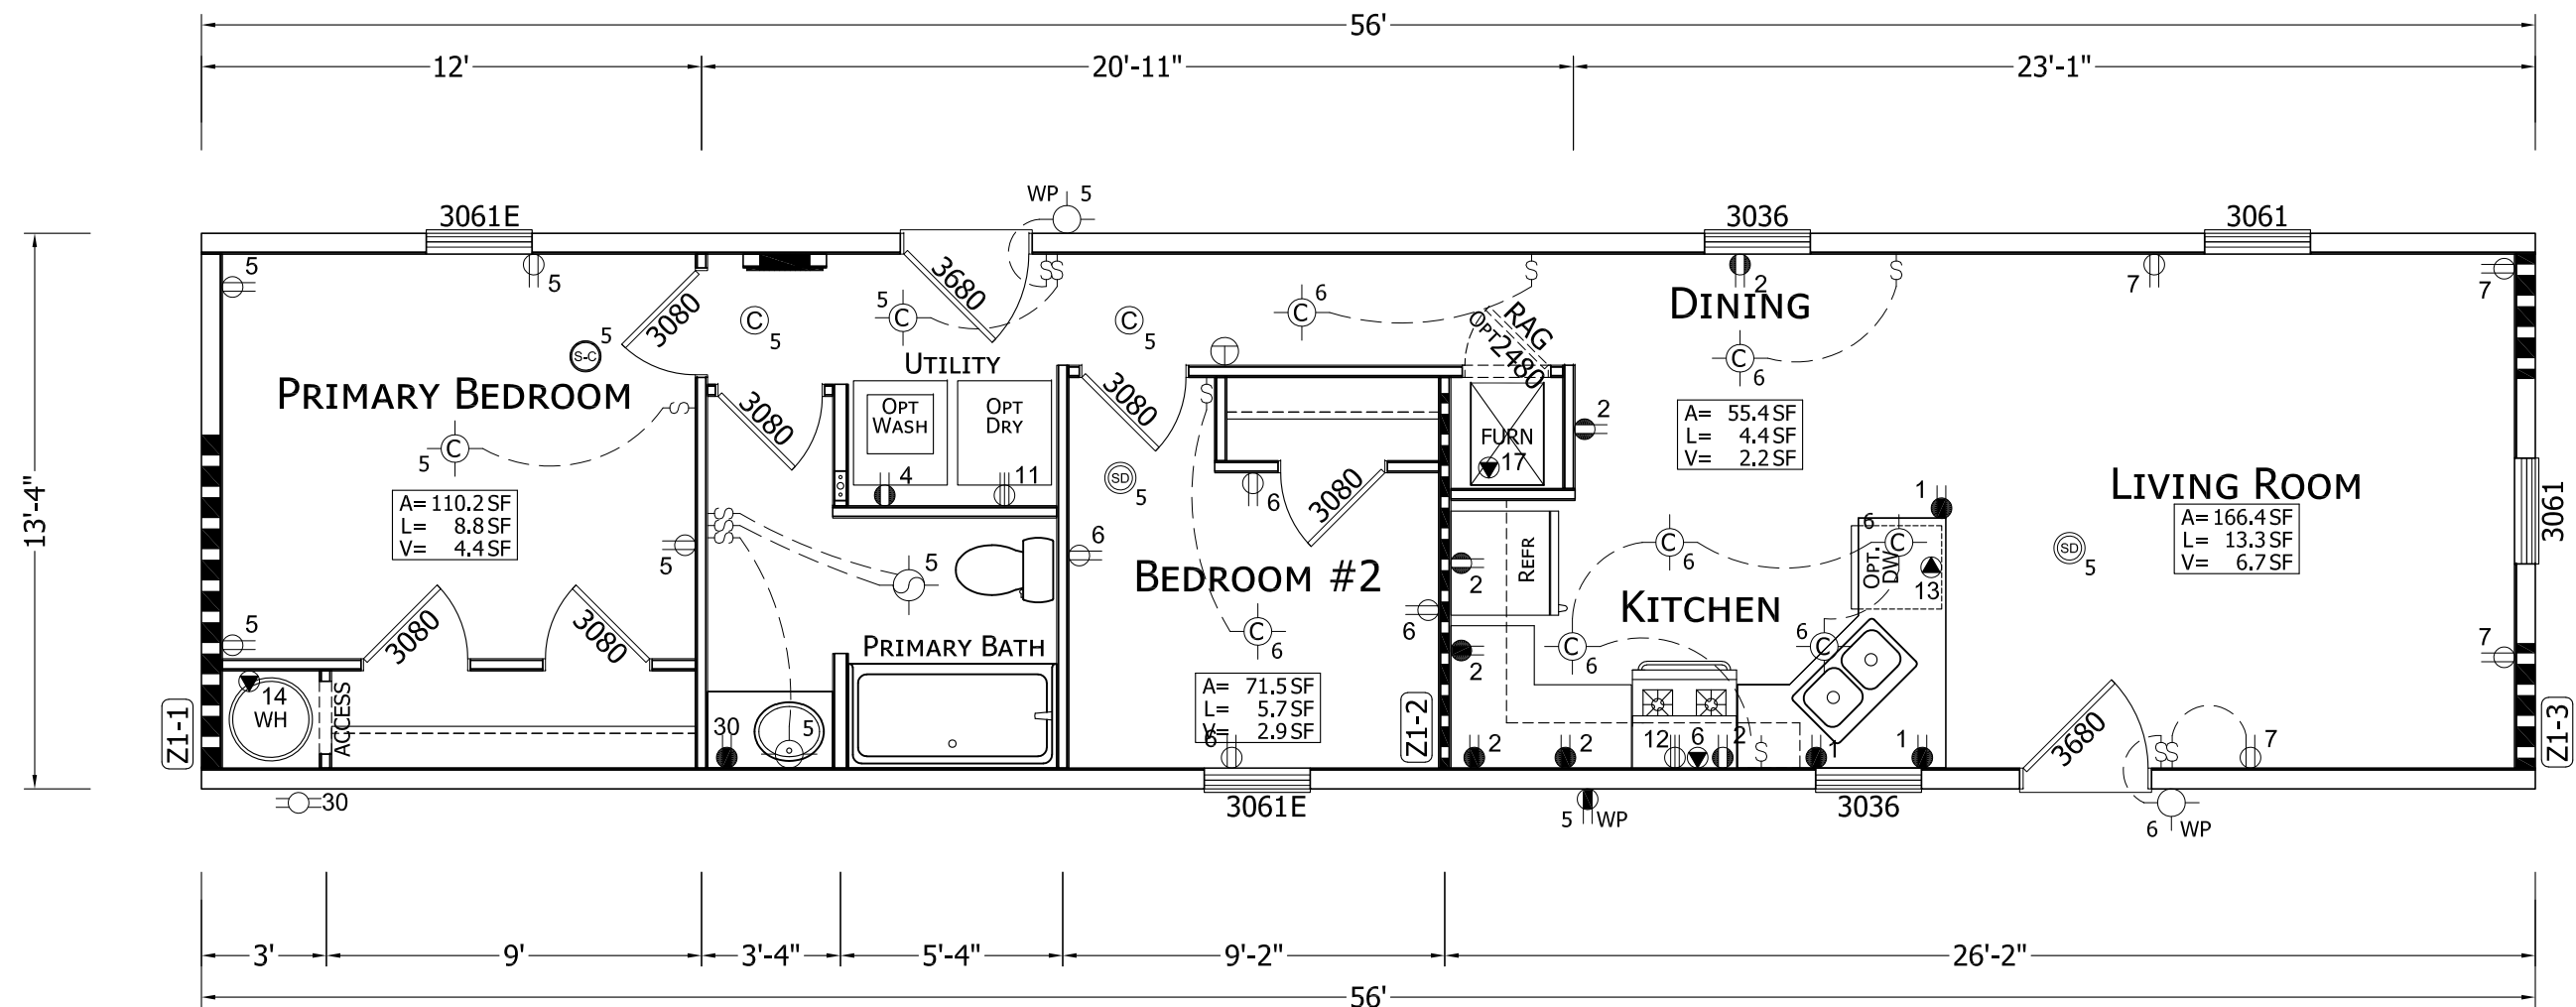

DESIGN CRITERIA
 ZONES: WIND 1, ROOF MIDDLE, TEMP III
 TOTAL ROUGH WINDOW OPENINGS: 67.4 SF




CHAMPION
HOME BUILDERS
 755 W. BIG BEAVER ROAD, SUITE 1000 TROY, MI 48064
 PHONE: 248-614-8200



MODIFICATIONS

PROJECT: 112AP-1456H21023 56'-0" x 13'-4" 2BD 1BT	TITLE: FLOOR PLAN ELECTRICAL PLAN	SHEET: AE-101
DRAWN BY: KG	FILENAME: 112AP-1456H21023	PROPRIETARY AND CONFIDENTIAL THESE DRAWINGS AND SPECIFICATIONS ARE ORIGINAL. PROPRIETARY AND CONFIDENTIAL MATERIALS OF CHAMPION. COPYRIGHT © 1976-2024 BY CHAMPION
DATE: 08-21-23		
SCALE: 5/32" = 1'-0"		

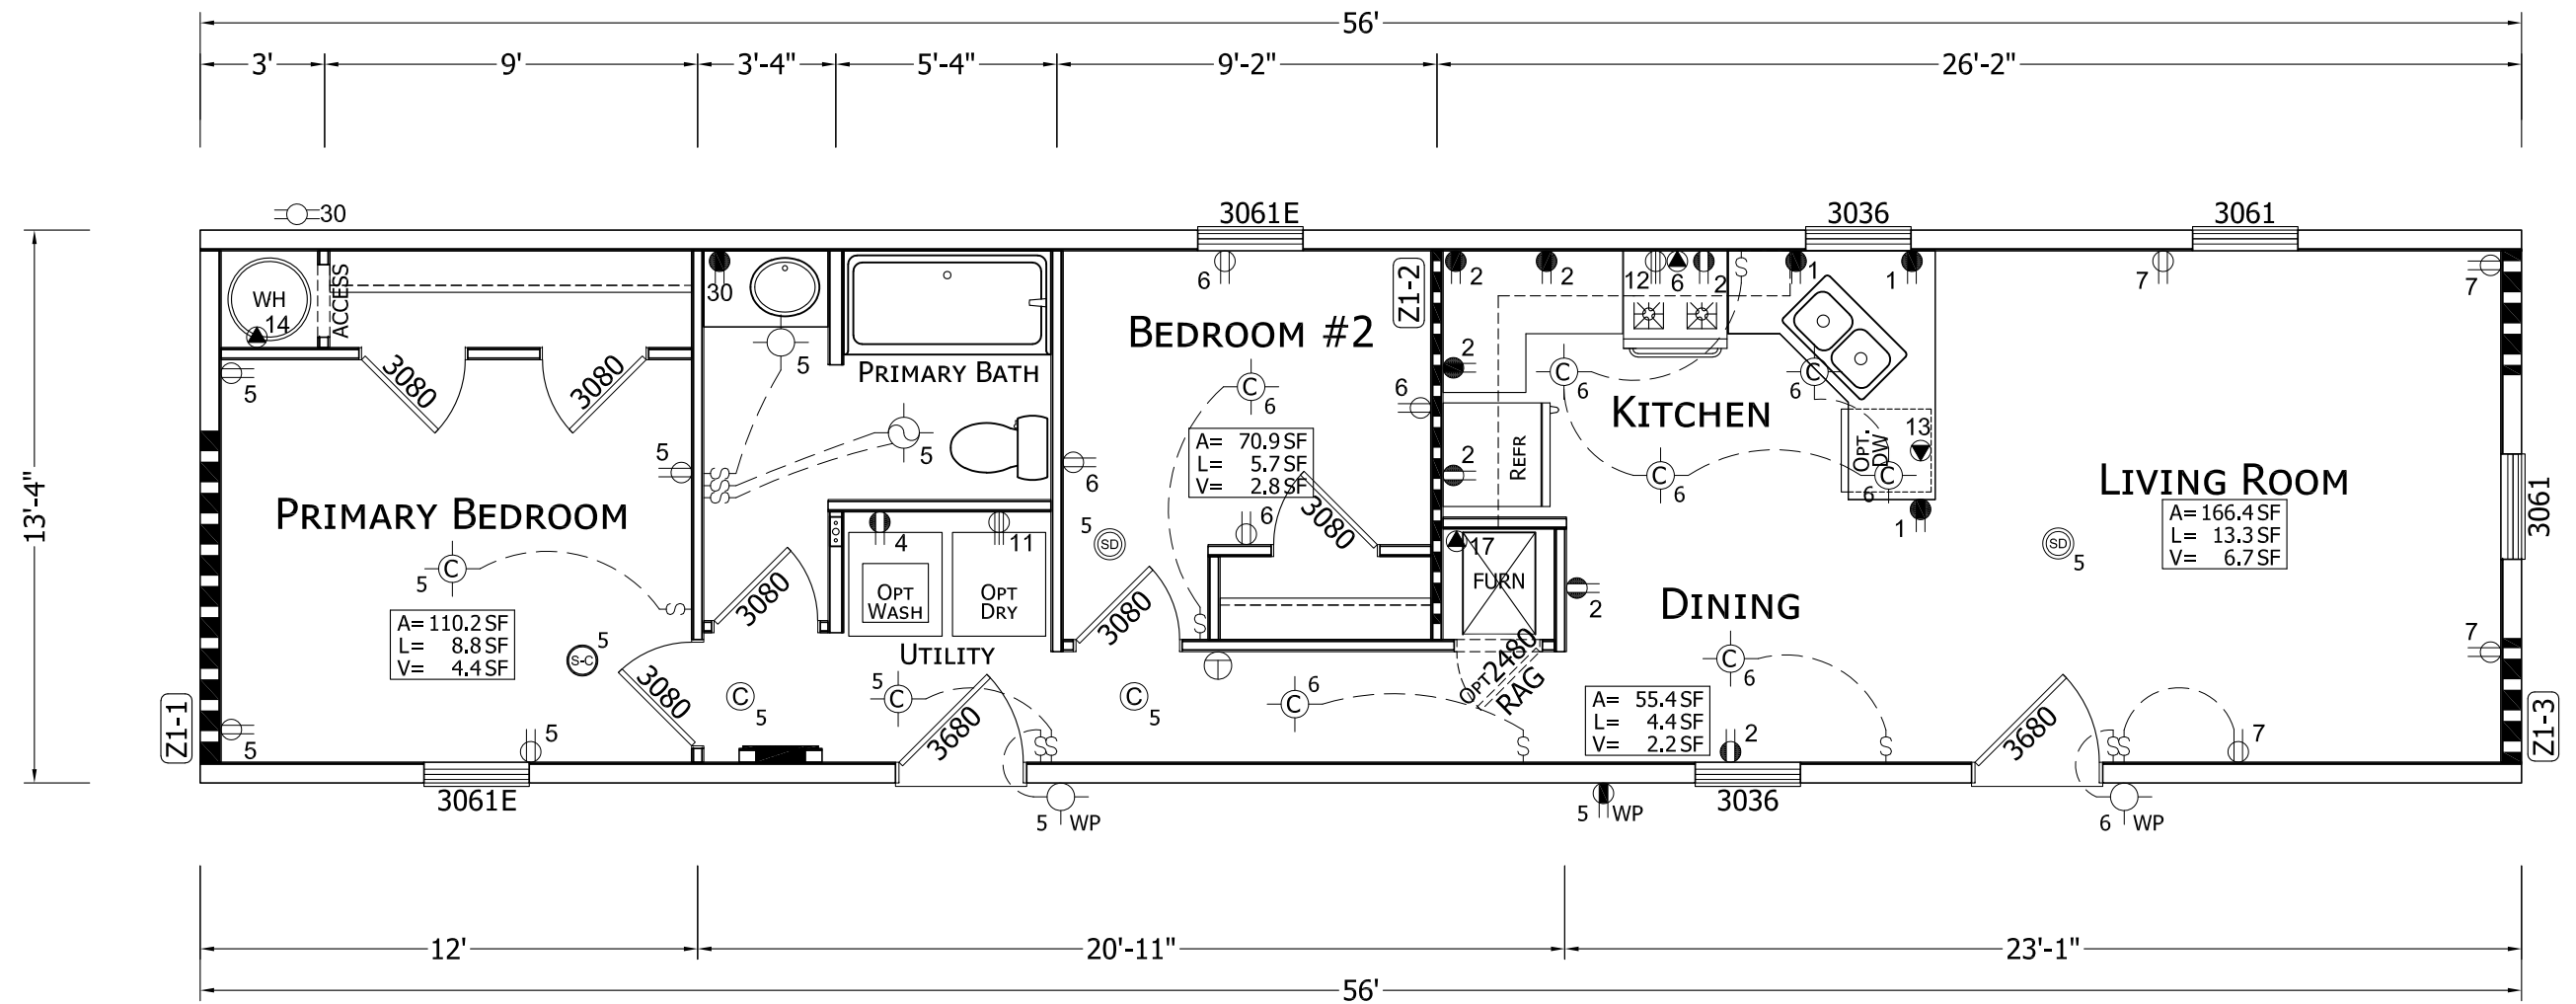

OPT. REVERSE AISLE



CHAMPION
HOME BUILDERS

755 W. BIG BEAVER ROAD, SUITE 1000 TROY, MI 48064
PHONE: 248-614-8200



1 2025 CODE UPDATE

MODIFICATIONS

2/7/2025 JR

PROJECT:
112AP-1456H21023
56'-0" x 13'-4"
2BD 1BT

DRAWN BY: KG
DATE: 08-21-23
SCALE: 5/32" = 1'-0"

TITLE:
FLOOR PLAN
ELECTRICAL PLAN

FILENAME: 112AP-1456H21023


SHEET:

AE-102

PROPRIETARY AND CONFIDENTIAL
THESE DRAWINGS AND SPECIFICATIONS ARE ORIGINAL
PROPRIETARY AND CONFIDENTIAL MATERIALS OF CHAMPION.
COPYRIGHT © 1976-2025 BY CHAMPION

NOTES:

- 1. PIPE SIZES DETERMINED BY FITTINGS ON EACH SIDE.
- 2. SITE INSTALLED PLUMBING NOTED BY ----- .

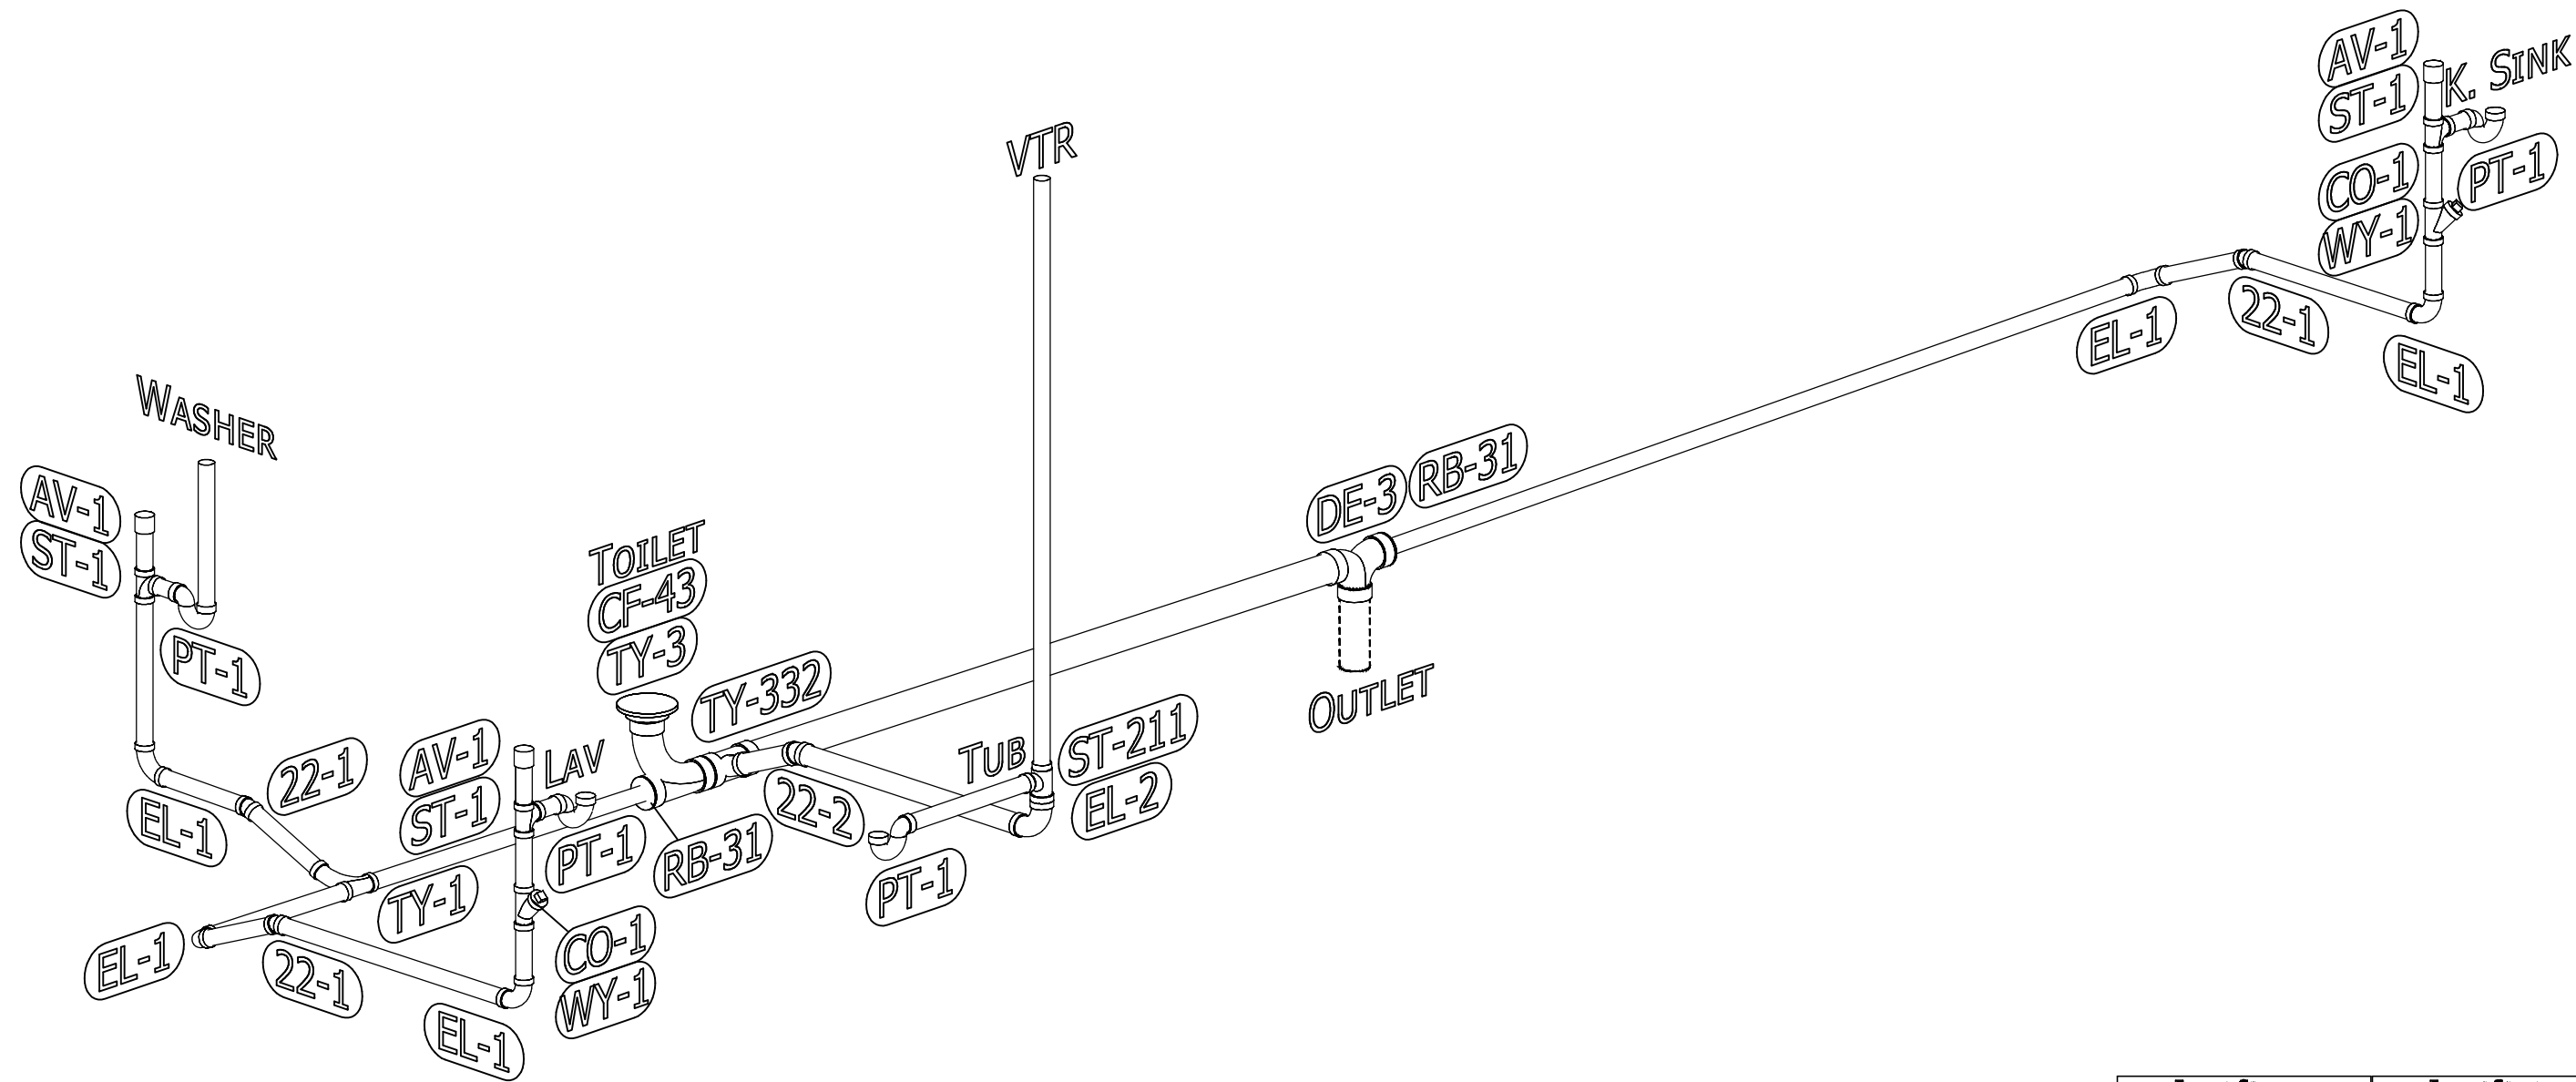

FITTING SCHEDULE		FITTING SCHEDULE	
CALL	NAME	CALL	NAME
22-1	1 1/2" 22 1/2° ELL	PT-1	1 1/2" P-TRAP
22-2	2" 22 1/2° ELL	RB-31	3" x 1 1/2" BUSHING
AV-1	1 1/2" AUTO VENT	ST-1	1 1/2" TEE
CF-43	4" x 3" CLOSET FLANGE	ST-211	2" x 1 1/2" x 1 1/2" TEE
CO-1	1 1/2" CLEANOUT	TY-1	1 1/2" LTTY
DE-3	3" DOUBLE ELL	TY-3	3" LTTY
EL-1	1 1/2" LT 90° ELL	TY-332	3" x 3" x 2" LTTY
EL-2	2" LT 90° ELL	WY-1	1 1/2" WYE

CHAMPION

HOME BUILDERS

755 W. BIG BEAVER ROAD, SUITE 1000 TROY, MI 48064
PHONE: 248-614-8200



MODIFICATIONS

PROJECT:
112AP-1456H21023
56'-0" x 13'-4"
2BD 1BT

DRAWN BY: KG

DATE: 08-21-23

SCALE: N.T.S.

TITLE:
DRAIN LINE
PLAN


FILENAME: 112AP-1456H21023

SHEET:
D-101

PROPRIETARY AND CONFIDENTIAL
THESE DRAWINGS AND SPECIFICATIONS ARE ORIGINAL,
PROPRIETARY AND CONFIDENTIAL MATERIALS OF CHAMPION.
COPYRIGHT © 1976-2024 BY CHAMPION

NOTES:

- 1. PIPE SIZES DETERMINED BY FITTINGS ON EACH SIDE.
- 2. SITE INSTALLED PLUMBING NOTED BY ----- .

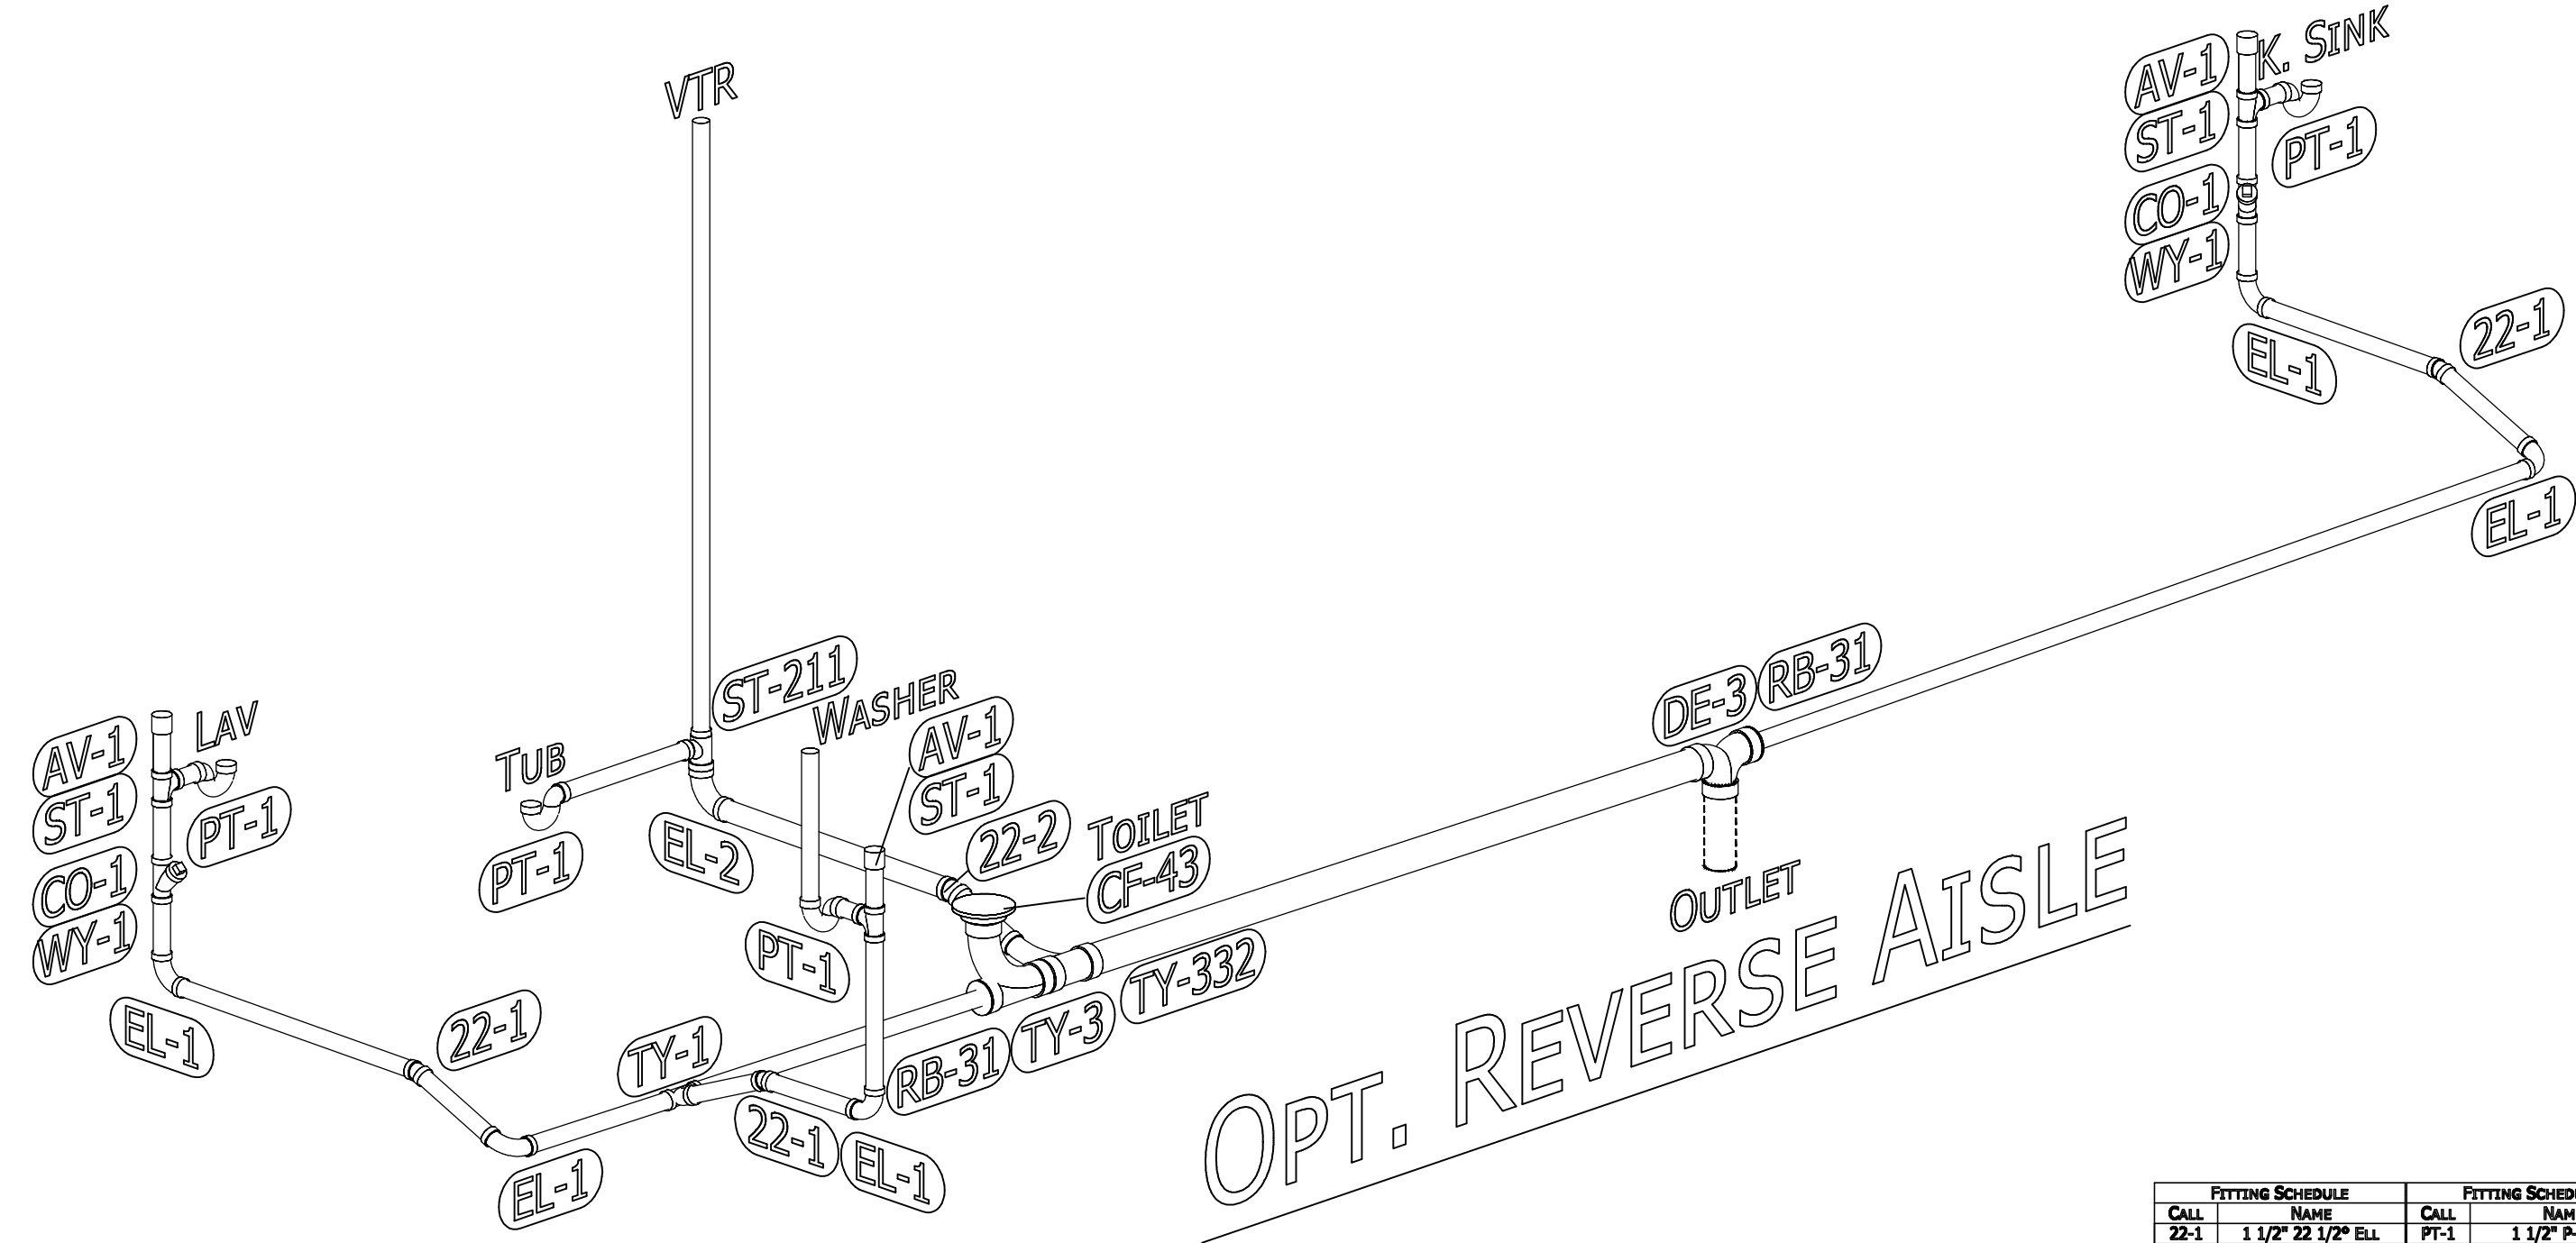

FITTING SCHEDULE		FITTING SCHEDULE	
CALL	NAME	CALL	NAME
22-1	1 1/2" 22 1/2° ELL	PT-1	1 1/2" P-TRAP
22-2	2" 22 1/2° ELL	RB-31	3" x 1 1/2" BUSHING
AV-1	1 1/2" AUTO VENT	ST-1	1 1/2" TEE
CF-43	4" x 3" CLOSET FLANGE	ST-211	2" x 1 1/2" x 1 1/2" TEE
CO-1	1 1/2" CLEANOUT	TY-1	1 1/2" LTTY
DE-3	3" DOUBLE ELL	TY-3	3" LTTY
EL-1	1 1/2" LT 90° ELL	TY-332	3" x 3" x 2" LTTY
EL-2	2" LT 90° ELL	WY-1	1 1/2" WYE

CHAMPION

HOME BUILDERS

755 W. BIG BEAVER ROAD, SUITE 1000 TROY, MI 48064
PHONE: 248-614-8200



MODIFICATIONS

PROJECT:
112AP-1456H21023
56'-0" x 13'-4"
2BD 1BT

DRAWN BY: KG
DATE: 08-21-23
SCALE: N.T.S.

TITLE:
DRAIN LINE
PLAN


FILENAME: 112AP-1456H21023

SHEET:
D-102

PROPRIETARY AND CONFIDENTIAL
THESE DRAWINGS AND SPECIFICATIONS ARE ORIGINAL,
PROPRIETARY AND CONFIDENTIAL MATERIALS OF CHAMPION.
COPYRIGHT © 1976-2024 BY CHAMPION

NOTES:

- 1. ALL PIPE SIZES 1/2" UNLESS OTHERWISE SPECIFIED
- 2. TOTAL BTU = 145,000(202,000 w/OPTIONS)
- 3. COLUMN LENGTH = 30'-0"

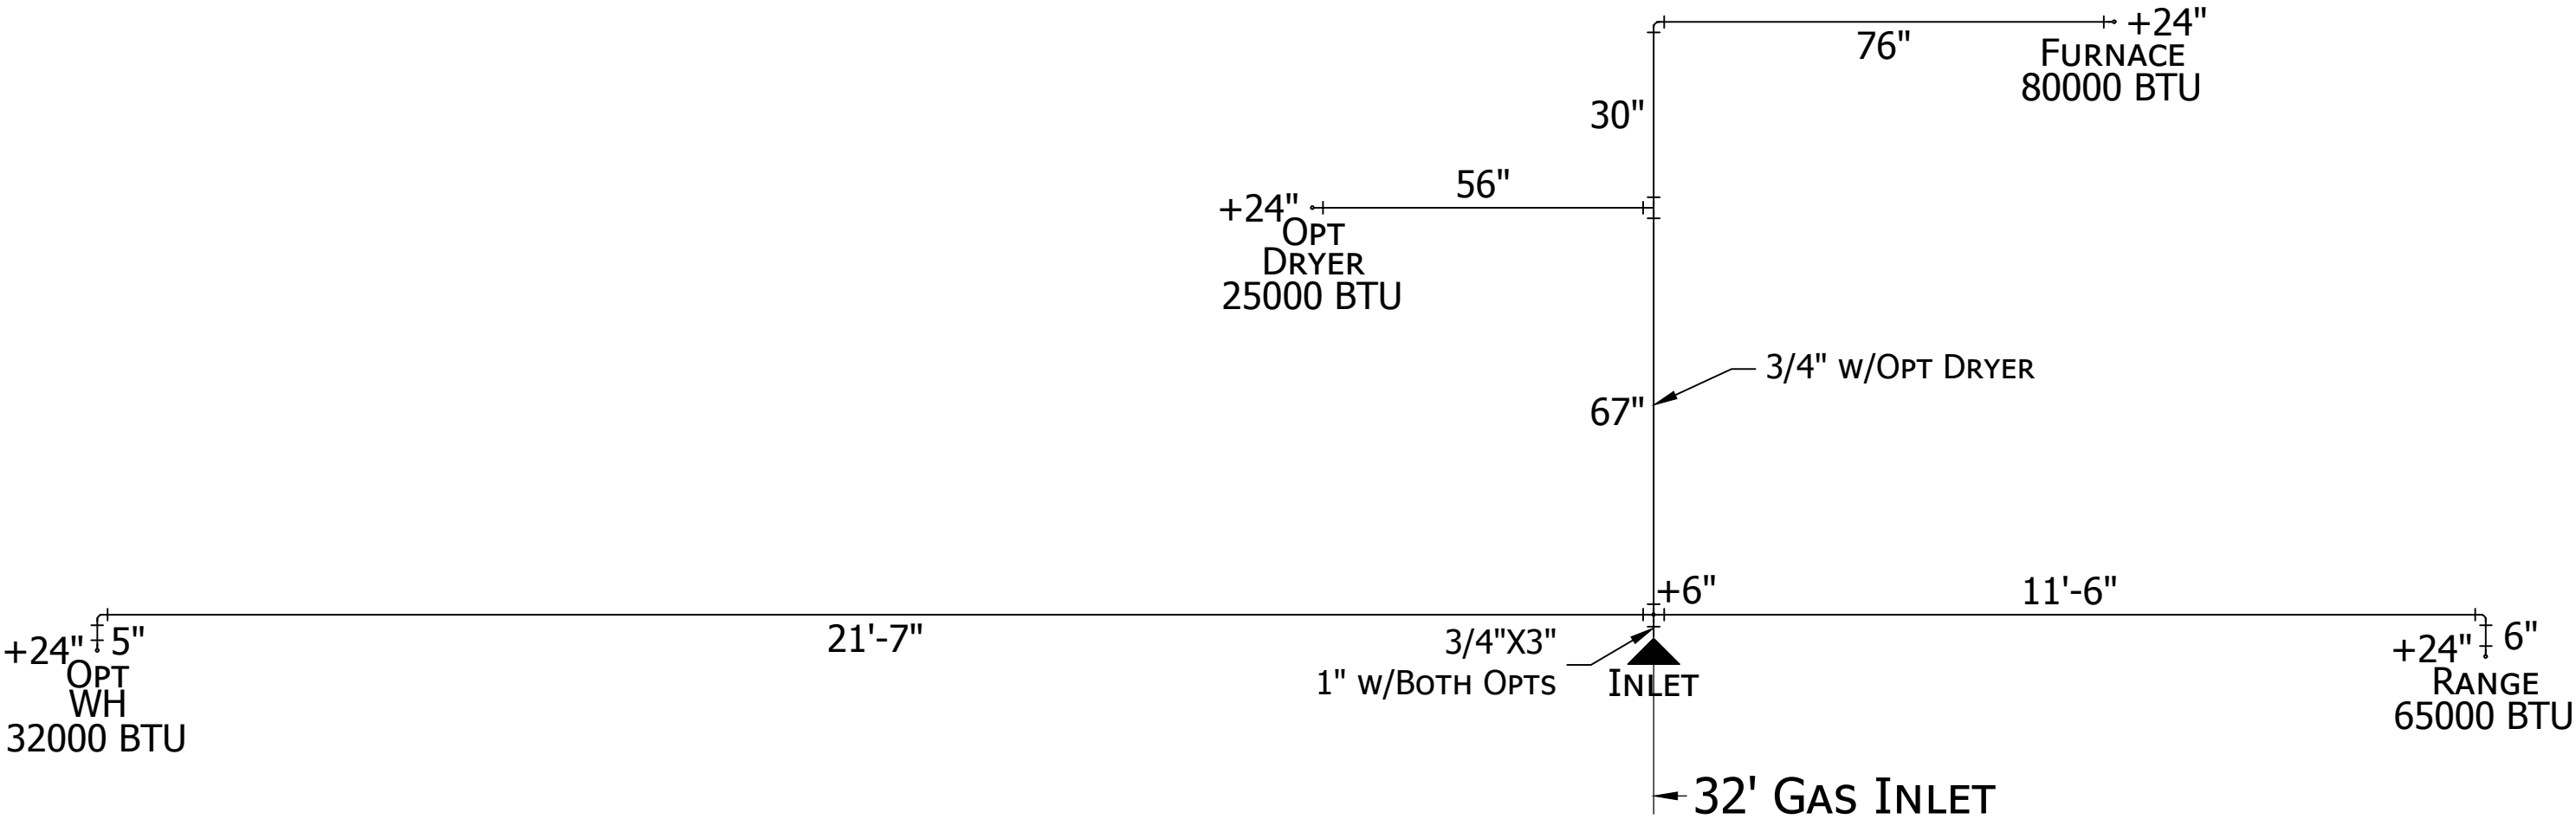

CHAMPION

HOME BUILDERS

755 W. BIG BEAVER ROAD, SUITE 1000 TROY, MI 48064
PHONE: 248-614-8200



MODIFICATIONS

PROJECT:
112AP-1456H21023
56'-0" x 13'-4"
2BD 1BT

DRAWN BY: KG

DATE: 08-21-23

SCALE: N.T.S.

TITLE:
GAS LINE
PLAN


FILENAME: 112AP-1456H21023

SHEET:
G-101

PROPRIETARY AND CONFIDENTIAL
THESE DRAWINGS AND SPECIFICATIONS ARE ORIGINAL,
PROPRIETARY AND CONFIDENTIAL MATERIALS OF CHAMPION.
COPYRIGHT © 1976-2024 BY CHAMPION

NOTES:

- 1. ALL PIPE SIZES 1/2" UNLESS OTHERWISE SPECIFIED
- 2. TOTAL BTU = 145,000(202,000 w/OPTIONS)
- 3. COLUMN LENGTH = 30'-0"

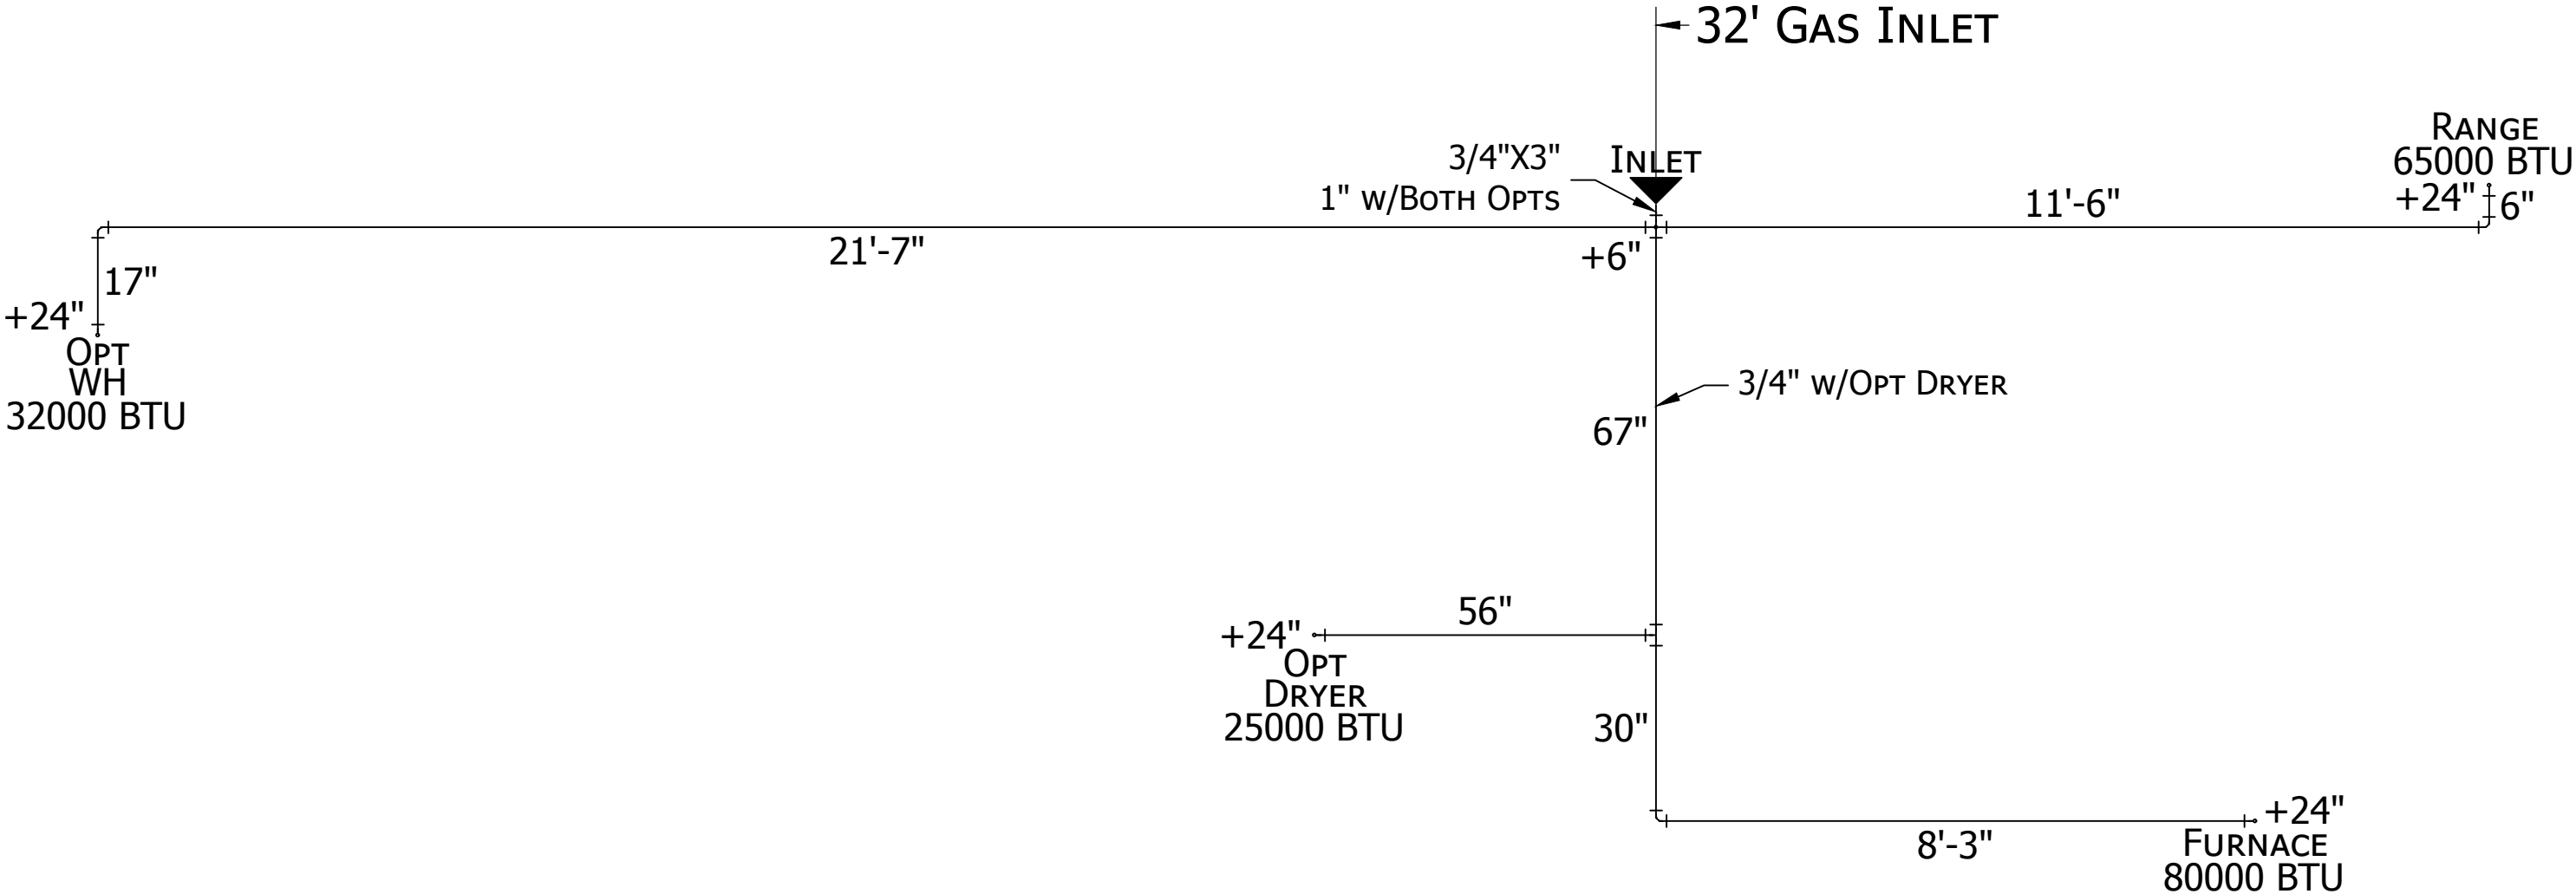

OPT. REVERSE AISLE



CHAMPION

HOME BUILDERS

755 W. BIG BEAVER ROAD, SUITE 1000 TROY, MI 48064
PHONE: 248-614-8200



MODIFICATIONS

PROJECT:
112AP-1456H21023
56'-0" x 13'-4"
2BD 1BT

DRAWN BY: KG

DATE: 08-21-23

SCALE: N.T.S.

TITLE:
GAS LINE
PLAN

FILENAME: 112AP-1456H21023

SHEET:
G-102

PROPRIETARY AND CONFIDENTIAL
THESE DRAWINGS AND SPECIFICATIONS ARE ORIGINAL,
PROPRIETARY AND CONFIDENTIAL MATERIALS OF CHAMPION.
COPYRIGHT © 1976-2024 BY CHAMPION