




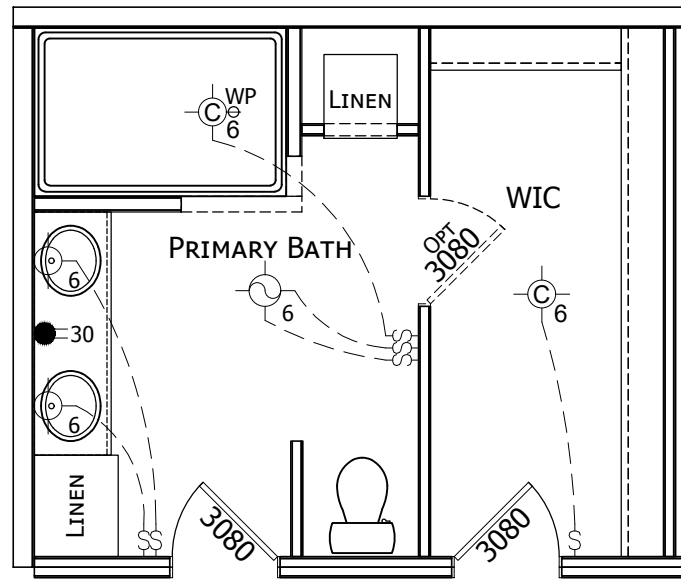


OPTIONAL SERENITY BATH

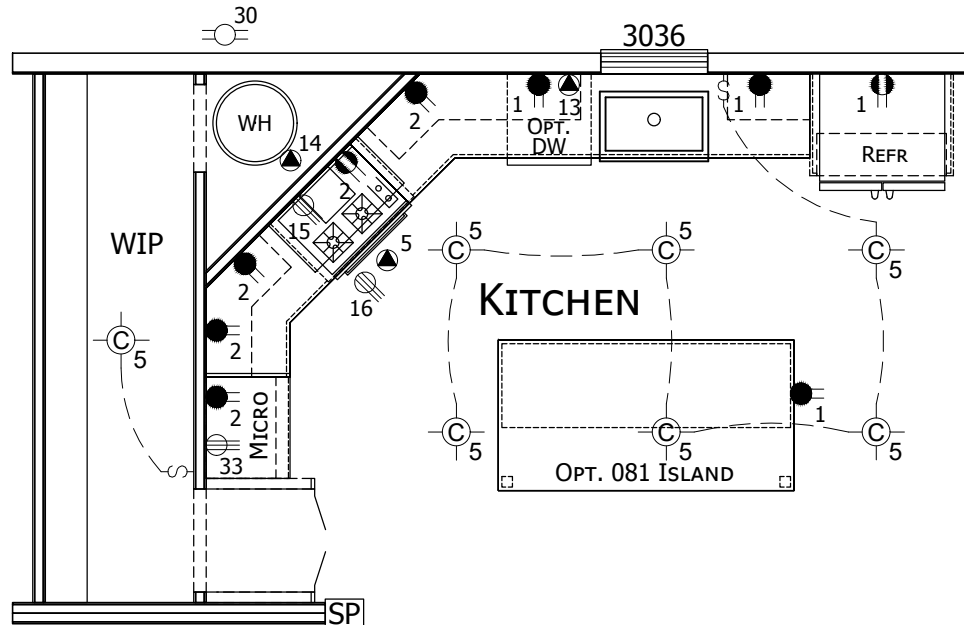


OPTIONAL ULTIMATE KITCHEN 2

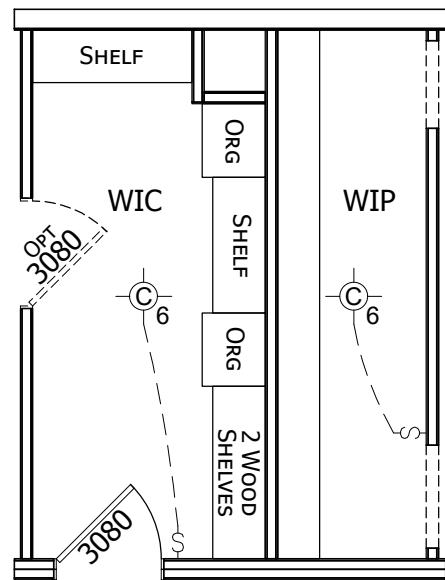

OPTIONAL CLOSET ORGANIZER

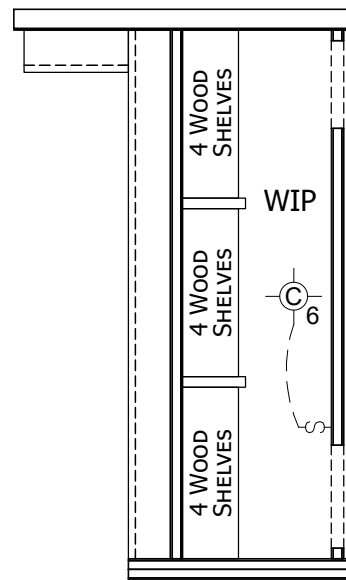

OPTIONAL PANTRY ORGANIZER

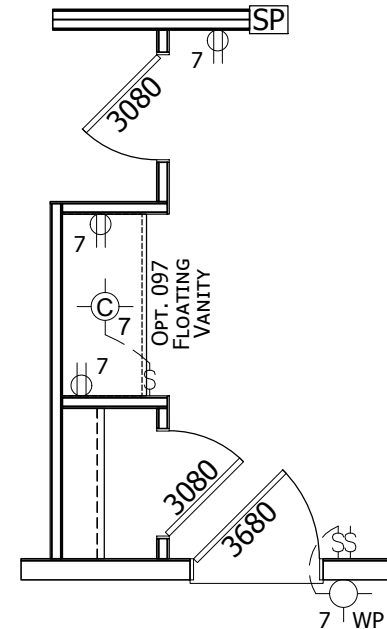

OPTIONAL FLOATING VANITY

**CHAMPION
HOME BUILDERS**

755 W. BIG BEAVER ROAD, SUITE 1000 TROY, MI 48064
PHONE: 248-614-8200

PFS #23
Conforms to
HUD MHCSS
2/21/24

MODIFICATIONS

PROJECT:
112APB-2860H32047
60'-0" x 26'-8"
3BD 2BT

DRAWN BY: T. COWLEY
DATE: 10-23-23
SCALE: 5/32" = 1'-0"

TITLE:
**FLOOR PLAN
ELECTRICAL PLAN**

FILENAME: 112APB-2860H32047
WAS 2864 225


SHEET:
AE-102

PROPRIETARY AND CONFIDENTIAL
THESE DRAWINGS AND SPECIFICATIONS ARE ORIGINAL,
PROPRIETARY AND CONFIDENTIAL MATERIALS OF CHAMPION.
COPYRIGHT © 1976-2024 BY CHAMPION

Overall Check =		PASS	CHB Shear Wall - Layout / Design										Model#:	112APB-2860H32047									
Wind Zone =		I	Diaphragm Construction:										Fasteners		Wall Construction:								
Wind Load =		15	psf	Diaphragm Type =		Wood Roof		15GAx1.75							Ground Tie Chart								
Module Width =		160	in	Minimum Width =				in		Bottom Plate Thickness =		2x											
Number of Boxes =		2		Max plf =		176.3		plf		Top Plate Thickness =		2x											
Wall Height =		96	in	Max. End Wall Reaction =		4,701		lbs		Wall to Floor Joist =		#10 x 3.5"											
Roof Pitch =		4.36	:12	Max. Interior Reaction =		9,403		lbs		Wall to Ceiling Framing =		#10 x 3.5"											
Angle =		20.0	°	Max. Span =		112.00		ft.		Wall to Wall Fastener =		#10 x 3.50"											
Roof Overhang =		8	in																				
Floor Joist Spacing =		16	in o.c.	Floor Construction:																			
Rim Joist Plies =		1																					
Frame Spacing =		99.5	in	Floor Joist Size =		2x6																	
Beam Depth =		12	in	Floor Joist Species =		SPF																	
Open Porch =		0.00	ft.	Floor Joist Grade =		#3																	
Home Length =		60.00	ft.	Decking Glued to Joists =		Yes																	
															* For monoslope homes only								
Vertical Trib =		4.00	ft	Vertical Trib =		4.00		ft		Vertical Trib =		4.00		ft		Vertical Trib =		4.00		ft			
King Post Height *=			in.	King Post Height *=				in.		King Post Height *=				in.		King Post Height *=				in.			
Porch End Wall =		--		Porch End Wall =		--				Porch End Wall =		--				Porch End Wall =		--					
Left End Wall Shear Wall				Shear Wall 2				Shear Wall 3				Shear Wall 4				Shear Wall 5				Shear Wall 6			
Dist. To Next SW =		60.00	ft.	Dist. To Next SW =				ft.		Dist. To Next SW =				ft.		Dist. To Next SW =				ft.			
Manual Input =		--		Manual Input =		--				Manual Input =		--				Manual Input =		--					
Load to Shearwall =		1800.0	lbs	Load to Shearwall =		1800.0		lbs		Load to Shearwall =		0.0		lbs		Load to Shearwall =		0.0		lbs			
Panel Layout				Panel Layout				Panel Layout				Panel Layout				Panel Layout				Panel Layout			
From Module Edge =		6.00	in.	From Module Edge =		6.00		in.		From Module Edge =				in.		From Module Edge =				in.			
Panel Length =		108.00	in.	Panel Length =		108.00		in.		Panel Length =				in.		Panel Length =				in.			
From Module Edge =			in.	From Module Edge =				in.		From Module Edge =				in.		From Module Edge =				in.			
Panel Length =			in.	Panel Length =				in.		Panel Length =				in.		Panel Length =				in.			
Shearwall plf =		200.0	plf	Shearwall plf =		200.0		plf		Shearwall plf =		N/A		plf		Shearwall plf =		N/A		plf			
Shearwall Panel =		Gypsum		Shearwall Panel =		Gypsum				Shearwall Panel =						Shearwall Panel =							
Gyp. Brand =		U.S.G.		Gyp. Brand =		U.S.G.				Gyp. Brand =						Gyp. Brand =							
Fasteners =		Yes		Fasteners =		Yes				Fasteners =						Fasteners =							
Adhesive =		PVA		Adhesive =		PVA				Adhesive =						Adhesive =							
One Side or Two =		1		One Side or Two =		1				One Side or Two =						One Side or Two =							
Max. Shearwall plf =		247	plf	Max. Shearwall plf =		247		plf		Max. Shearwall plf =				plf		Max. Shearwall plf =				plf			
*Construct per Note 6 on SW01.35.XX				*Construct per Note 6 on SW01.35.XX				*Construct per SW01.25.01				*Construct per SW01.25.01				*Construct per SW01.25.01				*Construct per SW01.25.01			
Zone - ID		Z1-1		Zone - ID		Z1-2		Zone - ID		Zone - ID		Zone - ID		Zone - ID		Zone - ID		Zone - ID		Zone - ID			
Joist		3		Joist		3		Joist		Joist		Joist		Joist		Joist		Joist		Joist			
Wall Conn.		8		Wall Conn.		8		Wall Conn.		Wall Conn.		Wall Conn.		Wall Conn.		Wall Conn.		Wall Conn.		Wall Conn.			
SC O.C.		18 @ 6"		SC O.C.		18 @ 6"		SC O.C.		SC O.C.		SC O.C.		SC O.C.		SC O.C.		SC O.C.		SC O.C.			
SF O.C.		22 @ 5"		SF O.C.		22 @ 5"		SF O.C.		SF O.C.		SF O.C.		SF O.C.		SF O.C.		SF O.C.		SF O.C.			
Beam Lag		2		Beam Lag		2		Beam Lag		Beam Lag		Beam Lag		Beam Lag		Beam Lag		Beam Lag		Beam Lag			
*May be 1 joist per Note 9.C. on SW01.00.04				*May be 1 joist per Note 9.C on SW01.00.04																			
Result =		PASS		Result =		PASS		Result =		Result =		Result =		Result =		Result =		Result =		Result =			

NOTES:

- 1. PIPE SIZES DETERMINED BY FITTINGS ON EACH SIDE.
- 2. SITE INSTALLED PLUMBING NOTED BY ----- .

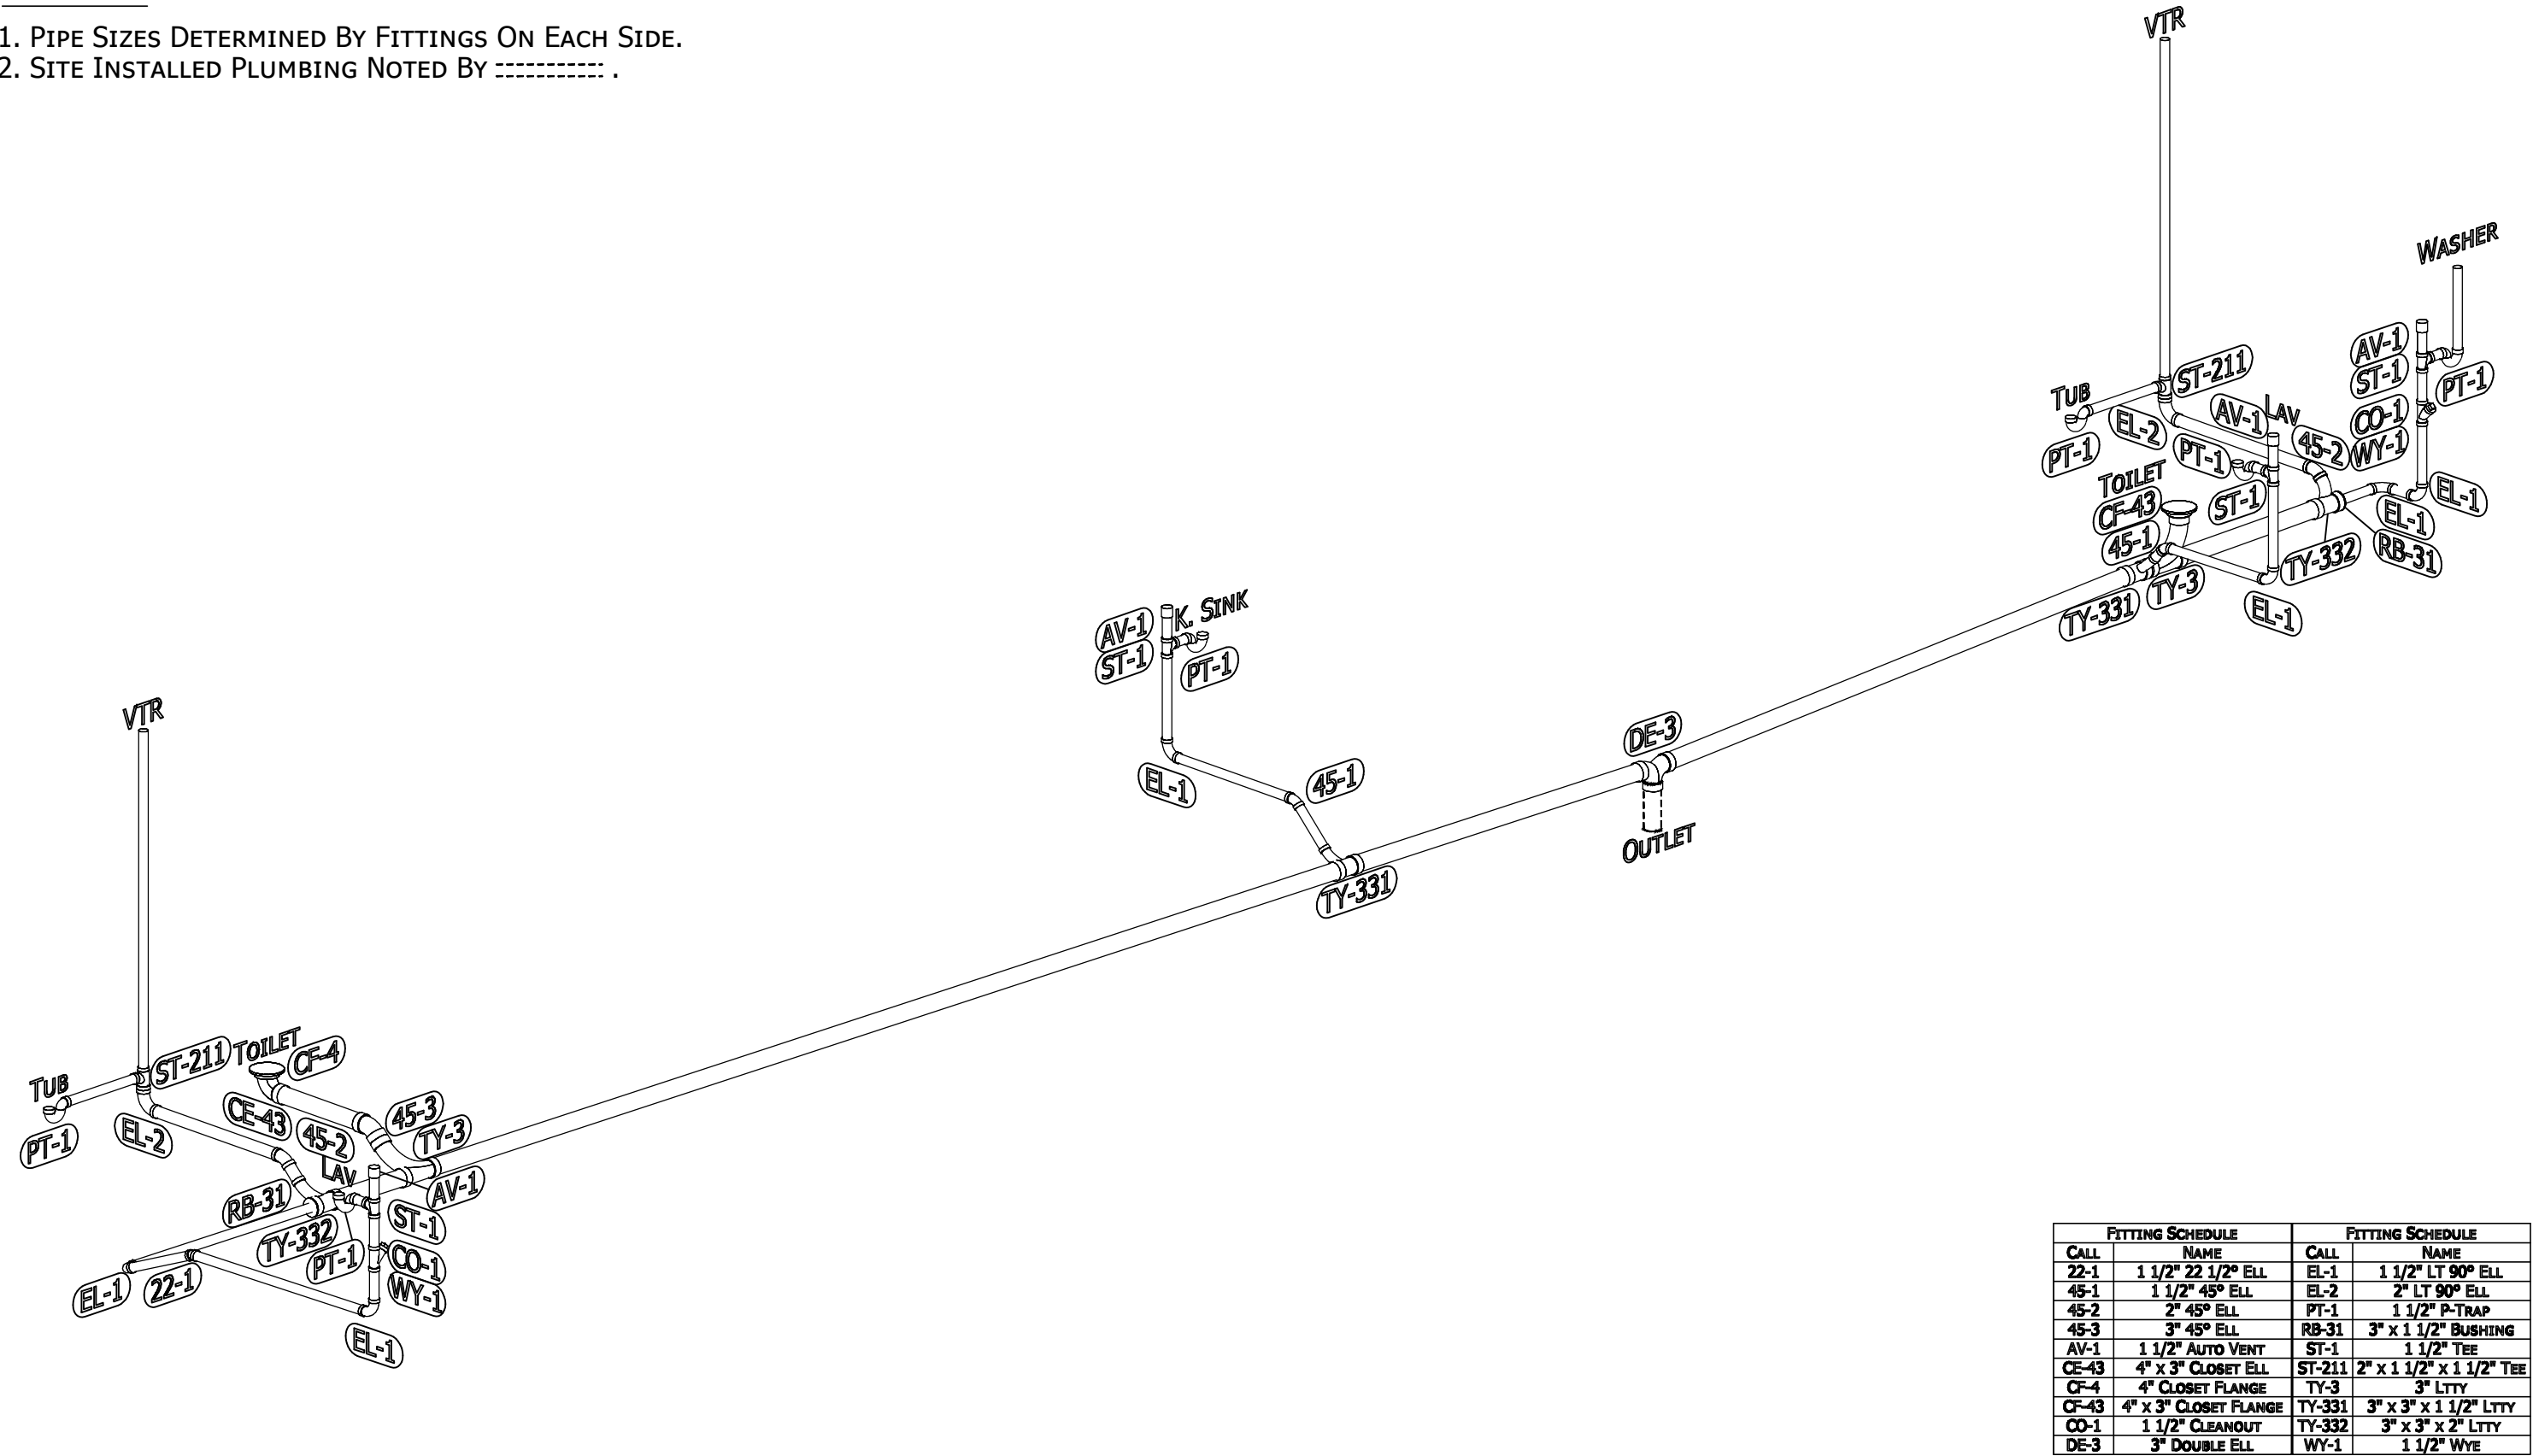

FITTING SCHEDULE		FITTING SCHEDULE	
CALL	NAME	CALL	NAME
22-1	1 1/2" 22 1/2° ELL	EL-1	1 1/2" LT 90° ELL
45-1	1 1/2" 45° ELL	EL-2	2" LT 90° ELL
45-2	2" 45° ELL	PT-1	1 1/2" P-TRAP
45-3	3" 45° ELL	RB-31	3" x 1 1/2" BUSHING
AV-1	1 1/2" AUTO VENT	ST-1	1 1/2" TEE
CE-43	4" x 3" CLOSET ELL	ST-211	2" x 1 1/2" x 1 1/2" TEE
CF-4	4" CLOSET FLANGE	TY-3	3" LT TY
CF-43	4" x 3" CLOSET FLANGE	TY-331	3" x 3" x 1 1/2" LT TY
CO-1	1 1/2" CLEANOUT	TY-332	3" x 3" x 2" LT TY
DE-3	3" DOUBLE ELL	WY-1	1 1/2" WYE

CHAMPION

HOME BUILDERS

755 W. BIG BEAVER ROAD, SUITE 1000 TROY, MI 48064
PHONE: 248-614-8200

PFS

#23

Conforms to
HUD MHCSS
2/21/24

MODIFICATIONS

PROJECT:
112APB-2860H32047
60'-0" x 26'-8"
3BD 2BT

DRAWN BY: T. COWLEY
DATE: 10-23-23
SCALE: 3/16" = 1'-0"

TITLE:
DRAIN LINE
PLAN



FILENAME: 112APB-2860H32047
WAS 2864 225

SHEET:
D-101

PROPRIETARY AND CONFIDENTIAL
THESE DRAWINGS AND SPECIFICATIONS ARE ORIGINAL,
PROPRIETARY AND CONFIDENTIAL MATERIALS OF CHAMPION.
COPYRIGHT © 1976-2024 BY CHAMPION

NOTES:

- 1. PIPE SIZES DETERMINED BY FITTINGS ON EACH SIDE.
- 2. SITE INSTALLED PLUMBING NOTED BY ----- .

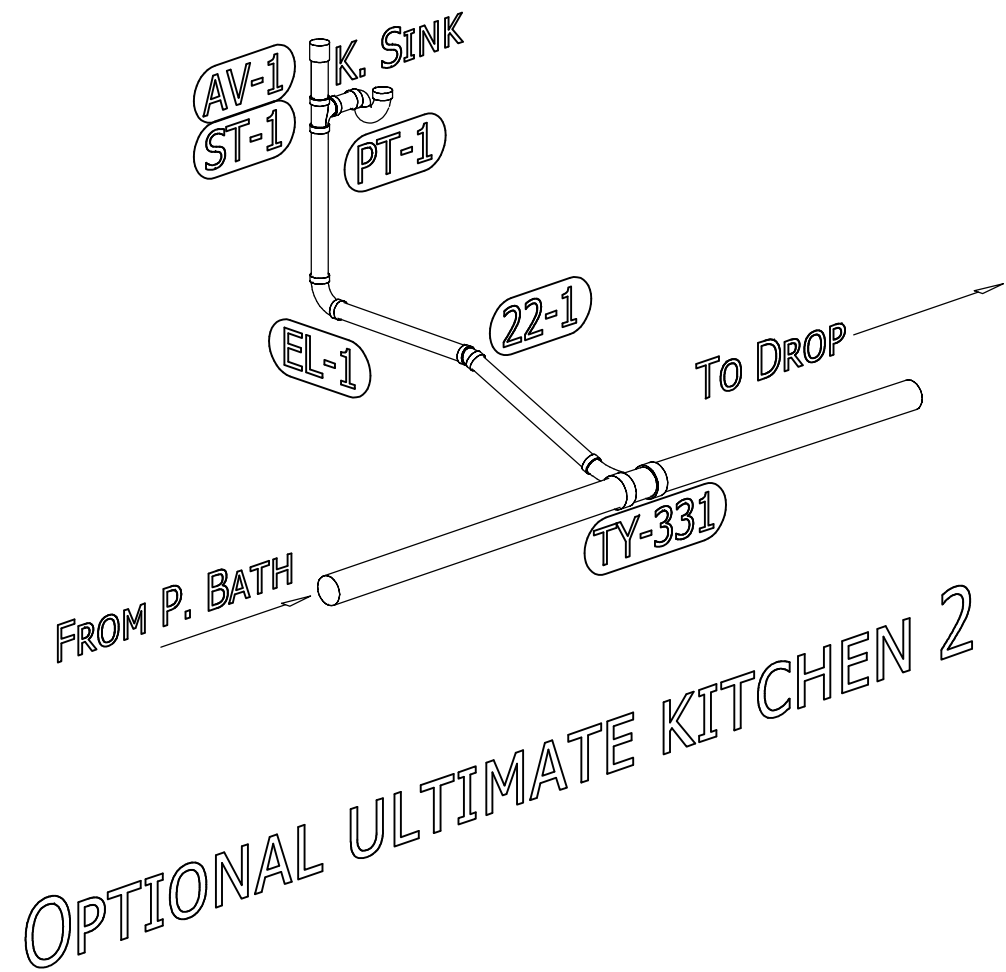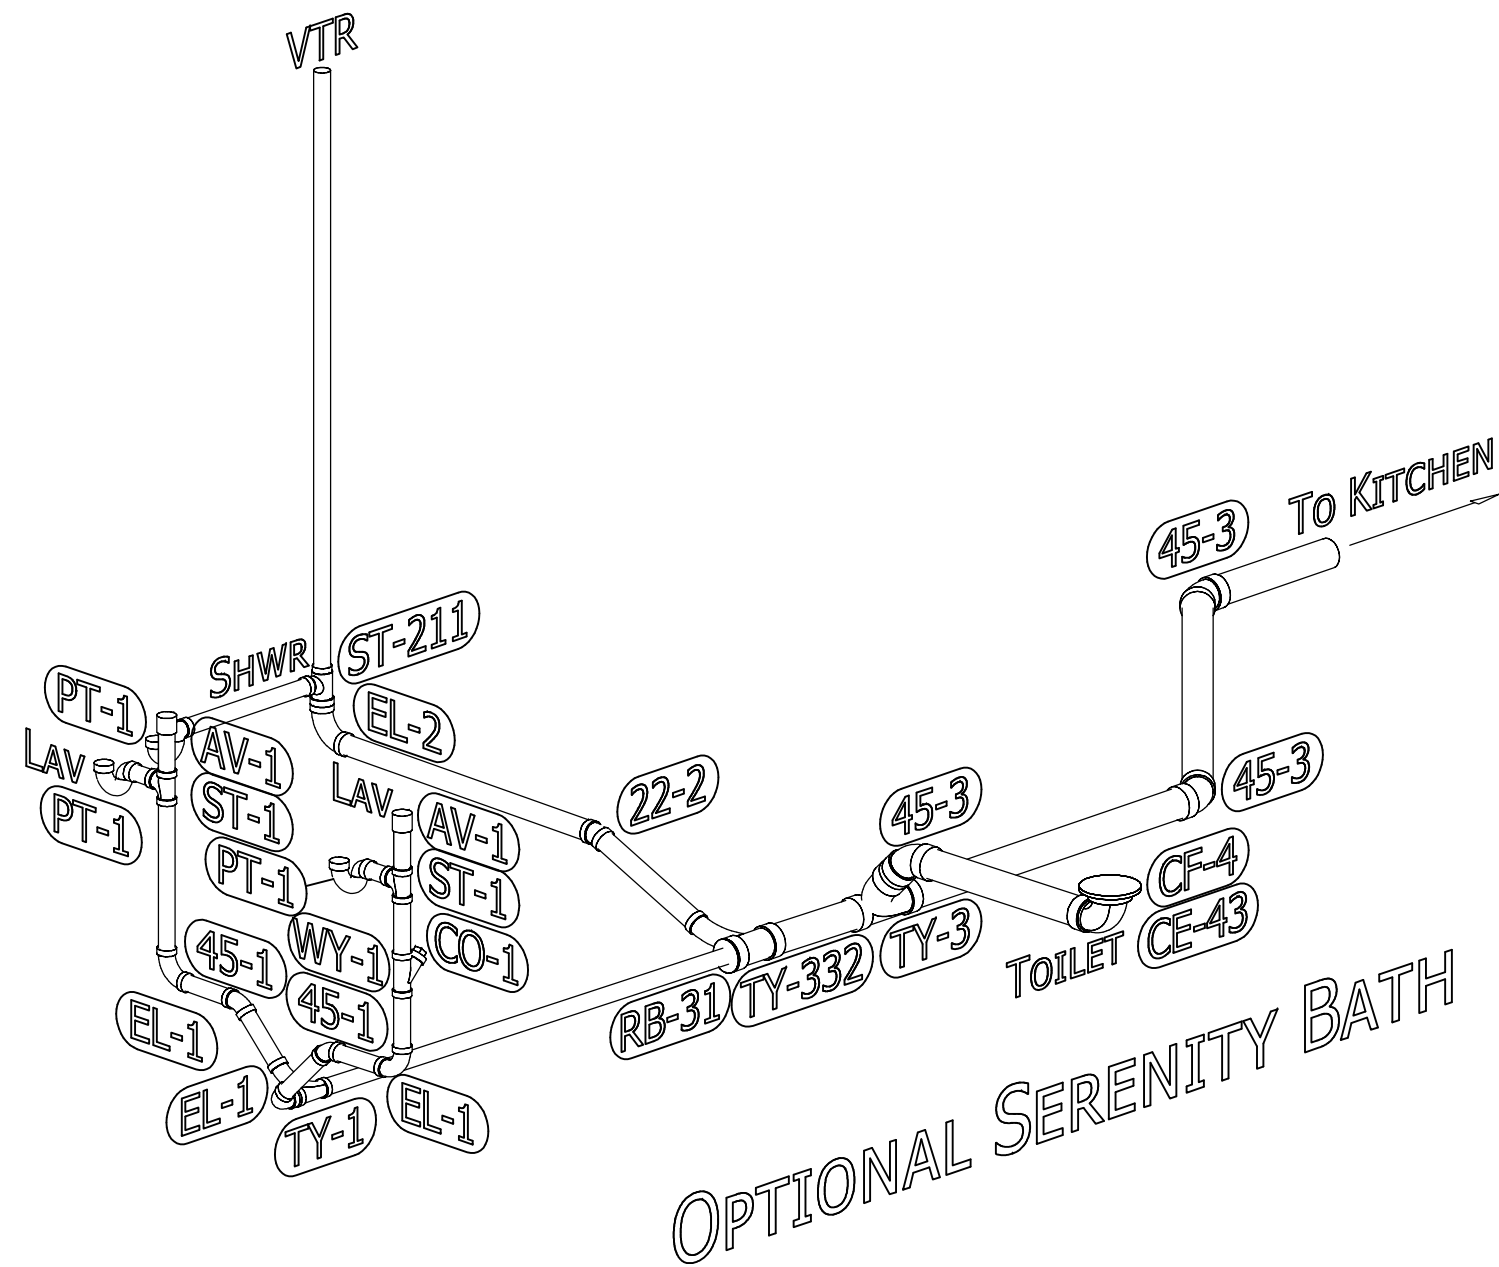

FITTING SCHEDULE		FITTING SCHEDULE	
CALL	NAME	CALL	NAME
22-1	1 1/2" 22 1/2° ELL	PT-1	1 1/2" P-TRAP
22-2	2" 22 1/2° ELL	RB-31	3" x 1 1/2" BUSHING
45-1	1 1/2" 45° ELL	ST-1	1 1/2" TEE
45-3	3" 45° ELL	ST-211	2" x 1 1/2" x 1 1/2" TEE
AV-1	1 1/2" AUTO VENT	TY-1	1 1/2" LTTY
CE-43	4" x 3" CLOSET ELL	TY-3	3" LTTY
CF-4	4" CLOSET FLANGE	TY-331	3" x 3" x 1 1/2" LTTY
CO-1	1 1/2" CLEANOUT	TY-332	3" x 3" x 2" LTTY
EL-1	1 1/2" LT 90° ELL	WY-1	1 1/2" WYE
EL-2	2" LT 90° ELL		

CHAMPION

HOME BUILDERS

755 W. BIG BEAVER ROAD, SUITE 1000, TROY, MI 48064
PHONE: 248-614-8900

PFS#23

Conforms to
HUD MHCSS
2/21/24

MODIFICATIONS

PROJECT:
112APB-2860H32047
60'-0" x 26'-8"
3BD 2BT

DRAWN BY: T. COWLEY
DATE: 10-23-23
SCALE: 3/16" = 1'-0"

TITLE:
DRAIN LINE
PLAN
OPTIONS


FILENAME: 112APB-2860H32047
WAS 2864 225

SHEET:
D-102

PROPRIETARY AND CONFIDENTIAL
THESE DRAWINGS AND SPECIFICATIONS ARE ORIGINAL,
PROPRIETARY AND CONFIDENTIAL MATERIALS OF CHAMPION.
COPYRIGHT © 1976-2024 BY CHAMPION


NOTES:

- 1. ALL PIPE SIZES 1/2" UNLESS OTHERWISE SPECIFIED
- 2. TOTAL BTU = 145,000(202,000 w/OPTIONS)
- 3. COLUMN LENGTH = 30'-0"

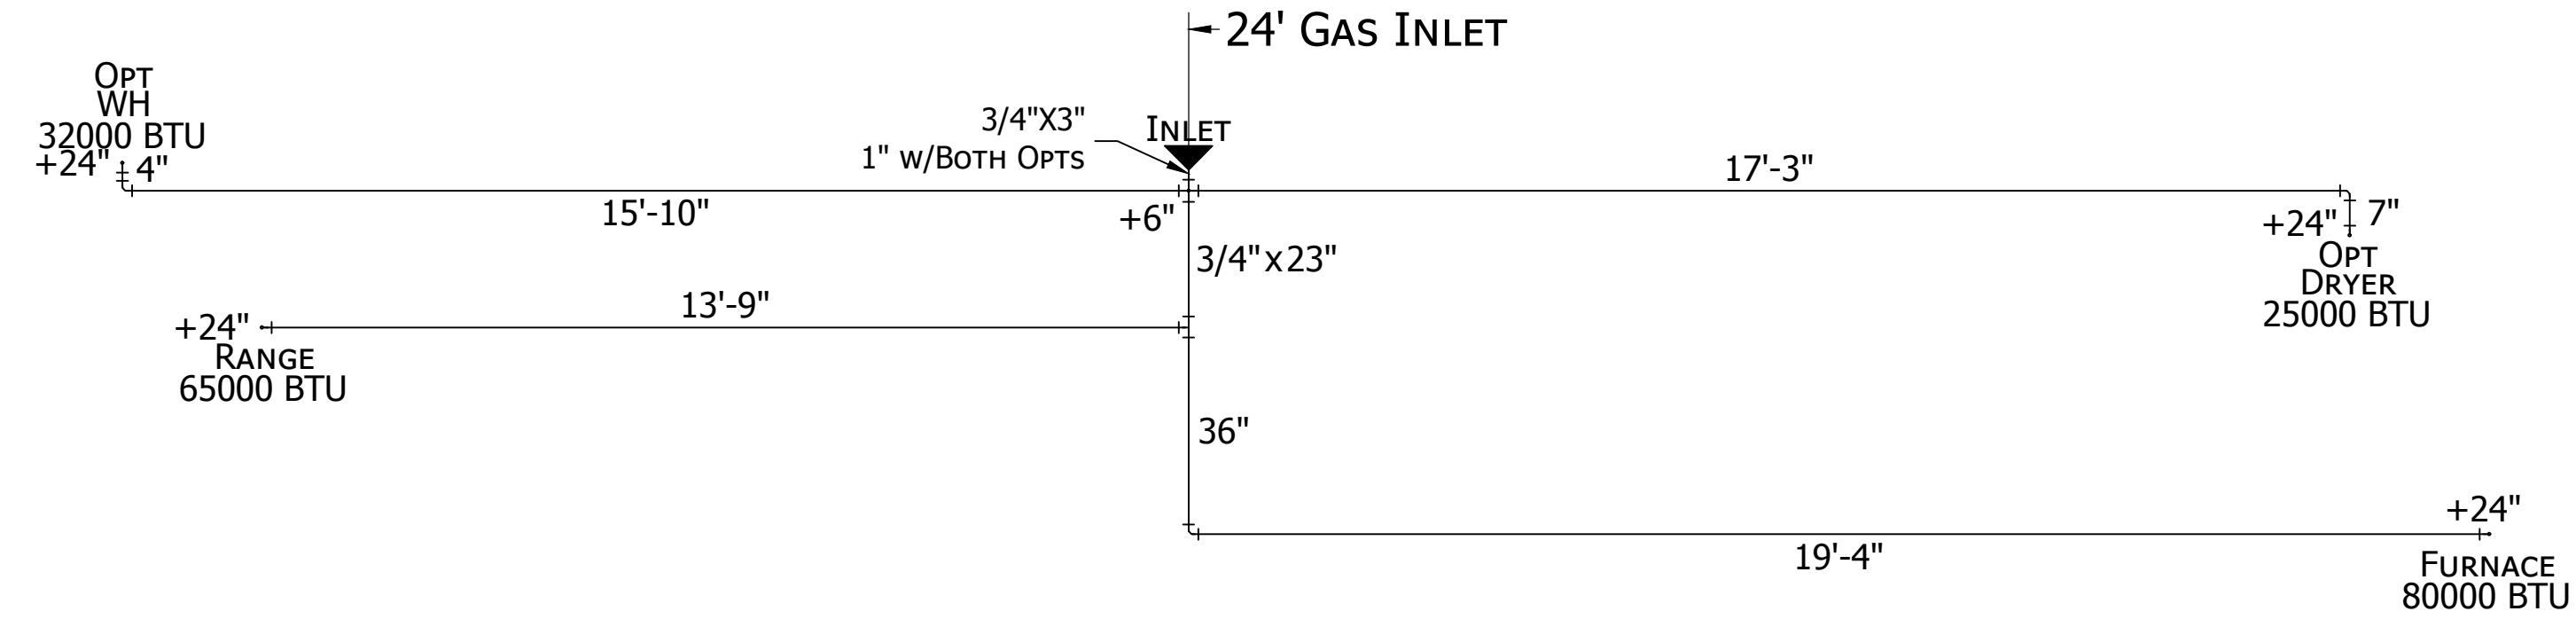

NOTES:

- 1. ALL PIPE SIZES 1/2" UNLESS OTHERWISE SPECIFIED
- 2. TOTAL BTU = 110,000(167,000 w/OPTIONS)
- 3. COLUMN LENGTH = 30'-0"

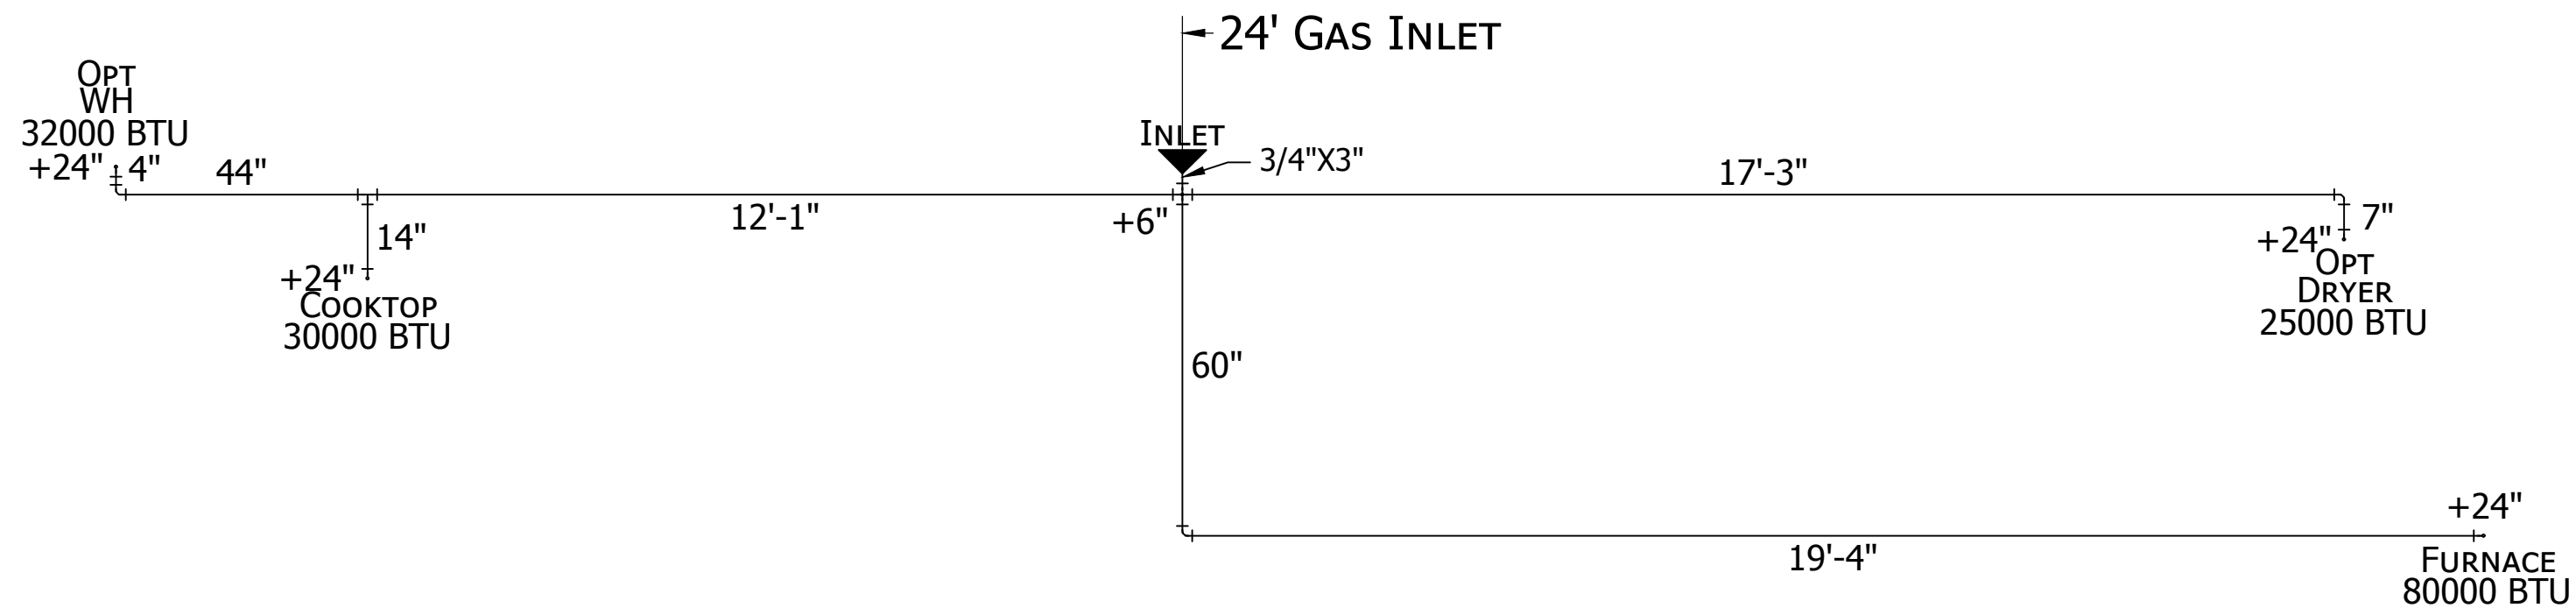

OPTIONAL ULTIMATE KITCHEN 2

CHAMPION
HOME BUILDERS

755 W. BIG BEAVER ROAD, SUITE 1000 TROY, MI 48064
PHONE: 248-614-8200



MODIFICATIONS

PROJECT:
112APB-2860H32047
60'-0" x 26'-8"
3BD 2BT

DRAWN BY: T. COWLEY
DATE: 10-23-23
SCALE: 3/16" = 1'-0"

TITLE:
GAS LINE
PLAN
OPTIONS

FILENAME: 112APB-2860H32047
WAS 2864 225

SHEET:
G-102

PROPRIETARY AND CONFIDENTIAL
THESE DRAWINGS AND SPECIFICATIONS ARE ORIGINAL,
PROPRIETARY AND CONFIDENTIAL MATERIALS OF CHAMPION.
COPYRIGHT © 1976-2024 BY CHAMPION