




CHAMPION
HOME BUILDERS

755 W. BIG BEAVER ROAD, SUITE 1000 TROY, MI 48064
PHONE: 248-614-8200

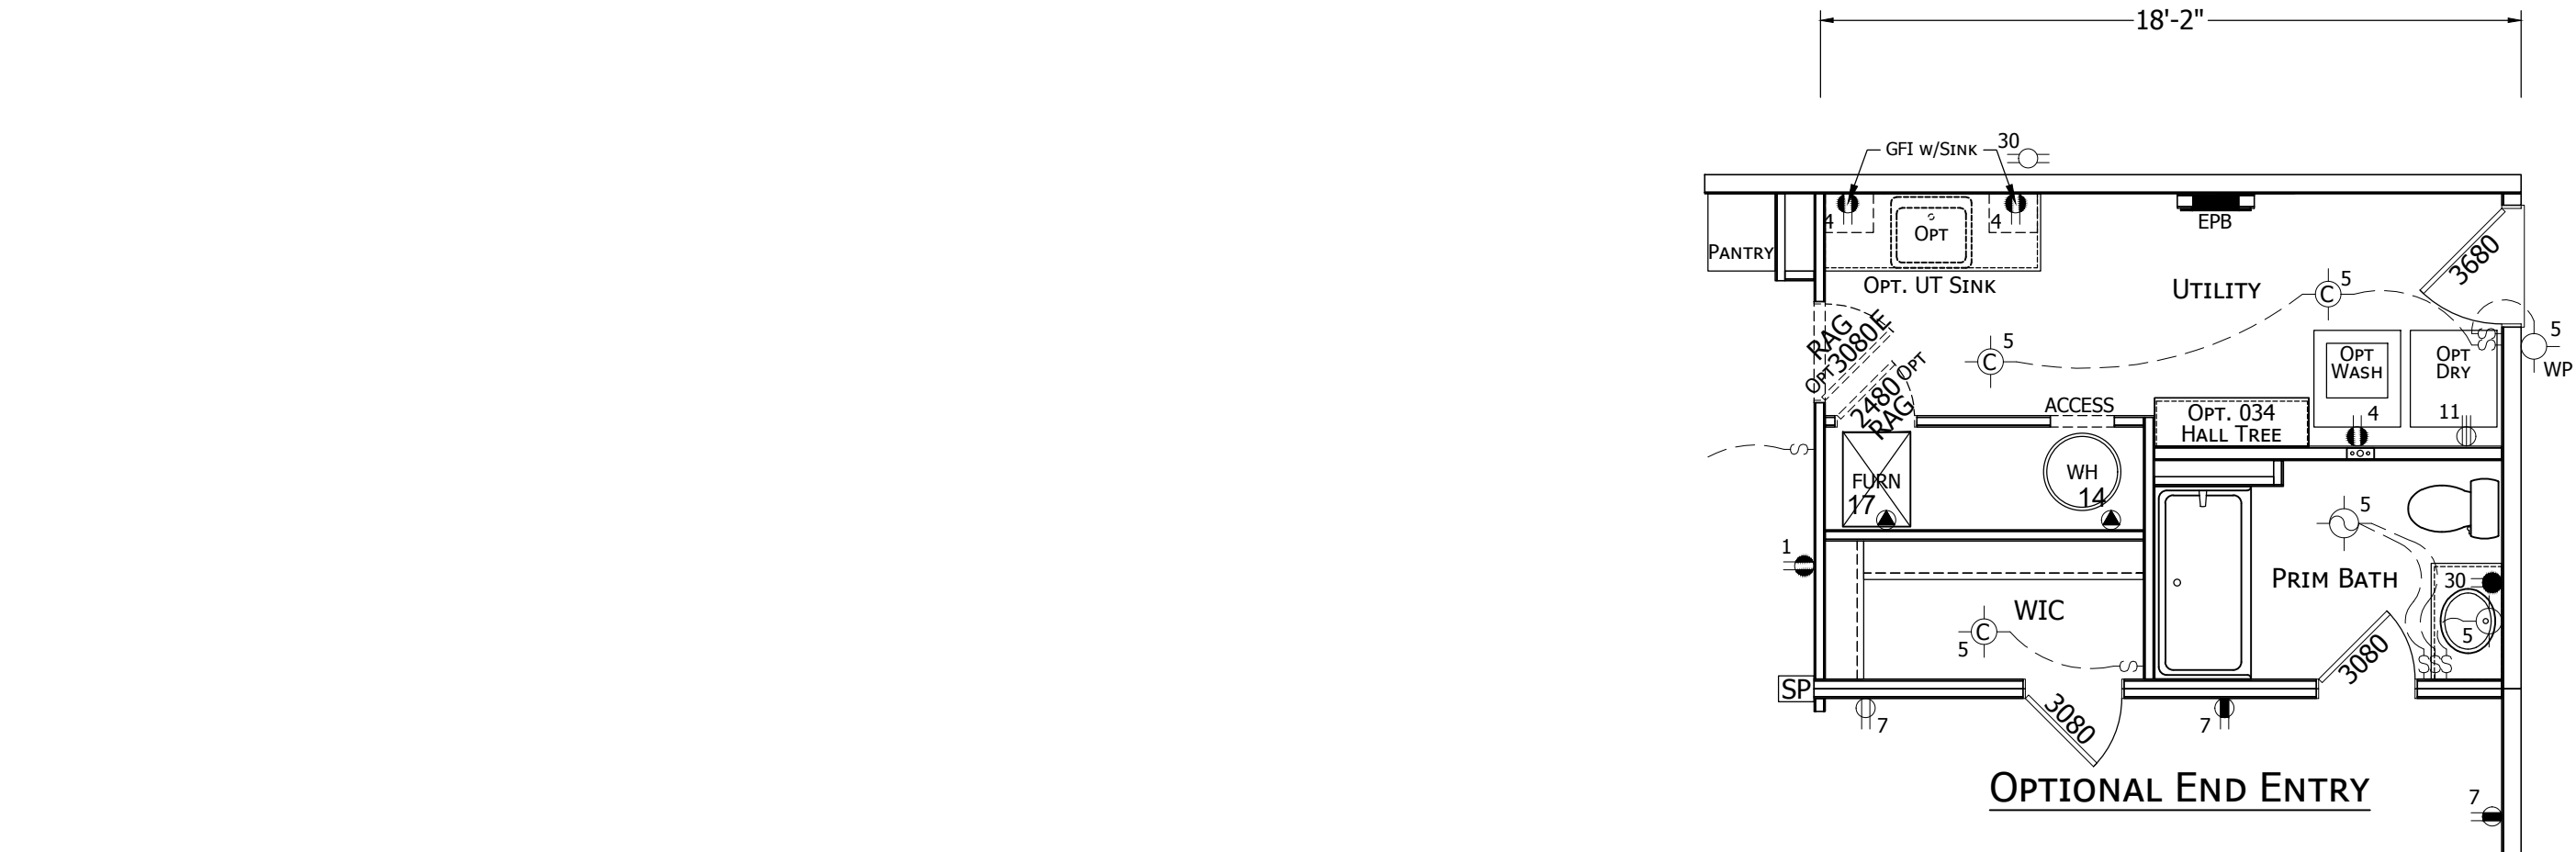

MODIFICATIONS	
1	ADDED OPT. END ENTRY 1/28/25 KG

PROJECT:
112APB-2856H32171
56'-0" x 26'-8"
3BD 2BT
DRAWN BY: STAFF
DATE: 04-21-24
SCALE: 5/32" = 1'-0"

TITLE:
FLOOR PLAN
ELECTRICAL PLAN
FILENAME: 112APB-2856H32171

SHEET:
AE-102
PROPRIETARY AND CONFIDENTIAL
THESE DRAWINGS AND SPECIFICATIONS ARE ORIGINAL, PROPRIETARY AND CONFIDENTIAL MATERIALS OF CHAMPION. COPYRIGHT © 1976-2025 BY CHAMPION

Overall Check = PASS

CHB Shear Wall - Layout / Design

Model#: 112APB-2856H32171

Wind Zone = I

Wind Load = 15 psf

Diaphragm Construction:

Diaphragm Type = Gypsum Ceiling

Foam Brand = F-2100

Minimum Width = 160 in

Max plf = 219 plf

Wall Construction:

Bottom Plate Thickness = 2x

Top Plate Thickness = 2x

Module Width = 160 in

Number of Boxes = 2

Wall Height = 96 in

Roof Pitch = 5 :12

Angle = 22.6 °

Roof Overhang = 8 in

Floor Joist Spacing = 16 in o.c.

Rim Joist Plies = 1

Frame Spacing = 99.5 in

Beam Depth = 12 in

Open Porch = 0.00 ft.

Home Length = 56.00 ft.

Max. End Wall Reaction = 5,840 lbs

Max. Interior Reaction = 11,680 lbs

Max. Span = 48.00 ft.

Floor Construction:

Floor Joist Size = 2x6

Floor Joist Species = SPF

Floor Joist Grade = #3

Decking Glued to Joists = Yes

Wall to Floor Joist = #10 x 3.5"

Wall to Ceiling Framing = #10 x 3.5"

Wall to Wall Fastener = #10 x 3.50"

Ground Tie Chart

Peir Height (in.)	Near Beam Angle (Deg.)	Far Beam Angle (Deg.)	Ground Tie Spacing (ft)	Max. Spacing (ft.)
12	42.44		11.48	11'-5"
20	50.64		9.87	9'-10"
28	56.73		8.62	8'-7"
36	61.33	20.89	14.53	14'-6"
44	64.89	24.00	14.21	14'-2"
52	67.70	26.97	13.86	13'-10"
60	69.97	29.79	13.50	13'-5"
68	71.83	32.46	13.12	13'-1"

* For monoslope homes only

Vertical Trib = 9.56 ft

King Post Height *= in.

Porch End Wall = --

Vertical Trib = 9.56 ft

King Post Height *= in.

Porch End Wall = --

Vertical Trib = 9.56 ft

King Post Height *= in.

Porch End Wall = --

Vertical Trib = 9.56 ft

King Post Height *= in.

Porch End Wall = --

Vertical Trib = 9.56 ft

King Post Height *= in.

Porch End Wall = --

Vertical Trib = 9.56 ft

King Post Height *= in.

Porch End Wall = --

Left End Wall Shear Wall

Dist. To Next SW = 18.17 ft.

Manual Input = --

Load to Shearwall = 1302.2 lbs

Shear Wall 2

Dist. To Next SW = 37.83 ft.

Manual Input = --

Load to Shearwall = 4013.3 lbs

Shear Wall 3

Dist. To Next SW = ft.

Manual Input = --

Load to Shearwall = 2711.2 lbs

Shear Wall 4

Dist. To Next SW = ft.

Manual Input = --

Load to Shearwall = 0.0 lbs

Shear Wall 5

Dist. To Next SW = ft.

Manual Input = --

Load to Shearwall = 0.0 lbs

Shear Wall 6

Dist. To Next SW = ft.

Manual Input = --

Load to Shearwall = 0.0 lbs

Panel Layout

From Module Edge = 6.00 in.

Panel Length = 108.00 in.

From Module Edge = in.

Panel Length = in.

Shearwall plf = 144.7 plf

Shearwall Panel = Gypsum

Gyp. Brand = U.S.G.

Fasteners = Yes

Adhesive = PVA

One Side or Two = 1

Max. Shearwall plf = 247 plf

Panel Layout

From Module Edge = 6.00 in.

Panel Length = 151.00 in.

From Module Edge = in.

Panel Length = in.

Shearwall plf = 318.9 plf

Shearwall Panel = Gypsum

Gyp. Brand = U.S.G.

Fasteners = Yes

Adhesive = PVA

One Side or Two = 2

Max. Shearwall plf = 432 plf

Panel Layout

From Module Edge = 6.00 in.

Panel Length = 132.00 in.

From Module Edge = in.

Panel Length = in.

Shearwall plf = 246.5 plf

Shearwall Panel = Gypsum

Gyp. Brand = U.S.G.

Fasteners = Yes

Adhesive = PVA

One Side or Two = 1

Max. Shearwall plf = 247 plf

Panel Layout

From Module Edge = in.

Panel Length = in.

From Module Edge = in.

Panel Length = in.

Shearwall plf = N/A plf

Shearwall Panel =

Gyp. Brand =

Fasteners =

Adhesive =

One Side or Two =

Max. Shearwall plf = plf

Panel Layout

From Module Edge = in.

Panel Length = in.

From Module Edge = in.

Panel Length = in.

Shearwall plf = N/A plf

Shearwall Panel =

Gyp. Brand =

Fasteners =

Adhesive =

One Side or Two =

Max. Shearwall plf = plf

Panel Layout

From Module Edge = in.

Panel Length = in.

From Module Edge = in.

Panel Length = in.

Shearwall plf = N/A plf

Shearwall Panel =

Gyp. Brand =

Fasteners =

Adhesive =

One Side or Two =

Max. Shearwall plf = plf

*Construct per Note 6 on SW01.35.XX

Zone - ID Z1-1

Joist 2

Wall Conn. 8

SC O.C. 14 @ 8"

SF O.C. 16 @ 7"

Beam Lag 2

*Construct per Note 6 on SW01.35.XX

Zone - ID Z1-2

Joist 2

Wall Conn. 8

SC O.C. 38 @ 4"

SF O.C. 44 @ 3.5"

Beam Lag 4

*Construct per Note 6 on SW01.35.XX

Zone - ID Z1-3

Joist 2

Wall Conn. 8

SC O.C. 27 @ 5"

SF O.C. 30 @ 4.5"

Beam Lag 4

*Construct per SW01.25.01

Zone - ID

Joist

Wall Conn.

SC O.C.

SF O.C.

Beam Lag

*Construct per SW01.25.01

Zone - ID

Joist

Wall Conn.

SC O.C.

SF O.C.

Beam Lag

*Construct per SW01.25.01

Zone - ID

Joist

Wall Conn.

SC O.C.

SF O.C.

Beam Lag

*May be 1 joist per Note 9.C. on SW01.00.04

Result = PASS

Result = PASS

Result = PASS

Result =


Result =

Result =

MODIFICATIONS

NOTES:

- 1. PIPE SIZES DETERMINED BY FITTINGS ON EACH SIDE.
- 2. SITE INSTALLED PLUMBING NOTED BY ----- .

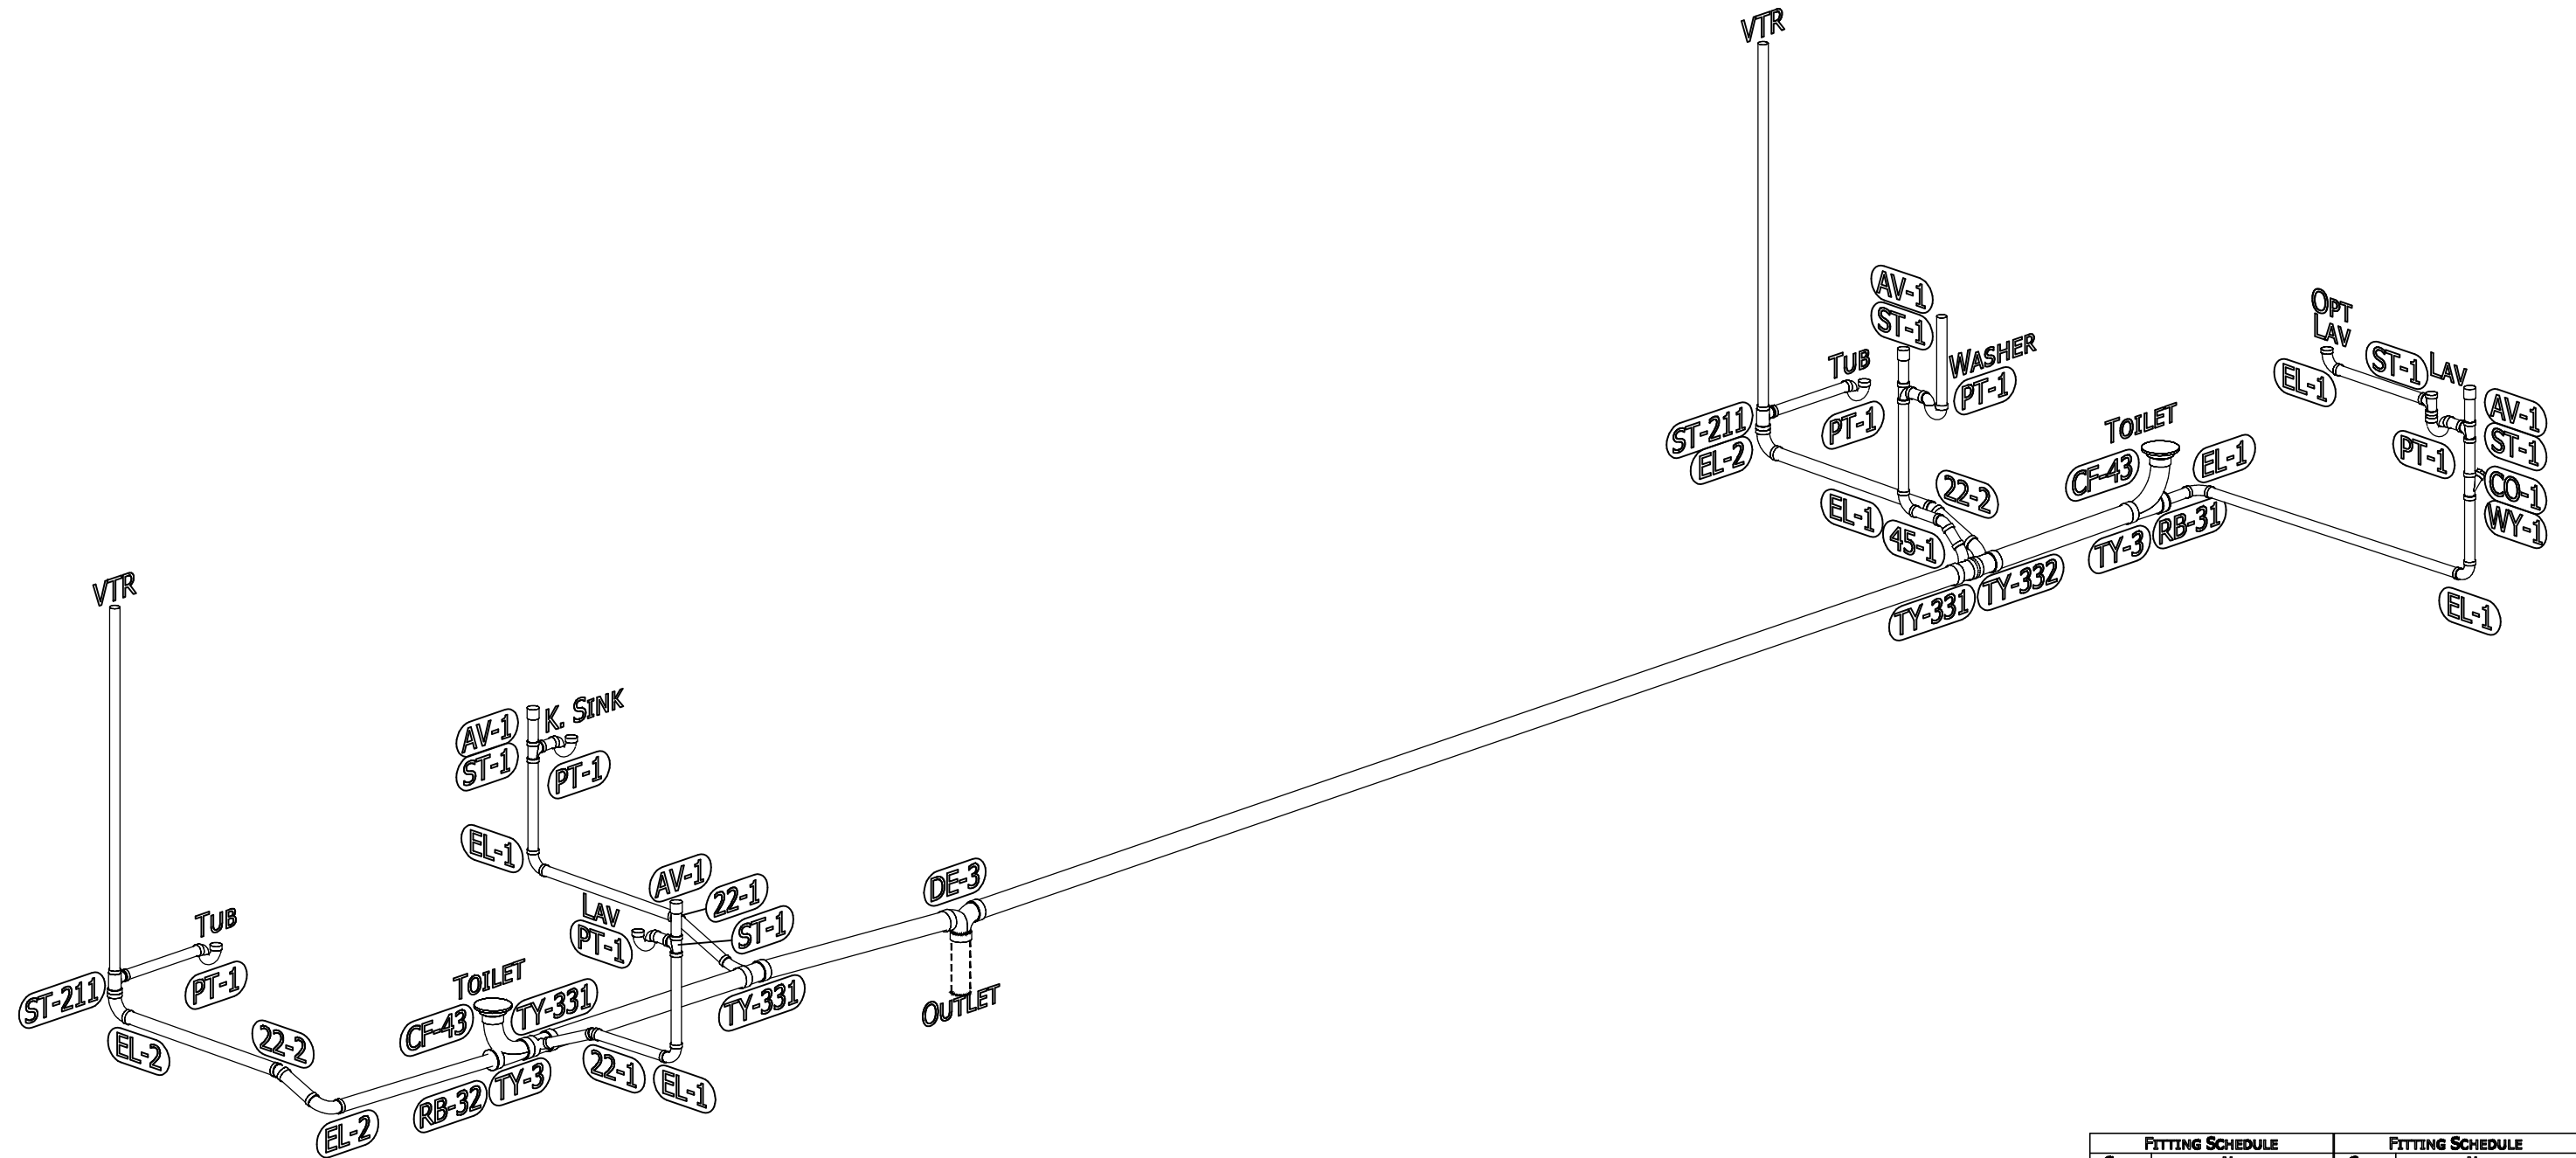

FITTING SCHEDULE		FITTING SCHEDULE	
CALL	NAME	CALL	NAME
22-1	1 1/2" 22 1/2° ELL	PT-1	1 1/2" P-TRAP
22-2	2" 22 1/2° ELL	RB-31	3" x 1 1/2" BUSHING
45-1	1 1/2" 45° ELL	RB-32	3" x 2" BUSHING
AV-1	1 1/2" AUTO VENT	ST-1	1 1/2" TEE
CF-43	4" x 3" CLOSET FLANGE	ST-211	2" x 1 1/2" x 1 1/2" TEE
CO-1	1 1/2" CLEANOUT	TY-3	3" LTYY
DE-3	3" DOUBLE ELL	TY-331	3" x 3" x 1 1/2" LTYY
EL-1	1 1/2" LT 90° ELL	TY-332	3" x 3" x 2" LTYY
EL-2	2" LT 90° ELL	WY-1	1 1/2" WYE

CHAMPION

HOME BUILDERS

755 W. BIG BEAVER ROAD, SUITE 1000 TROY, MI 48064
PHONE: 248-614-8200



MODIFICATIONS

PROJECT:
112APB-2856H32171
56'-0" x 26'-8"
3BD 2BT

DRAWN BY: STAFF

DATE: 04-21-24

SCALE: N.T.S.

TITLE:
DRAIN LINE
PLAN


FILENAME: 112APB-2856H32171

SHEET:
D-101

PROPRIETARY AND CONFIDENTIAL
THESE DRAWINGS AND SPECIFICATIONS ARE ORIGINAL,
PROPRIETARY AND CONFIDENTIAL MATERIALS OF CHAMPION.
COPYRIGHT © 1976-2024 BY CHAMPION

NOTES:

1. PIPE SIZES DETERMINED BY FITTINGS ON EACH SIDE.
2. SITE INSTALLED PLUMBING NOTED BY ----- .

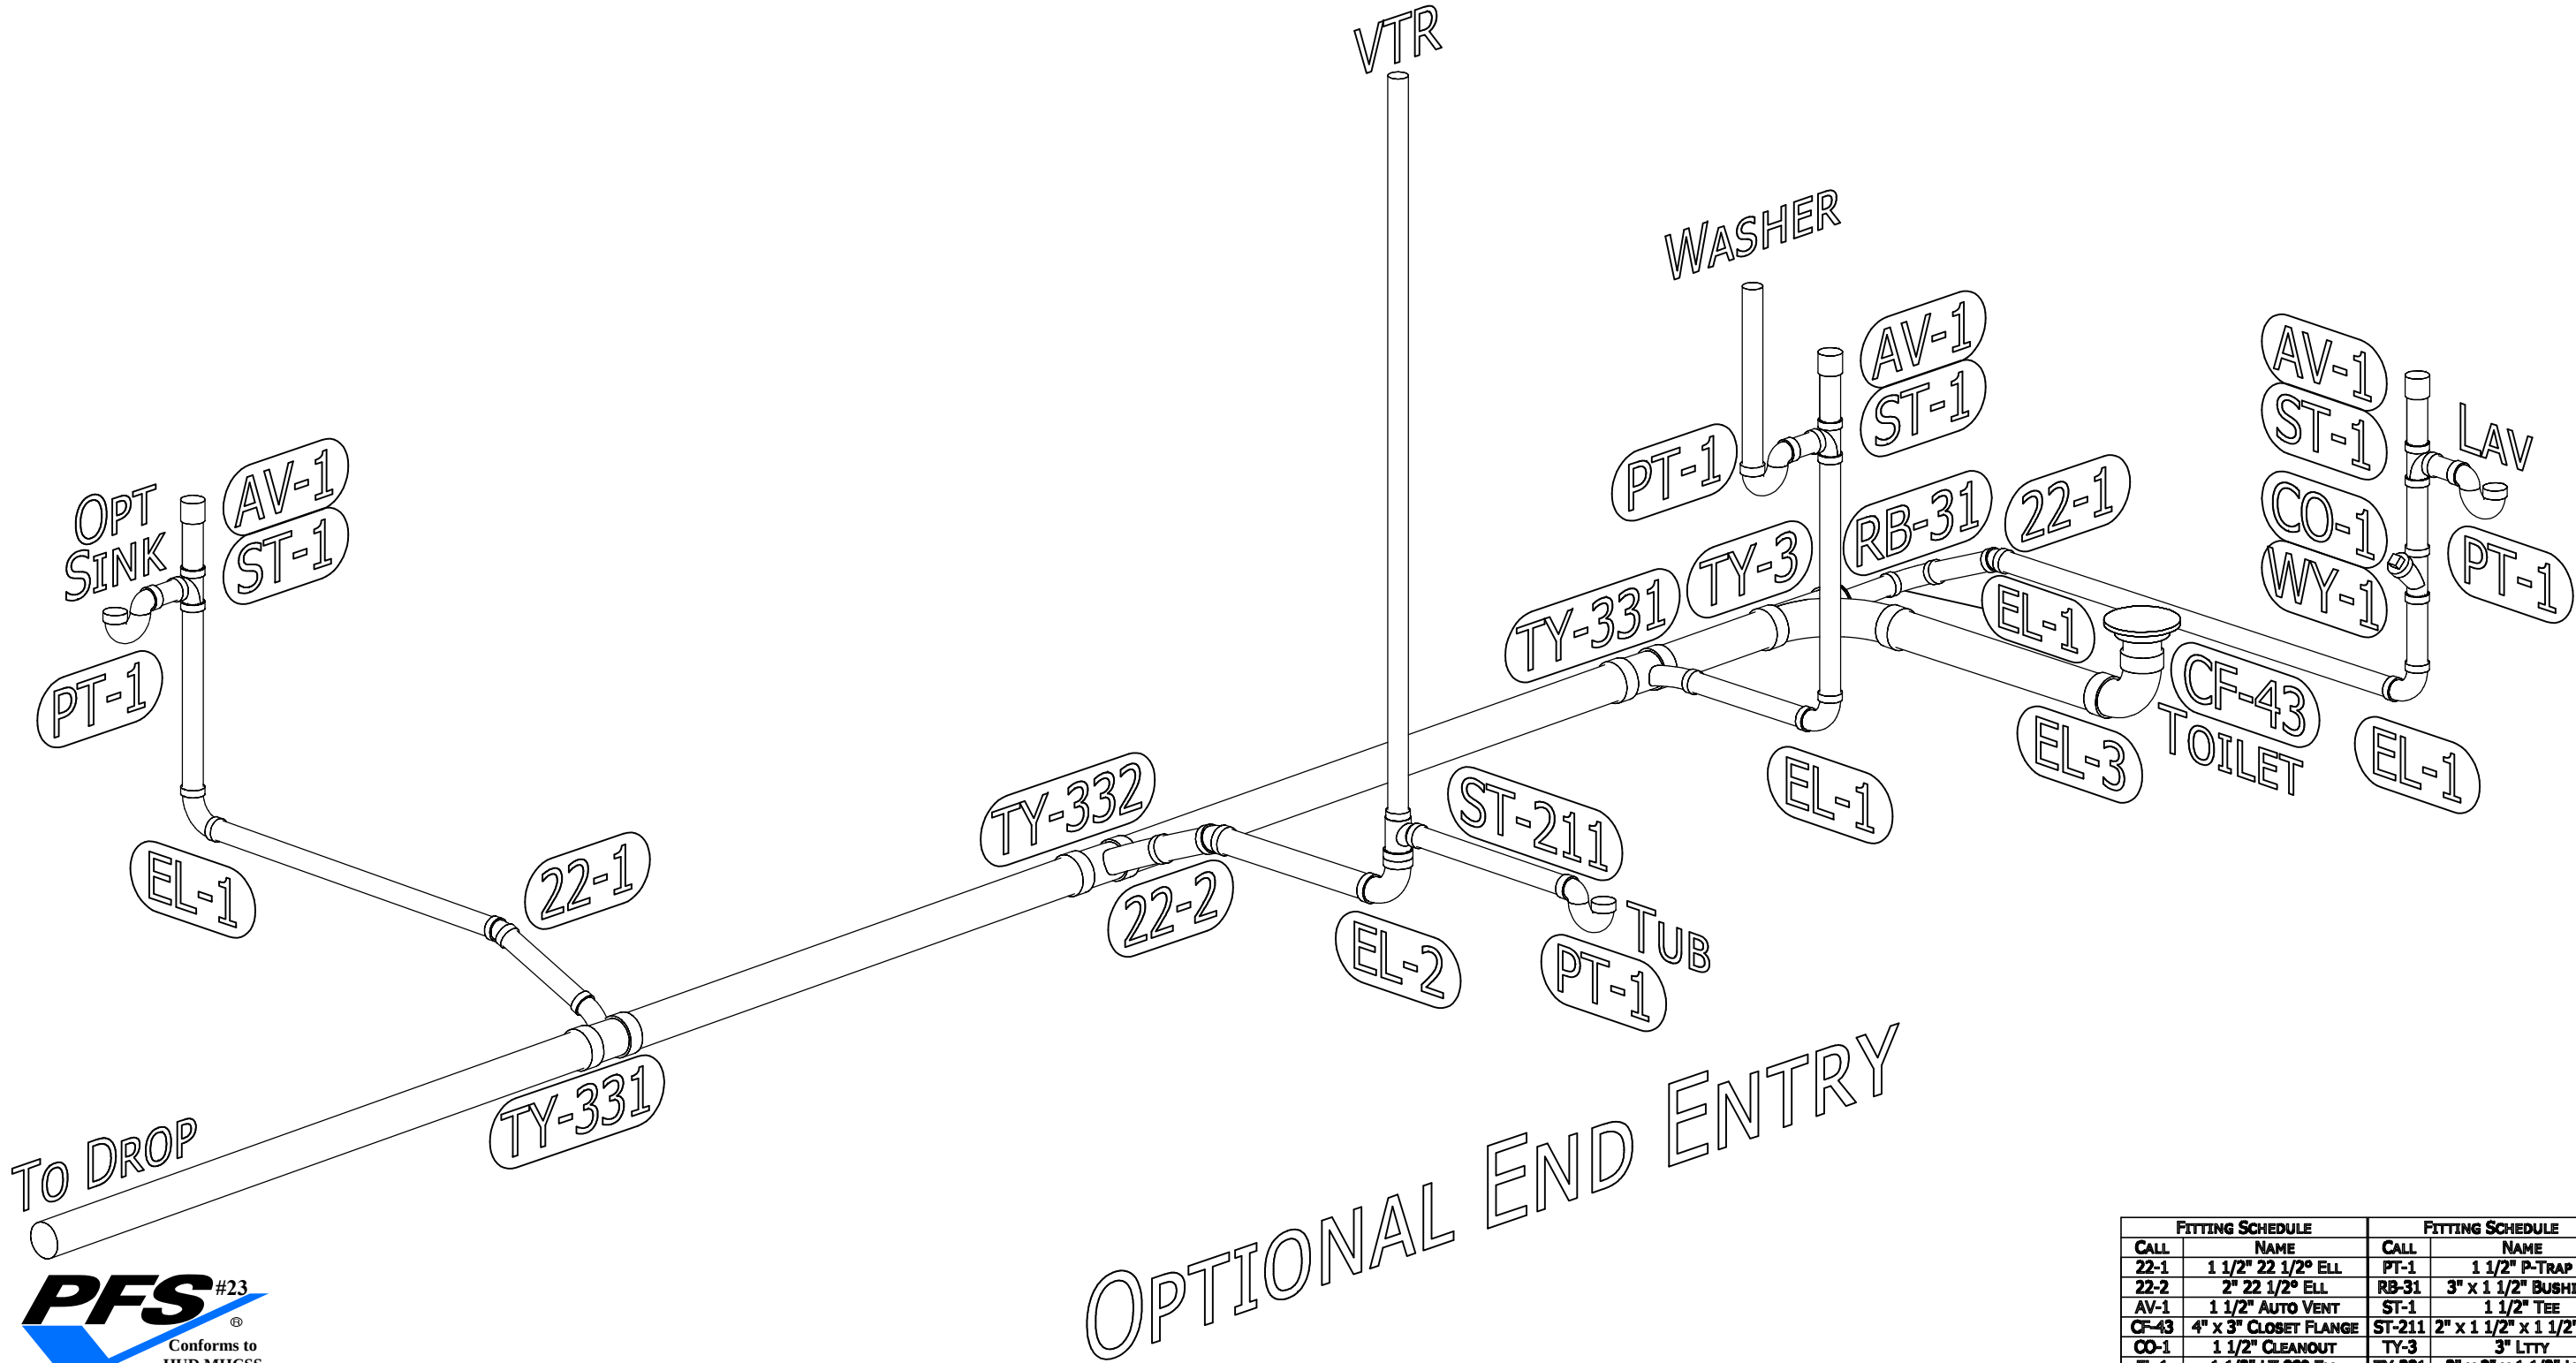

FITTING SCHEDULE		FITTING SCHEDULE	
CALL	NAME	CALL	NAME
22-1	1 1/2" 22 1/2" ELL	PT-1	1 1/2" P-TRAP
22-2	2" 22 1/2" ELL	RB-31	3" x 1 1/2" BUSHING
AV-1	1 1/2" AUTO VENT	ST-1	1 1/2" TEE
CF-43	4" x 3" CLOSET FLANGE	ST-211	2" x 1 1/2" x 1 1/2" TEE
CO-1	1 1/2" CLEANOUT	TY-3	3" LT TY
EL-1	1 1/2" LT 90° ELL	TY-331	3" x 3" x 1 1/2" LT TY
EL-2	2" LT 90° ELL	TY-332	3" x 3" x 2" LT TY
EL-3	3" LT 90° ELL	WY-1	1 1/2" WYE

CHAMPION

HOME BUILDERS

755 W. BIG BEAVER ROAD, SUITE 1000 TROY, MI 48064
PHONE: 248-614-8900



MODIFICATIONS	
1	ADDED OPT. END ENTRY 1/28/25 KG

PROJECT:
112APB-2856H32171
56'-0" x 26'-8"
3BD 2BT

DRAWN BY: STAFF
DATE: 04-21-24
SCALE: N.T.S.

TITLE:
DRAIN LINE
PLAN


FILENAME: 112APB-2856H32171

SHEET:
D-102

PROPRIETARY AND CONFIDENTIAL
THESE DRAWINGS AND SPECIFICATIONS ARE ORIGINAL,
PROPRIETARY AND CONFIDENTIAL MATERIALS OF CHAMPION.
COPYRIGHT © 1976-2025 BY CHAMPION

NOTES:

- 1. ALL PIPE SIZES 1/2" UNLESS OTHERWISE SPECIFIED
- 2. TOTAL BTU = 145,000 (202,000 w/OPTIONS)
- 3. COLUMN LENGTH = 30'-0"

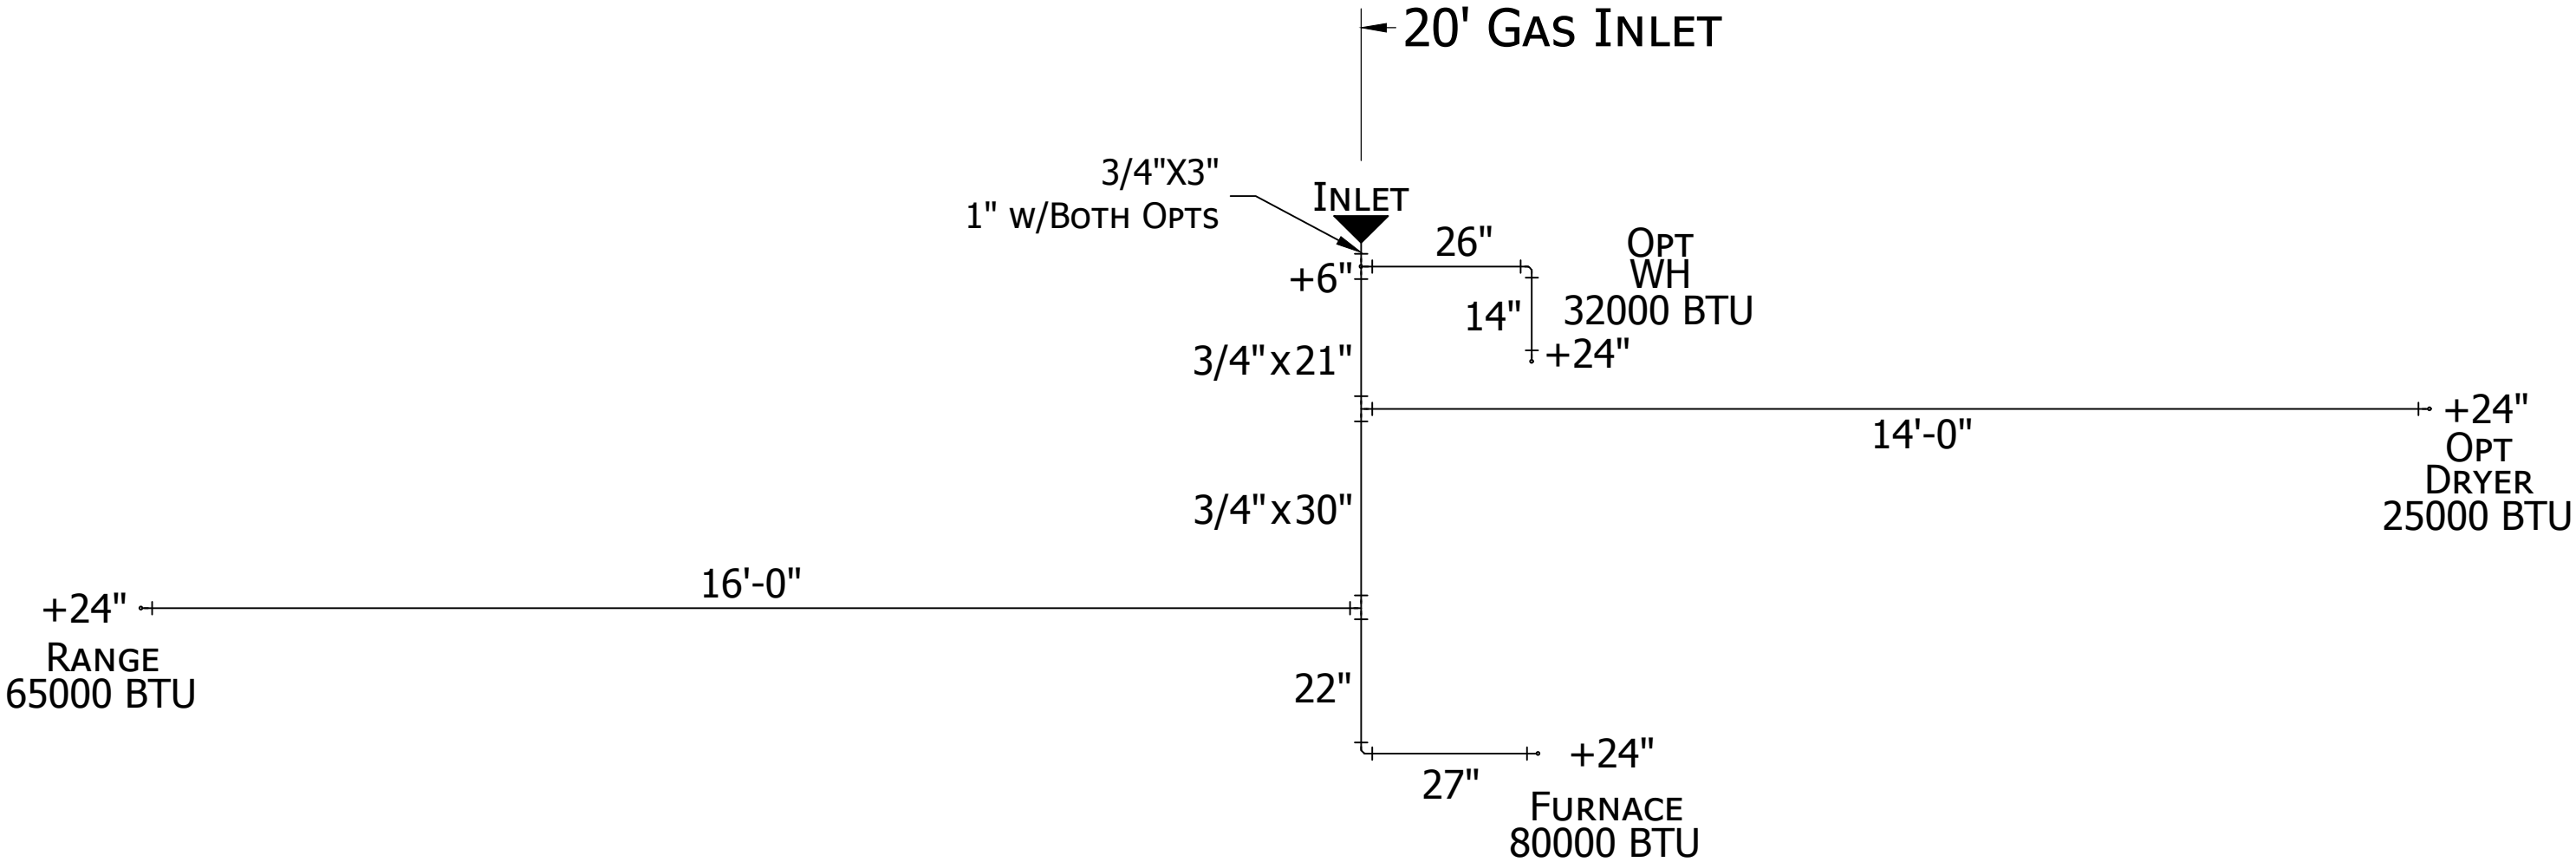

CHAMPION
HOME BUILDERS

755 W. BIG BEAVER ROAD, SUITE 1000 TROY, MI 48064
PHONE: 248-614-8900



MODIFICATIONS

PROJECT:
112APB-2856H32171
56'-0" x 26'-8"
3BD 2BT

DRAWN BY: STAFF
DATE: 04-21-24
SCALE: N.T.S.

TITLE:
GAS LINE
PLAN


FILENAME: 112APB-2856H32171

SHEET:
G-101

PROPRIETARY AND CONFIDENTIAL
THESE DRAWINGS AND SPECIFICATIONS ARE ORIGINAL,
PROPRIETARY AND CONFIDENTIAL MATERIALS OF CHAMPION.
COPYRIGHT © 1976-2024 BY CHAMPION

NOTES:

- 1. ALL PIPE SIZES 1/2" UNLESS OTHERWISE SPECIFIED
- 2. TOTAL BTU = 145,000 (202,000 w/OPTIONS)
- 3. COLUMN LENGTH = 30'-0"

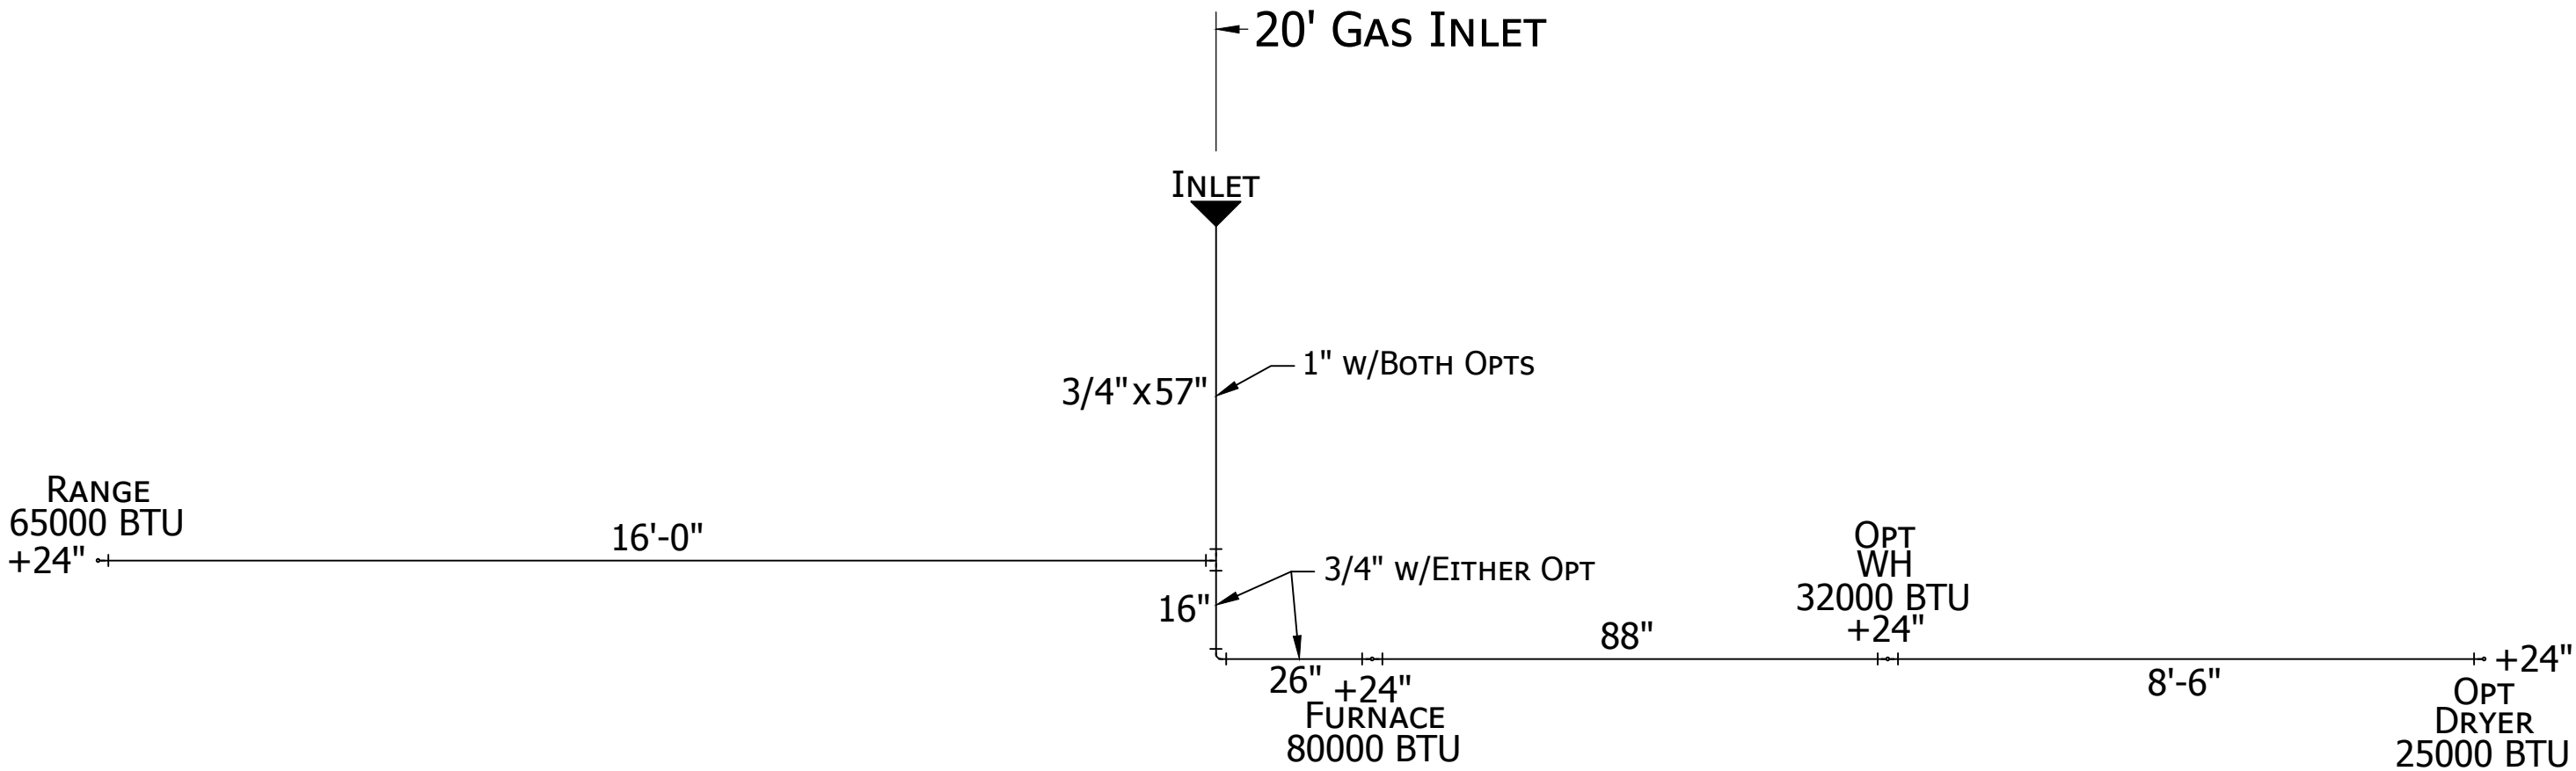

OPTIONAL END ENTRY



CHAMPION

HOME BUILDERS

755 W. BIG BEAVER ROAD, SUITE 1000 TROY, MI 48064
PHONE: 248-614-8200



MODIFICATIONS		
1	ADDED OPT. END ENTRY	1/28/25 KG

PROJECT:
112APB-2856H32171
56'-0" x 26'-8"
3BD 2BT
DRAWN BY: STAFF
DATE: 04-21-24
SCALE: N.T.S.

TITLE:
GAS LINE PLAN
FILENAME: 112APB-2856H32171

SHEET:
G-102
PROPRIETARY AND CONFIDENTIAL THESE DRAWINGS AND SPECIFICATIONS ARE ORIGINAL, PROPRIETARY AND CONFIDENTIAL MATERIALS OF CHAMPION. COPYRIGHT © 1976-2025 BY CHAMPION