


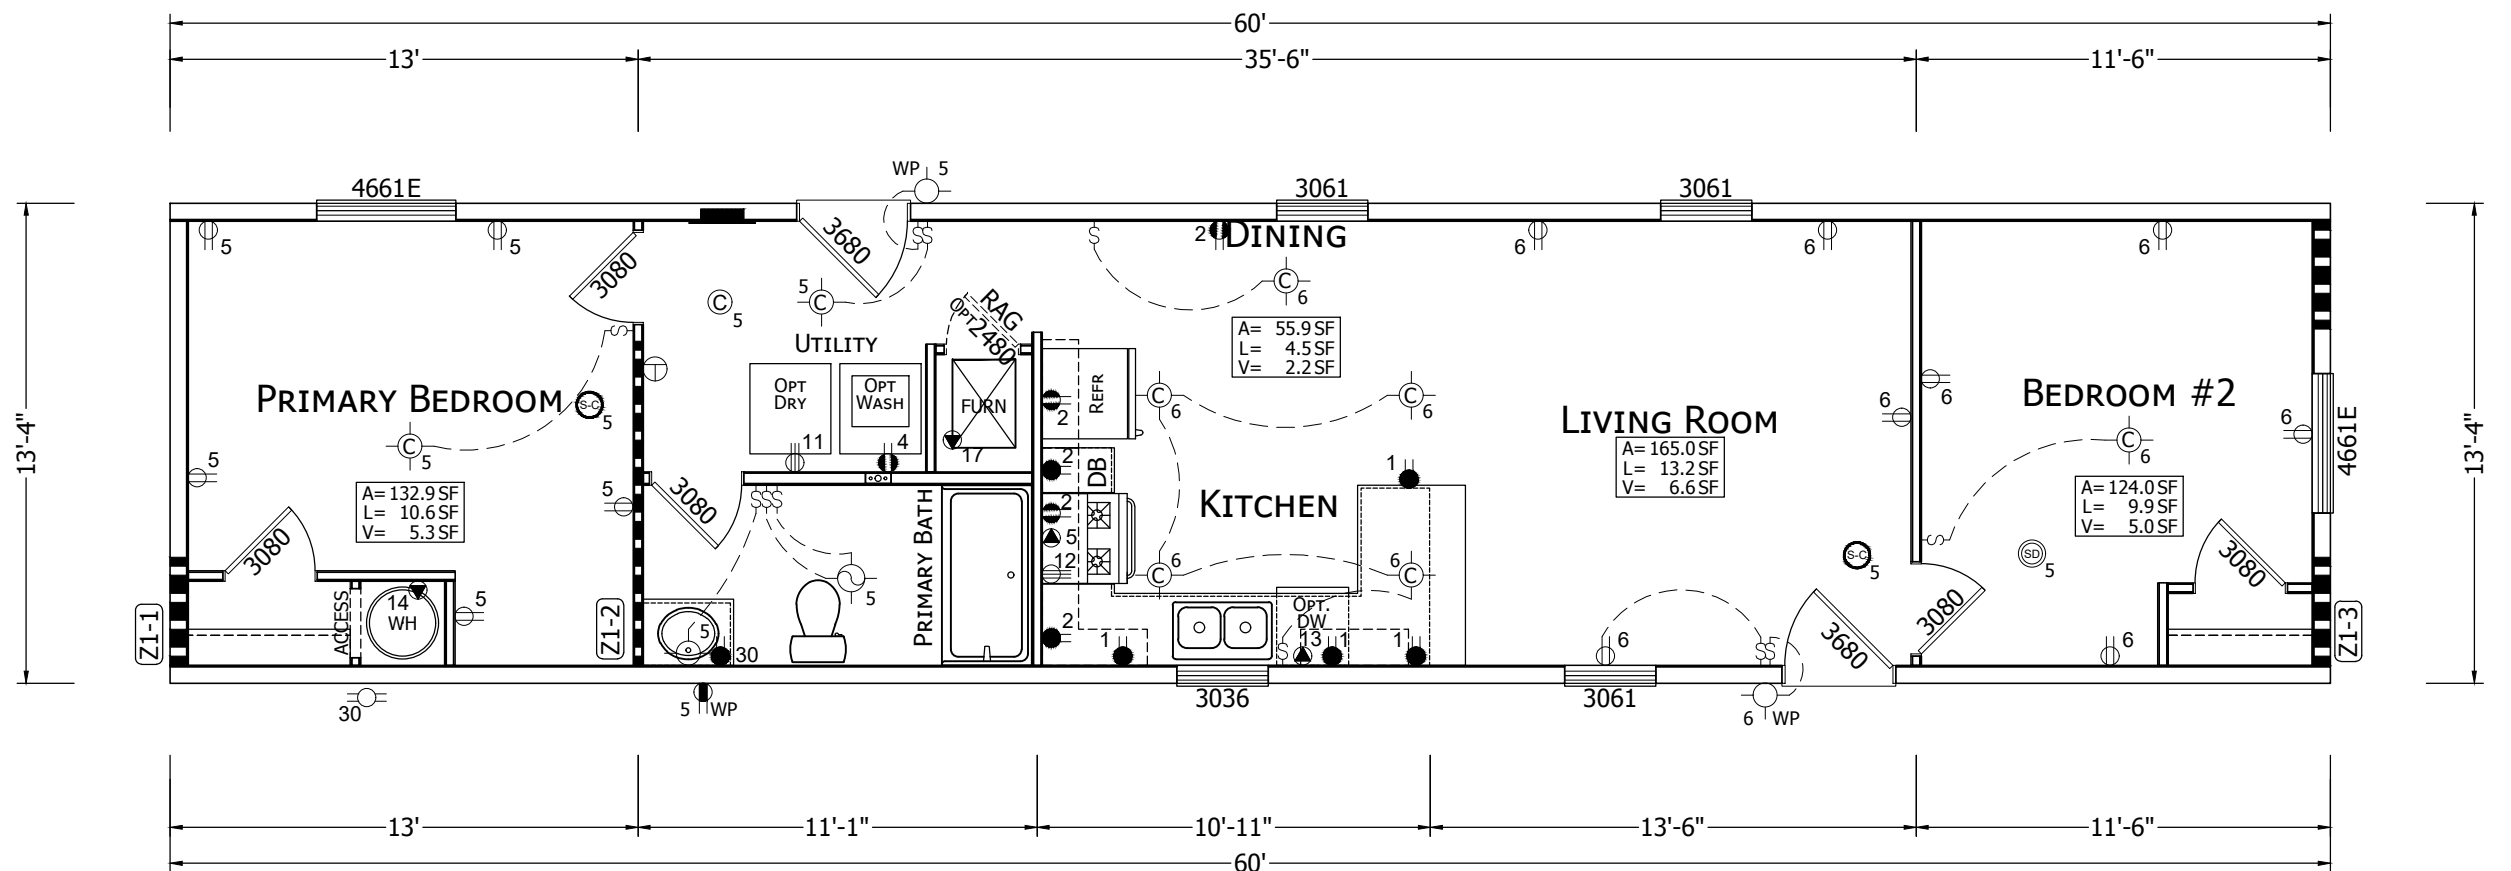

DESIGN CRITERIA
ZONES: WIND 1, ROOF MIDDLE, TEMP III
TOTAL ROUGH WINDOW OPENINGS: 86.5 SF



CHAMPION
HOME BUILDERS

755 W. BIG BEAVER ROAD, SUITE 1000 TROY, MI 48064
PHONE: 248-614-8200



MODIFICATIONS

PROJECT:
112AP-1460H21216
60'-0" x 13'-4"
2BD 1BT


DRAWN BY: KG
DATE: 08-22-23
SCALE: 5/32" = 1'-0"

TITLE:
FLOOR PLAN
ELECTRICAL PLAN

FILENAME: 112AP-1460H21216

SHEET:
AE-101

PROPRIETARY AND CONFIDENTIAL
THESE DRAWINGS AND SPECIFICATIONS ARE ORIGINAL,
PROPRIETARY AND CONFIDENTIAL MATERIALS OF CHAMPION.
COPYRIGHT © 1976-2024 BY CHAMPION

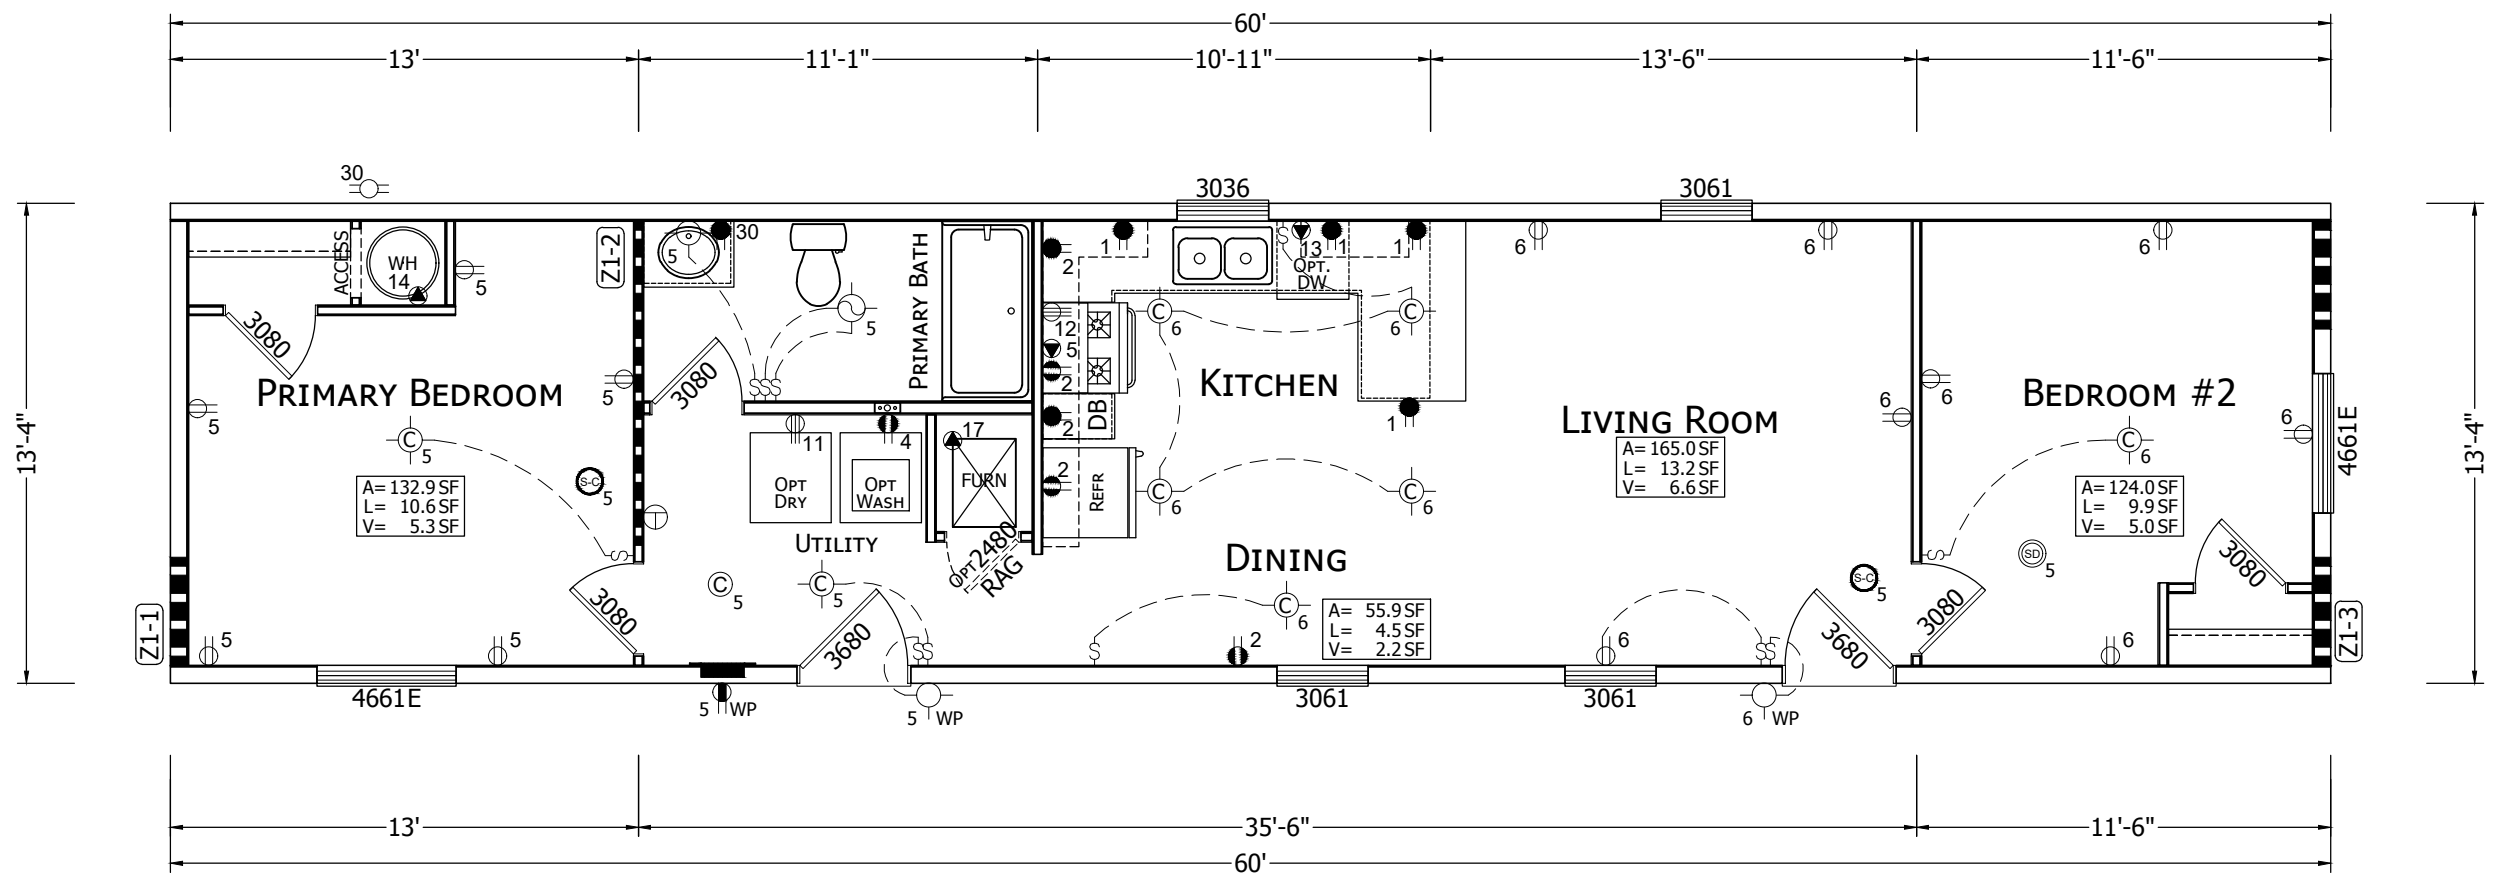

OPT. REVERSE AISLE



CHAMPION
HOME BUILDERS

755 W. BIG BEAVER ROAD, SUITE 1000 TROY, MI 48064
PHONE: 248-614-8200



MODIFICATIONS

PROJECT:
112AP-1460H21216
60'-0" x 13'-4"
2BD 1BT

DRAWN BY: KG
DATE: 08-22-23
SCALE: 5/32" = 1'-0"

TITLE:
**FLOOR PLAN
ELECTRICAL PLAN**


FILENAME: 112AP-1460H21216

SHEET:
AE-102

PROPRIETARY AND CONFIDENTIAL
THESE DRAWINGS AND SPECIFICATIONS ARE ORIGINAL,
PROPRIETARY AND CONFIDENTIAL MATERIALS OF CHAMPION.
COPYRIGHT © 1976-2024 BY CHAMPION

NOTES:

1. PIPE SIZES DETERMINED BY FITTINGS ON EACH SIDE.
2. SITE INSTALLED PLUMBING NOTED BY ----- .

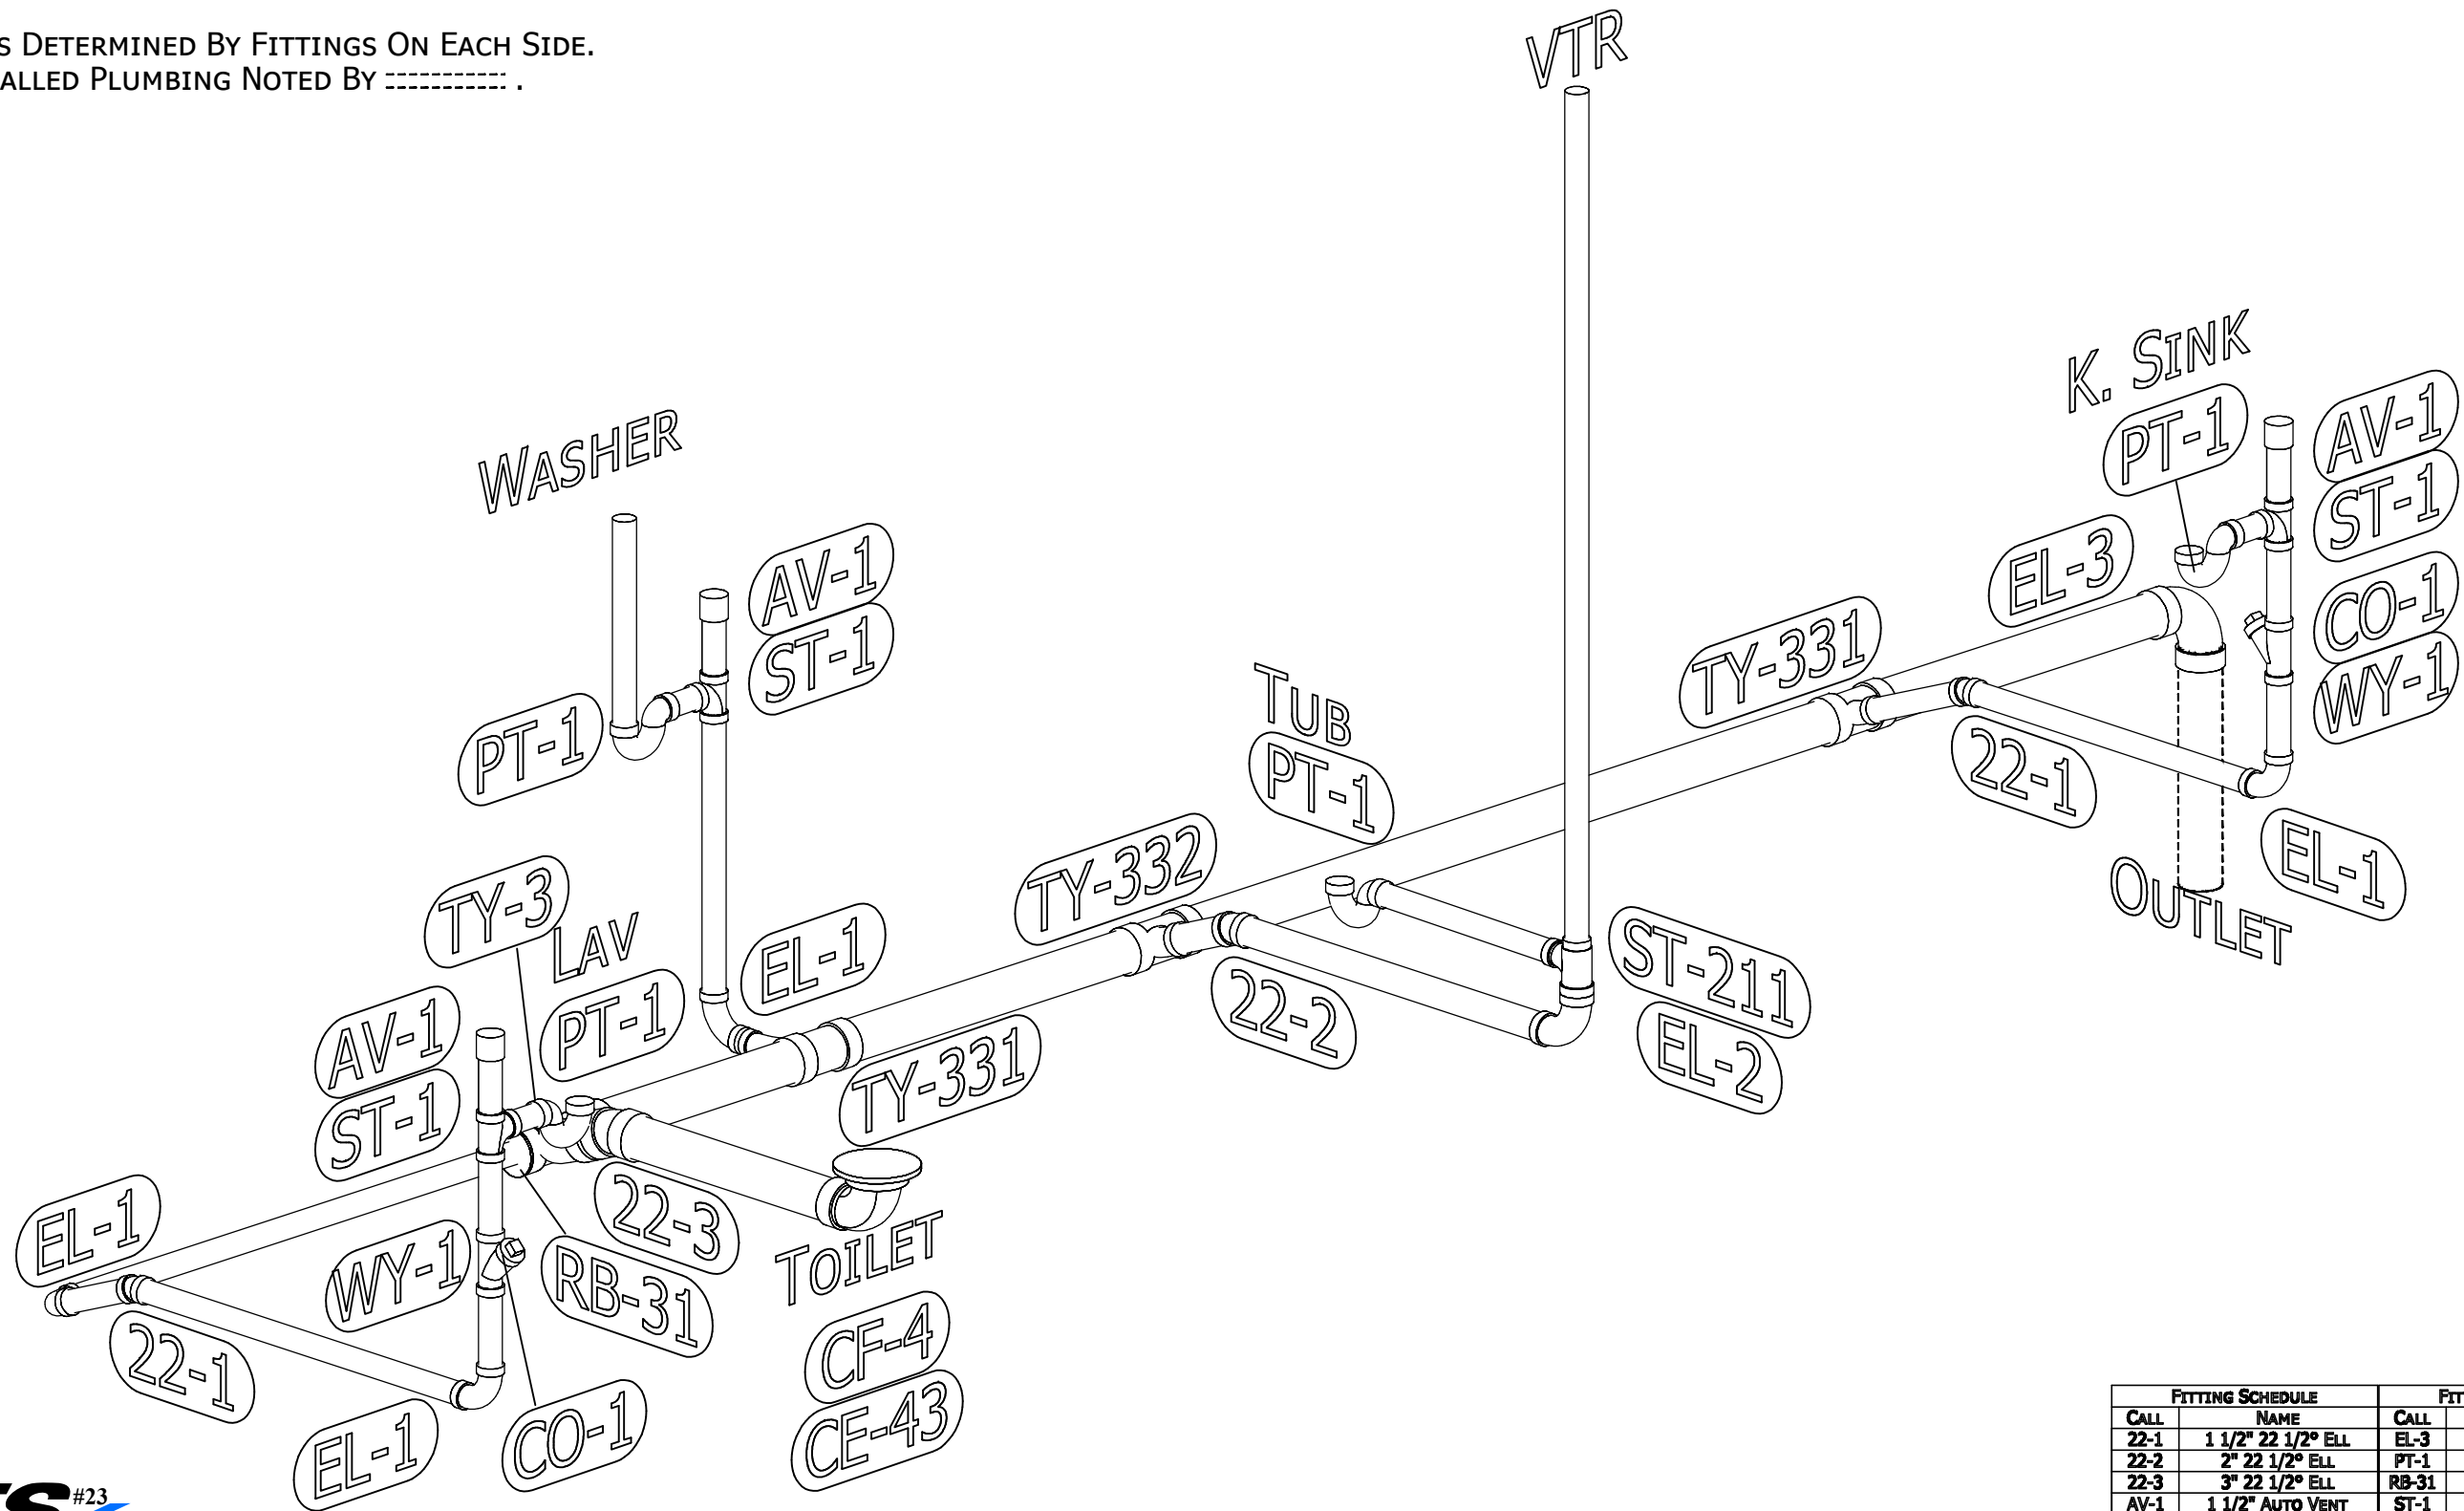

FITTING SCHEDULE		FITTING SCHEDULE	
CALL	NAME	CALL	NAME
22-1	1 1/2" 22 1/2° ELL	EL-3	3" LT 90° ELL
22-2	2" 22 1/2° ELL	PT-1	1 1/2" P-TRAP
22-3	3" 22 1/2° ELL	RB-31	3" x 1 1/2" BUSHING
AV-1	1 1/2" AUTO VENT	ST-1	1 1/2" TEE
CE-43	4" x 3" CLOSET ELL	ST-211	2" x 1 1/2" x 1 1/2" TEE
CF-4	4" CLOSET FLANGE	TY-3	3" LT TY
CO-1	1 1/2" CLEANOUT	TY-331	3" x 3" x 1 1/2" LT TY
EL-1	1 1/2" LT 90° ELL	TY-332	3" x 3" x 2" LT TY
EL-2	2" LT 90° ELL	WY-1	1 1/2" WYE

CHAMPION

HOME BUILDERS

755 W. BIG BEAVER ROAD, SUITE 1000 TROY, MI 48064
PHONE: 248-614-8900



MODIFICATIONS

PROJECT:
112AP-1460H21216
60'-0" x 13'-4"
2BD 1BT

DRAWN BY: KG
DATE: 08-22-23
SCALE: N.T.S.

TITLE:
DRAIN LINE
PLAN


FILENAME: 112AP-1460H21216

SHEET:
D-101

PROPRIETARY AND CONFIDENTIAL
THESE DRAWINGS AND SPECIFICATIONS ARE ORIGINAL,
PROPRIETARY AND CONFIDENTIAL MATERIALS OF CHAMPION.
COPYRIGHT © 1976-2024 BY CHAMPION

NOTES:

1. PIPE SIZES DETERMINED BY FITTINGS ON EACH SIDE.
2. SITE INSTALLED PLUMBING NOTED BY ----- .

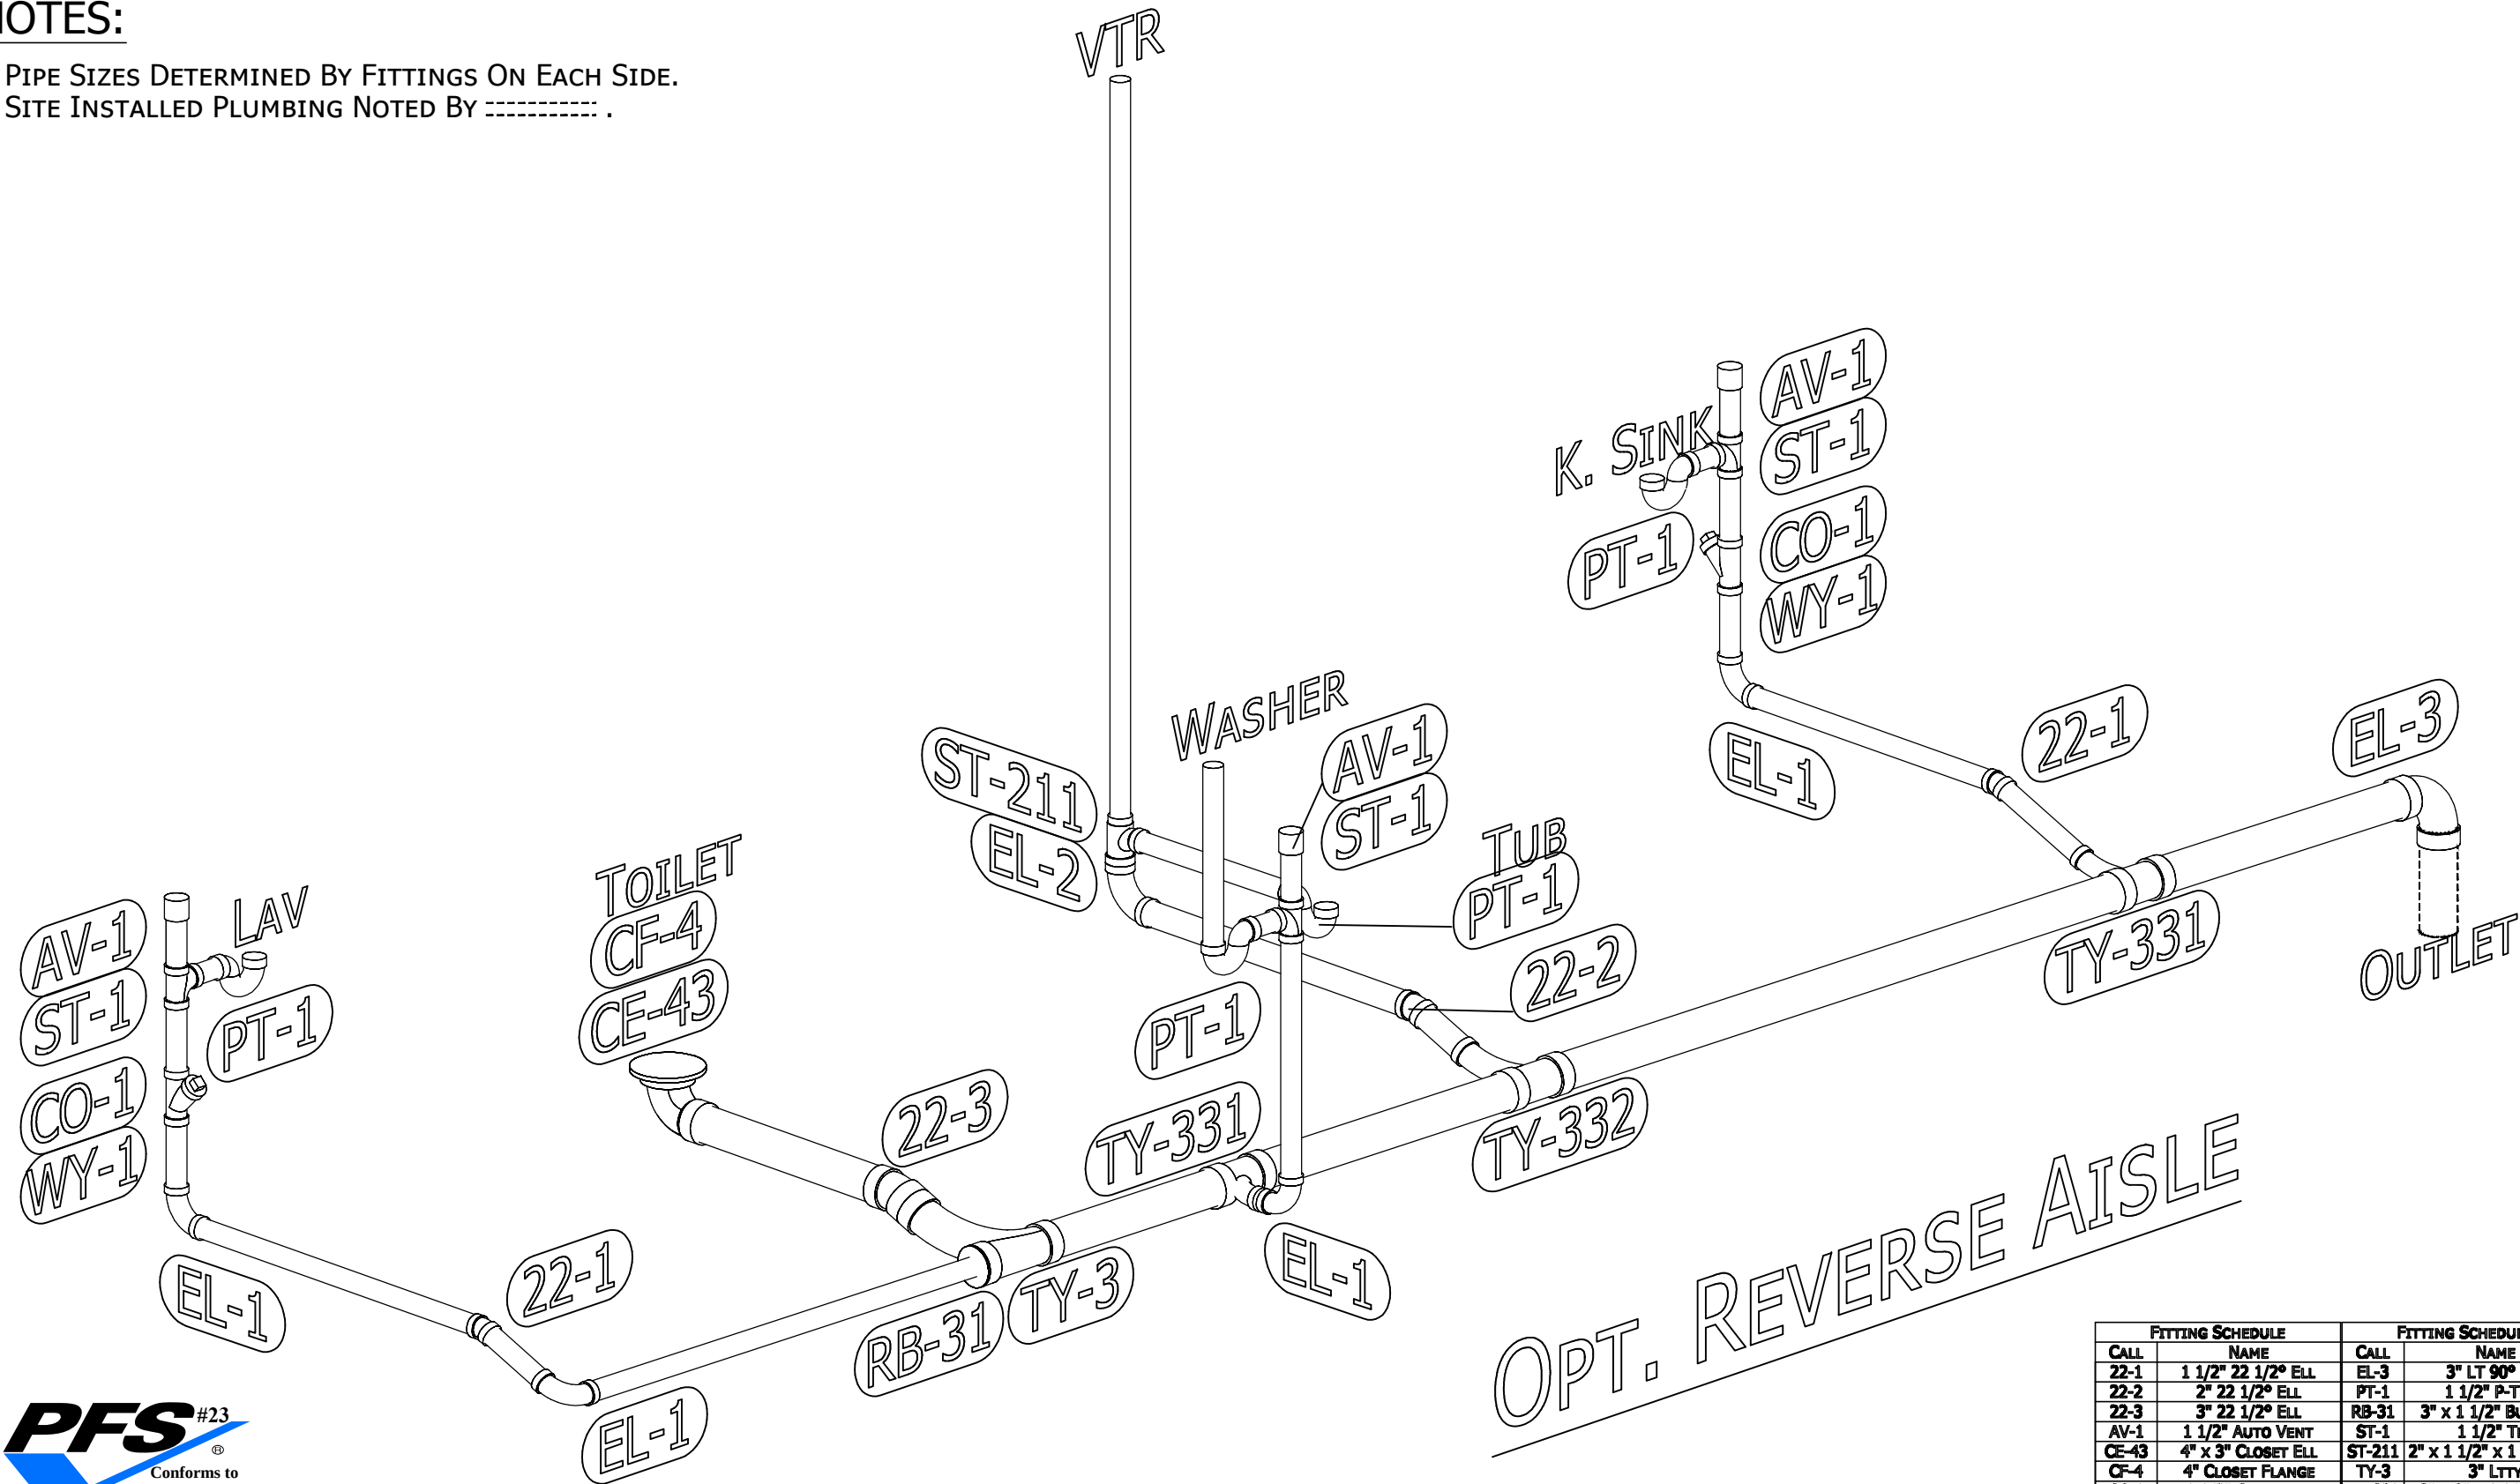

CHAMPION
HOME BUILDERS
755 W. BIG BEAVER ROAD, SUITE 1000 TROY, MI 48064
PHONE: 248-614-8900



MODIFICATIONS

PROJECT:
112AP-1460H21216
60'-0" x 13'-4"
2BD 1BT
DRAWN BY: KG
DATE: 08-22-23
SCALE: N.T.S.


TITLE:
DRAIN LINE
PLAN
FILENAME: 112AP-1460H21216

FITTING SCHEDULE		FITTING SCHEDULE	
CALL	NAME	CALL	NAME
22-1	1 1/2" 22 1/2° ELL	EL-3	3" LT 90° ELL
22-2	2" 22 1/2° ELL	PT-1	1 1/2" P-TRAP
22-3	3" 22 1/2° ELL	RB-31	3" x 1 1/2" BUSHING
AV-1	1 1/2" AUTO VENT	ST-1	1 1/2" TEE
CE-43	4" x 3" CLOSET ELL	ST-211	2" x 1 1/2" x 1 1/2" TEE
CF-4	4" CLOSET FLANGE	TY-3	3" LT TY
CO-1	1 1/2" CLEANOUT	TY-331	3" x 3" x 1 1/2" LT TY
EL-1	1 1/2" LT 90° ELL	TY-332	3" x 3" x 2" LT TY
EL-2	2" LT 90° ELL	WY-1	1 1/2" WYE

SHEET:
D-102
PROPRIETARY AND CONFIDENTIAL
THESE DRAWINGS AND SPECIFICATIONS ARE ORIGINAL,
PROPRIETARY AND CONFIDENTIAL MATERIALS OF CHAMPION.
COPYRIGHT © 1976-2024 BY CHAMPION

NOTES:

- 1. ALL PIPE SIZES 1/2" UNLESS OTHERWISE SPECIFIED
- 2. TOTAL BTU = 145,000(202,000 w/OPTIONS)
- 3. COLUMN LENGTH = 30'-0"

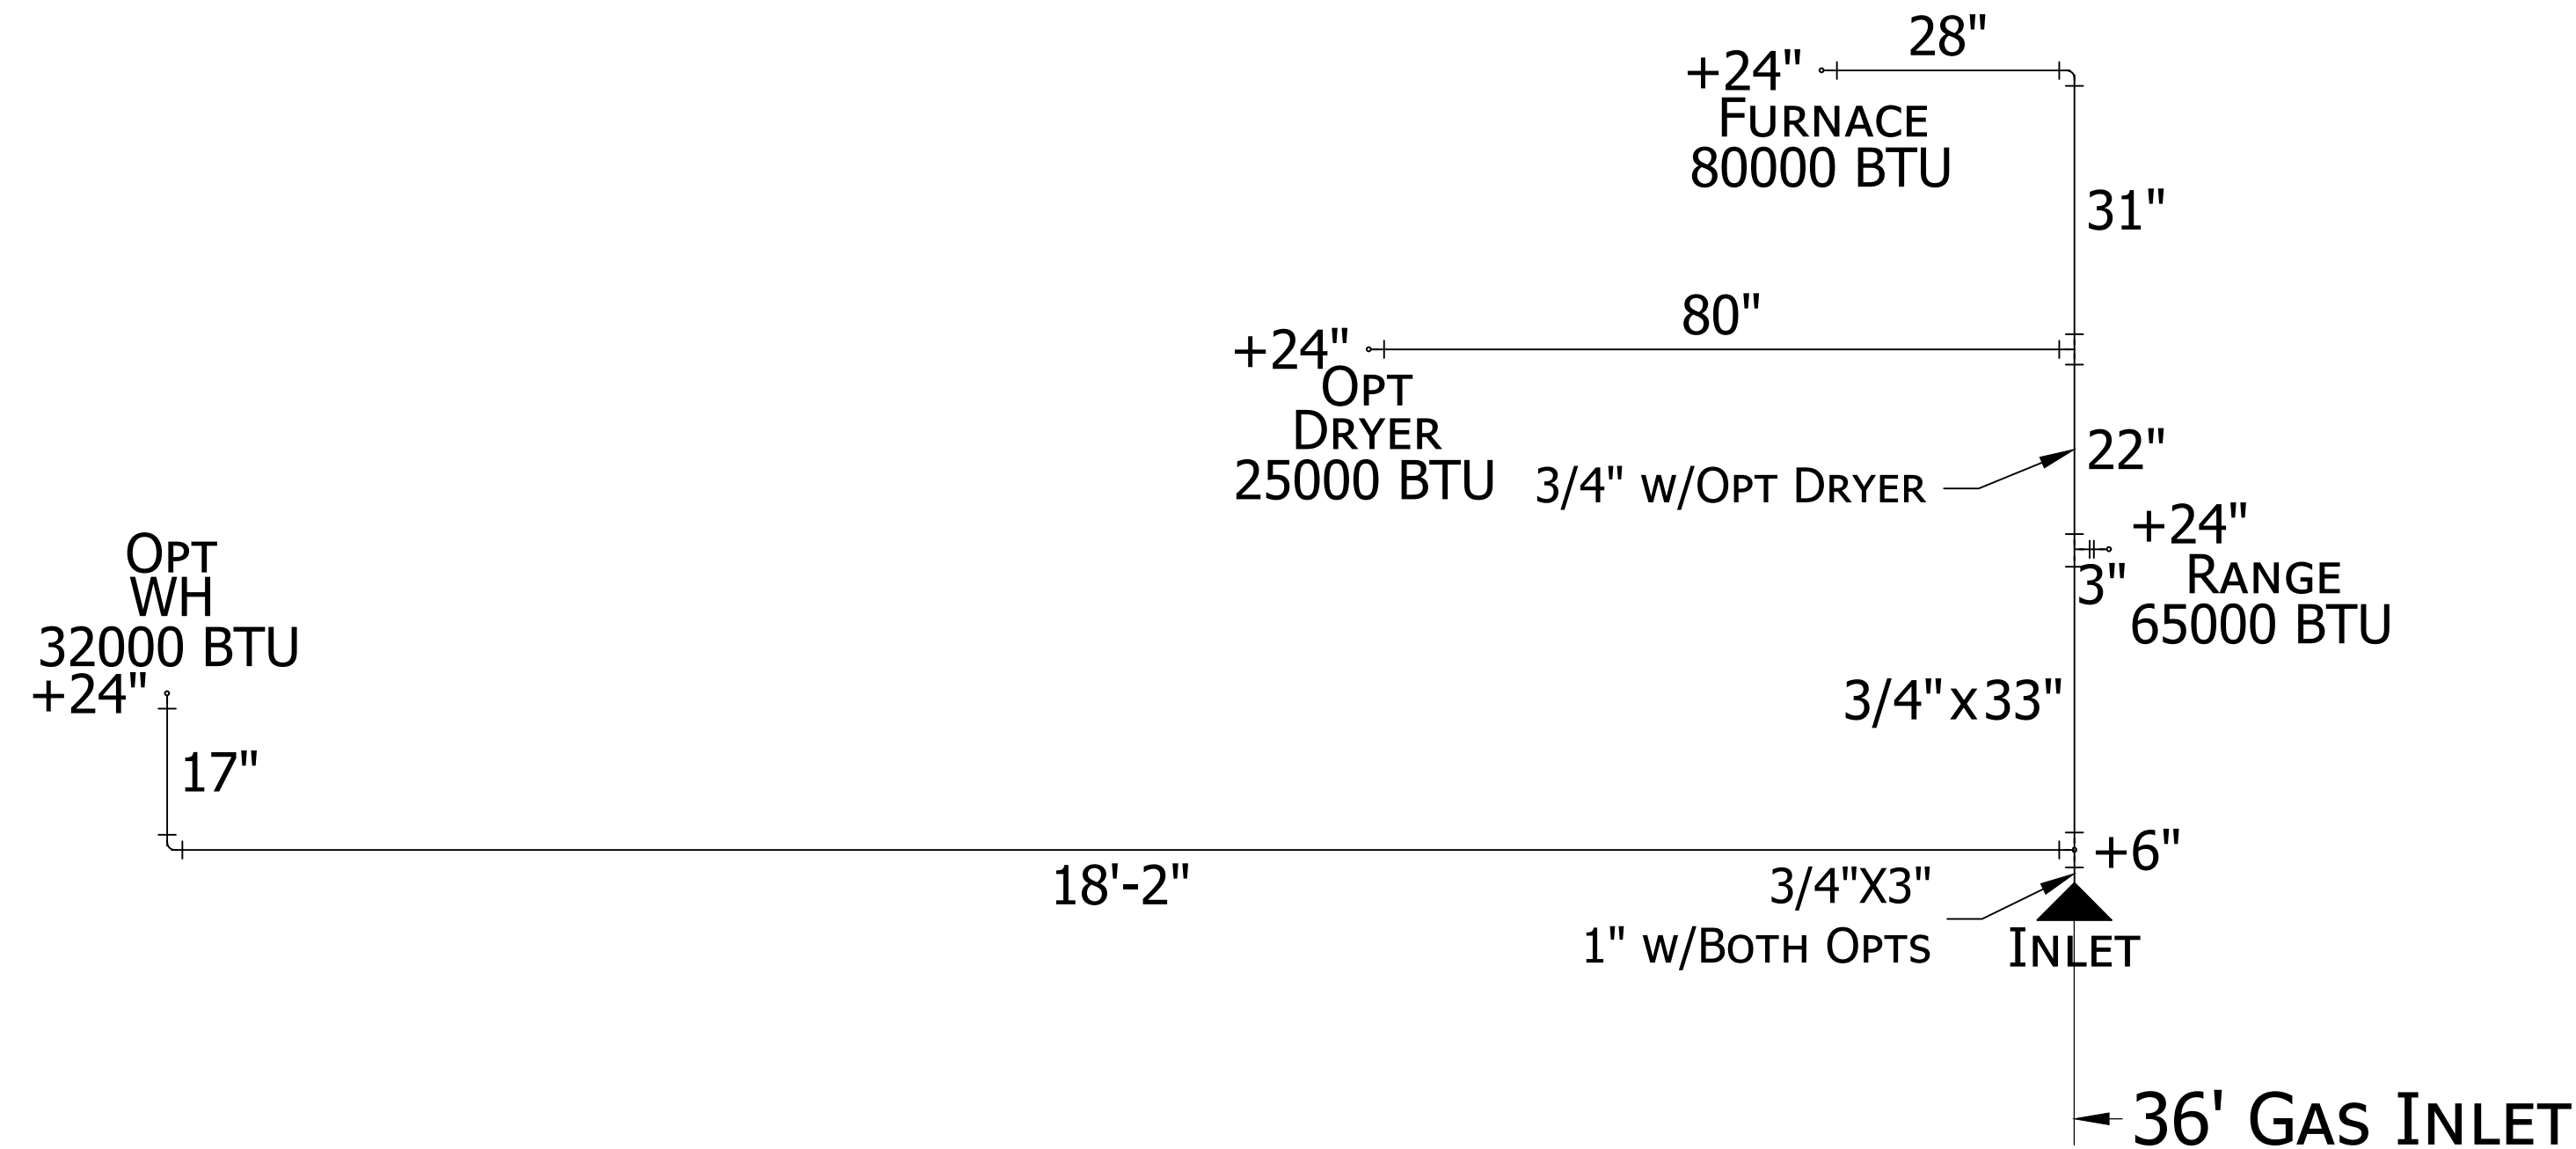

CHAMPION
HOME BUILDERS

755 W. BIG BEAVER ROAD, SUITE 1000 TROY, MI 48064
PHONE: 248-614-8900



MODIFICATIONS

PROJECT:
112AP-1460H21216
60'-0" x 13'-4"
2BD 1BT

DRAWN BY: KG
DATE: 08-22-23
SCALE: N.T.S.

TITLE:
GAS LINE
PLAN

FILENAME: 112AP-1460H21216

SHEET:
G-101

PROPRIETARY AND CONFIDENTIAL
THESE DRAWINGS AND SPECIFICATIONS ARE ORIGINAL,
PROPRIETARY AND CONFIDENTIAL MATERIALS OF CHAMPION.
COPYRIGHT © 1976-2024 BY CHAMPION

NOTES:

- 1. ALL PIPE SIZES 1/2" UNLESS OTHERWISE SPECIFIED
- 2. TOTAL BTU = 192,000
- 3. COLUMN LENGTH = 30'-0"

OPT
WH
32000 BTU
+24" 5"

18'-2"

36' GAS INLET
INLET
3/4"X3"
1" w/BOTH OPTS

+6"

3/4"x33"

+24" RANGE
3" 65000 BTU
22"

3/4" w/OPT DRYER

80"

+24" OPT
DRYER
25000 BTU

31"

+24" 4"
FURNACE
80000 BTU

OPT. REVERSE AISLE



CHAMPION
HOME BUILDERS

755 W. BIG BEAVER ROAD, SUITE 1000 TROY, MI 48064
PHONE: 248-614-8200



MODIFICATIONS

PROJECT:
112AP-1460H21216
60'-0" x 13'-4"
2BD 1BT

DRAWN BY: KG
DATE: 08-22-23
SCALE: N.T.S.

TITLE:
GAS LINE
PLAN

FILENAME: 112AP-1460H21216

SHEET:
G-102

PROPRIETARY AND CONFIDENTIAL
THESE DRAWINGS AND SPECIFICATIONS ARE ORIGINAL,
PROPRIETARY AND CONFIDENTIAL MATERIALS OF CHAMPION.
COPYRIGHT © 1976-2024 BY CHAMPION