




CHAMPION
HOME BUILDERS

755 W. BIG BEAVER ROAD, SUITE 1000 TROY, MI 48064
PHONE: 248-614-8200

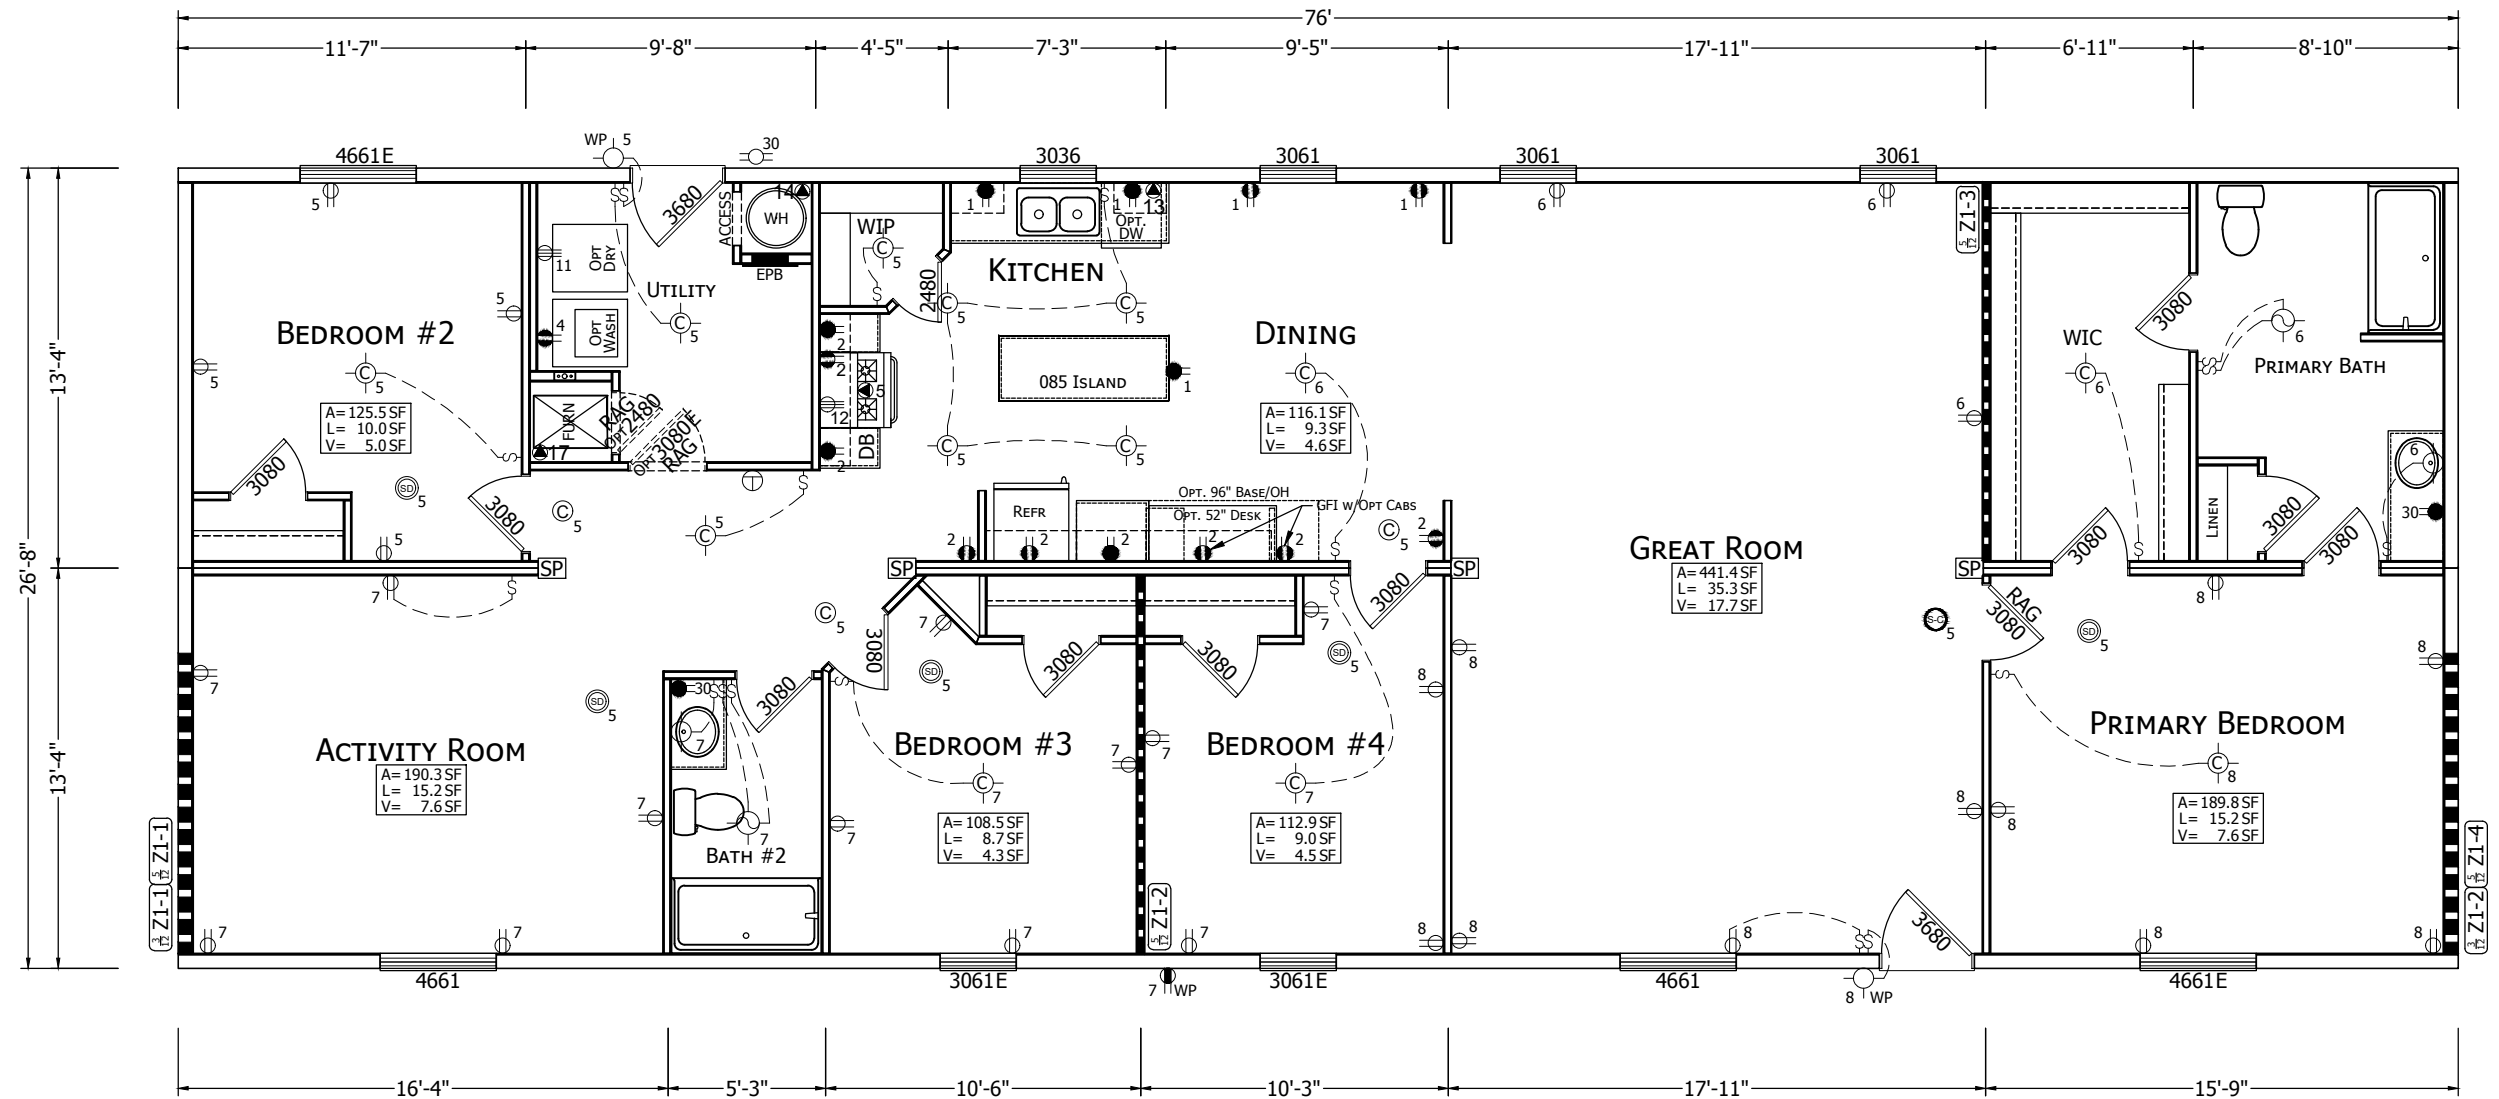

MODIFICATIONS

PROJECT:
112APB-2876H42180
76'-0" x 26'-8"
4BD 2BT


DRAWN BY: KG
DATE: 10-24-23
SCALE: 5/32" = 1'-0"

TITLE:
FLOOR PLAN
ELECTRICAL PLAN


FILENAME: 112APB-2876H42180

SHEET:
AE-101


PROPRIETARY AND CONFIDENTIAL
THESE DRAWINGS AND SPECIFICATIONS ARE ORIGINAL,
PROPRIETARY AND CONFIDENTIAL MATERIALS OF CHAMPION.
COPYRIGHT © 1976-2024 BY CHAMPION

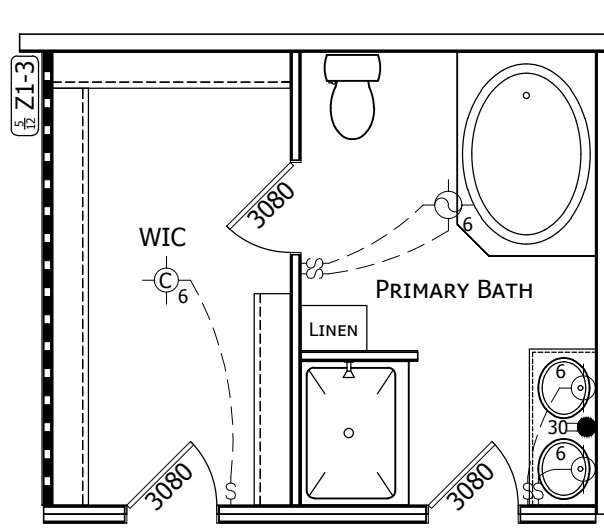


OPTIONAL PRIMARY BATH

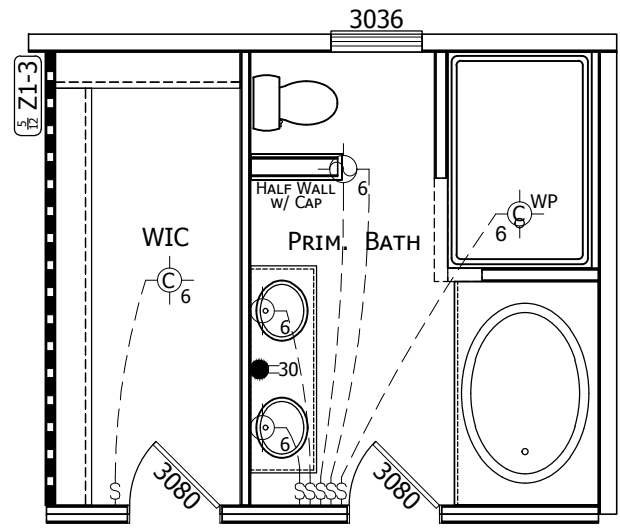



OPTIONAL SERENITY BATH

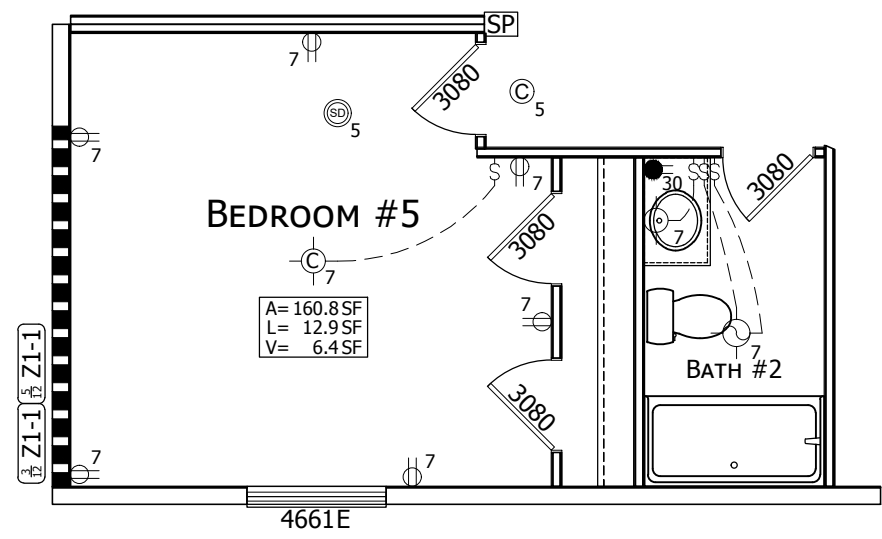

OPTIONAL 5TH BEDROOM

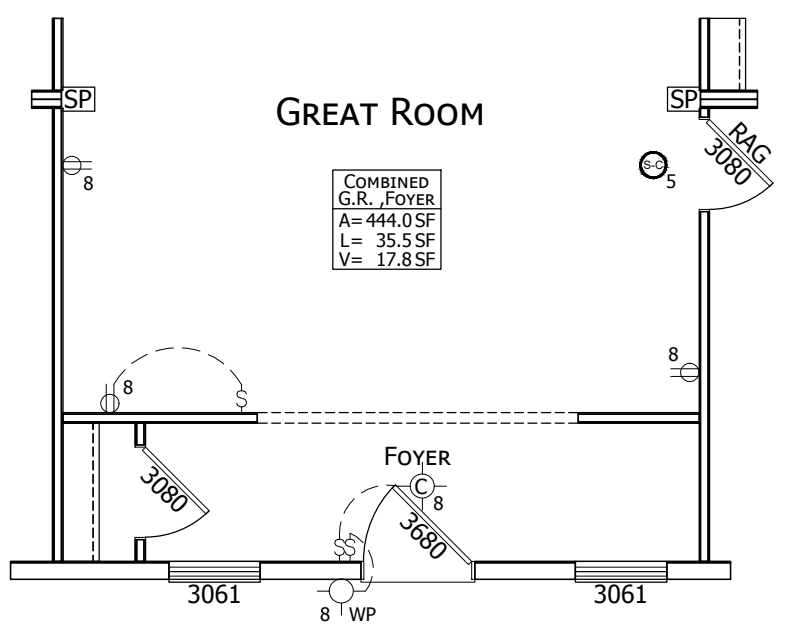

OPTIONAL FOYER

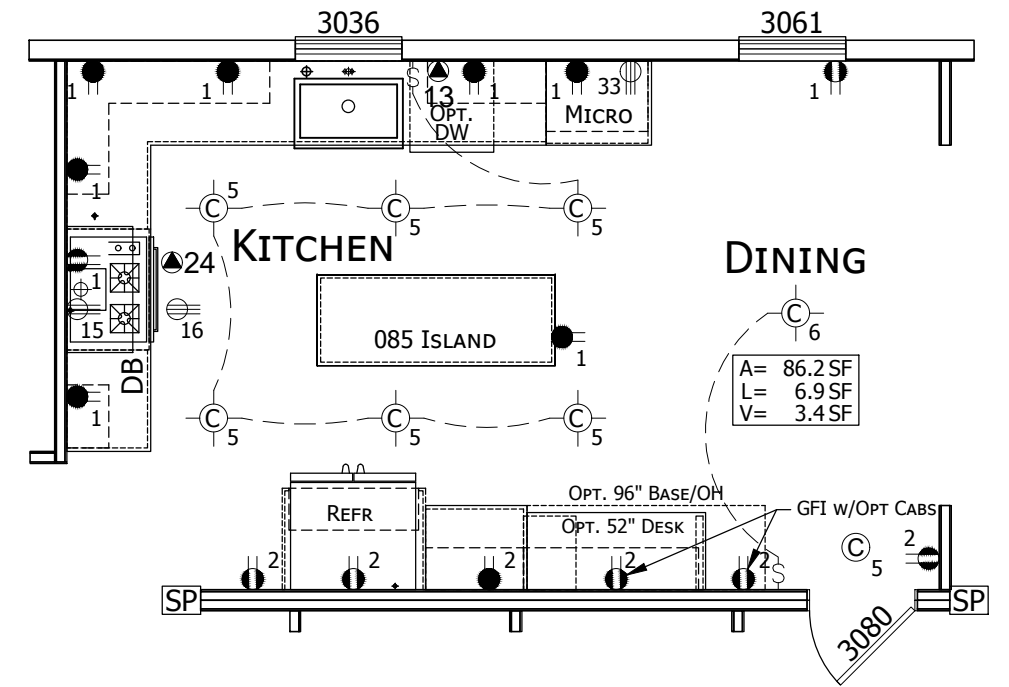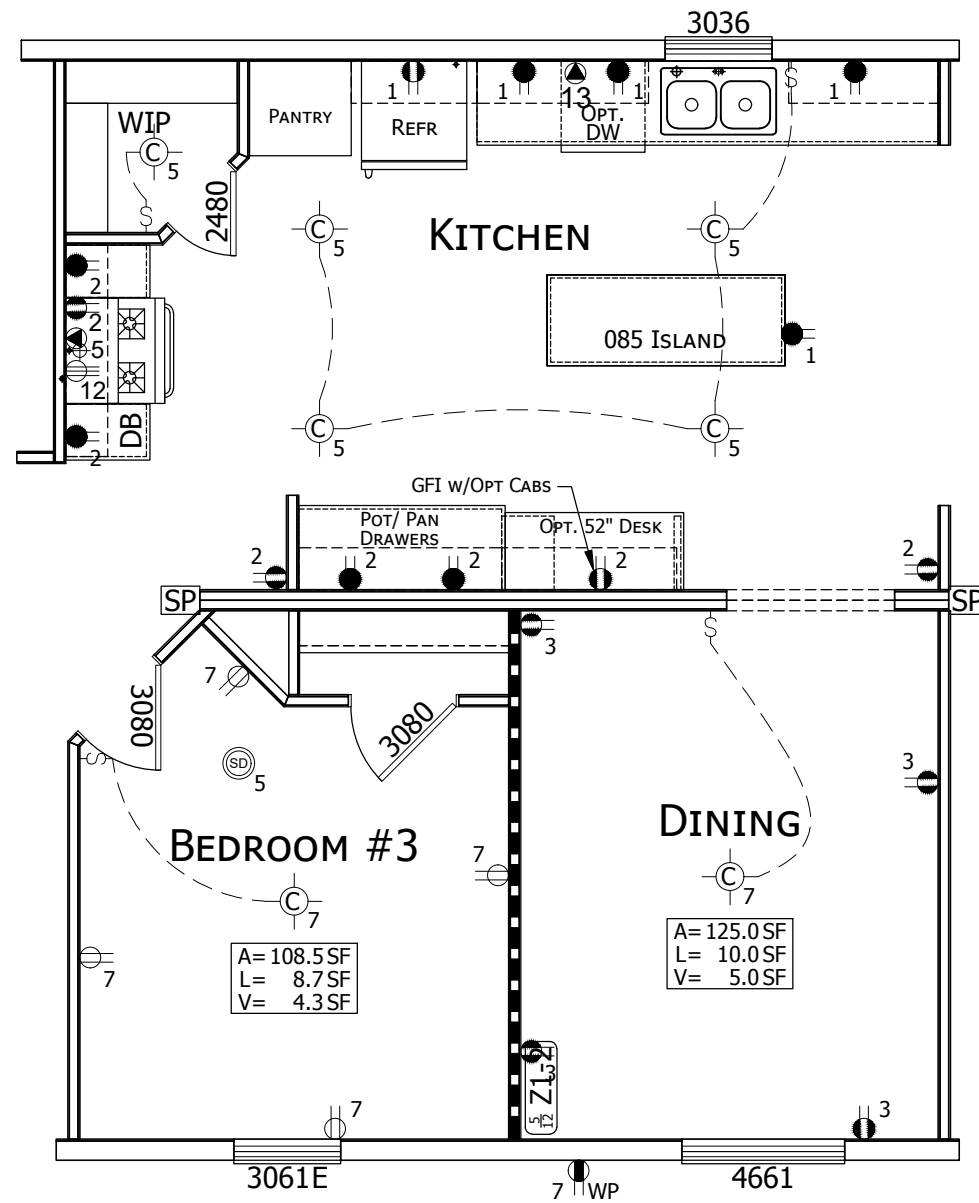

OPTIONAL ULTIMATE KITCHEN 2

CHAMPION
HOME BUILDERS

755 W. BIG BEAVER ROAD, SUITE 1000 TROY, MI 48064
PHONE: 248-614-8200



MODIFICATIONS

PROJECT:
112APB-2876H42180
76'-0" x 26'-8"
4BD 2BT

DRAWN BY: KG
DATE: 10-24-23
SCALE: 5/32" = 1'-0"

TITLE:
FLOOR PLAN
ELECTRICAL PLAN
OPTIONS

FILENAME: 112APB-2876H42180


SHEET:
AE-103

PROPRIETARY AND CONFIDENTIAL
THESE DRAWINGS AND SPECIFICATIONS ARE ORIGINAL,
PROPRIETARY AND CONFIDENTIAL MATERIALS OF CHAMPION.
COPYRIGHT © 1976-2024 BY CHAMPION

Overall Check =		PASS	CHB Shear Wall - Layout / Design				Model#:	112APB-2876H42180																					
Wind Zone =		I	Diaphragm Construction:		Fasteners		Wall Construction:																						
Wind Load =		15	psf	Diaphragm Type =		Wood Roof	15GAx1.75																						
Module Width =		160	in	Minimum Width =			in	Bottom Plate Thickness =		2x																			
Number of Boxes =		2		Max plf =		176.3	plf	Top Plate Thickness =		2x																			
Wall Height =		96	in	Max. End Wall Reaction =		4,701	lbs	Wall to Floor Joist =		#10	x 3.5"																		
Roof Pitch =		4.36	:12	Max. Interior Reaction =		9,403	lbs	Wall to Ceiling Framing =		#10	x 3.5"																		
Angle =		20.0	°	Max. Span =		112.00	ft.	Wall to Wall Fastener =		#10	x 3.50"																		
Roof Overhang =		8	in																										
Floor Joist Spacing =		16	in o.c.	Floor Construction:																									
Rim Joist Plies =		1																											
Frame Spacing =		99.5	in	Floor Joist Size =		2x6																							
Beam Depth =		12	in	Floor Joist Species =		SPF																							
Open Porch =		0.00	ft.	Floor Joist Grade =		#3																							
Home Length =		76.00	ft.	Decking Glued to Joists =		Yes																							
																				* For monoslope homes only									
Vertical Trib =		4.00	ft	Vertical Trib =		4.00	ft	Vertical Trib =		4.00	ft	Vertical Trib =		4.00	ft	Vertical Trib =		4.00	ft										
King Post Height *=			in.	King Post Height *=			in.	King Post Height *=			in.	King Post Height *=			in.	King Post Height *=			in.										
Porch End Wall =		--		Porch End Wall =		--		Porch End Wall =		--		Porch End Wall =		--		Porch End Wall =		--											
Left End Wall Shear Wall				Shear Wall 2				Shear Wall 3				Shear Wall 4				Shear Wall 5				Shear Wall 6									
Dist. To Next SW =		76.00	ft.	Dist. To Next SW =			ft.	Dist. To Next SW =			ft.	Dist. To Next SW =			ft.	Dist. To Next SW =			ft.										
Manual Input =		--		Manual Input =		--		Manual Input =		--		Manual Input =		--		Manual Input =		--											
Load to Shearwall =		2280.0	lbs	Load to Shearwall =		2280.0	lbs	Load to Shearwall =		0.0	lbs	Load to Shearwall =		0.0	lbs	Load to Shearwall =		0.0	lbs										
Panel Layout				Panel Layout				Panel Layout				Panel Layout				Panel Layout				Panel Layout									
From Module Edge =		6.00	in.	From Module Edge =		6.00	in.	From Module Edge =			in.	From Module Edge =			in.	From Module Edge =			in.										
Panel Length =		120.00	in.	Panel Length =		120.00	in.	Panel Length =			in.	Panel Length =			in.	Panel Length =			in.										
From Module Edge =			in.	From Module Edge =			in.	From Module Edge =			in.	From Module Edge =			in.	From Module Edge =			in.										
Panel Length =			in.	Panel Length =			in.	Panel Length =			in.	Panel Length =			in.	Panel Length =			in.										
Shearwall plf =		228.0	plf	Shearwall plf =		228.0	plf	Shearwall plf =		N/A	plf	Shearwall plf =		N/A	plf	Shearwall plf =		N/A	plf										
Shearwall Panel =		Gypsum		Shearwall Panel =		Gypsum		Shearwall Panel =				Shearwall Panel =				Shearwall Panel =													
Gyp. Brand =		U.S.G.		Gyp. Brand =		U.S.G.		Gyp. Brand =				Gyp. Brand =				Gyp. Brand =													
Fasteners =		Yes		Fasteners =		Yes		Fasteners =				Fasteners =				Fasteners =													
Adhesive =		PVA		Adhesive =		PVA		Adhesive =				Adhesive =				Adhesive =													
One Side or Two =		1		One Side or Two =		1		One Side or Two =				One Side or Two =				One Side or Two =													
Max. Shearwall plf =		247	plf	Max. Shearwall plf =		247	plf	Max. Shearwall plf =			plf	Max. Shearwall plf =			plf	Max. Shearwall plf =			plf										
*Construct per Note 6 on SW01.35.XX				*Construct per Note 6 on SW01.35.XX				*Construct per SW01.25.01				*Construct per SW01.25.01				*Construct per SW01.25.01				*Construct per SW01.25.01									
Zone - ID		Z1-1		Zone - ID		Z1-2		Zone - ID				Zone - ID				Zone - ID													
Joist		2		Joist		2		Joist				Joist				Joist													
Wall Conn.		8		Wall Conn.		8		Wall Conn.				Wall Conn.				Wall Conn.													
SC O.C.		22 @ 5.5"		SC O.C.		22 @ 5.5"		SC O.C.				SC O.C.				SC O.C.													
SF O.C.		27 @ 4.5"		SF O.C.		27 @ 4.5"		SF O.C.				SF O.C.				SF O.C.													
Beam Lag		3		Beam Lag		3		Beam Lag				Beam Lag				Beam Lag													
*May be 1 joist per Note 9.C. on SW01.00.04				*May be 1 joist per Note 9.C on SW01.00.04																									
Result =		PASS		Result =		PASS		Result =				Result =				Result =													

NOTES:

- 1. PIPE SIZES DETERMINED BY FITTINGS ON EACH SIDE.
- 2. SITE INSTALLED PLUMBING NOTED BY ----- .

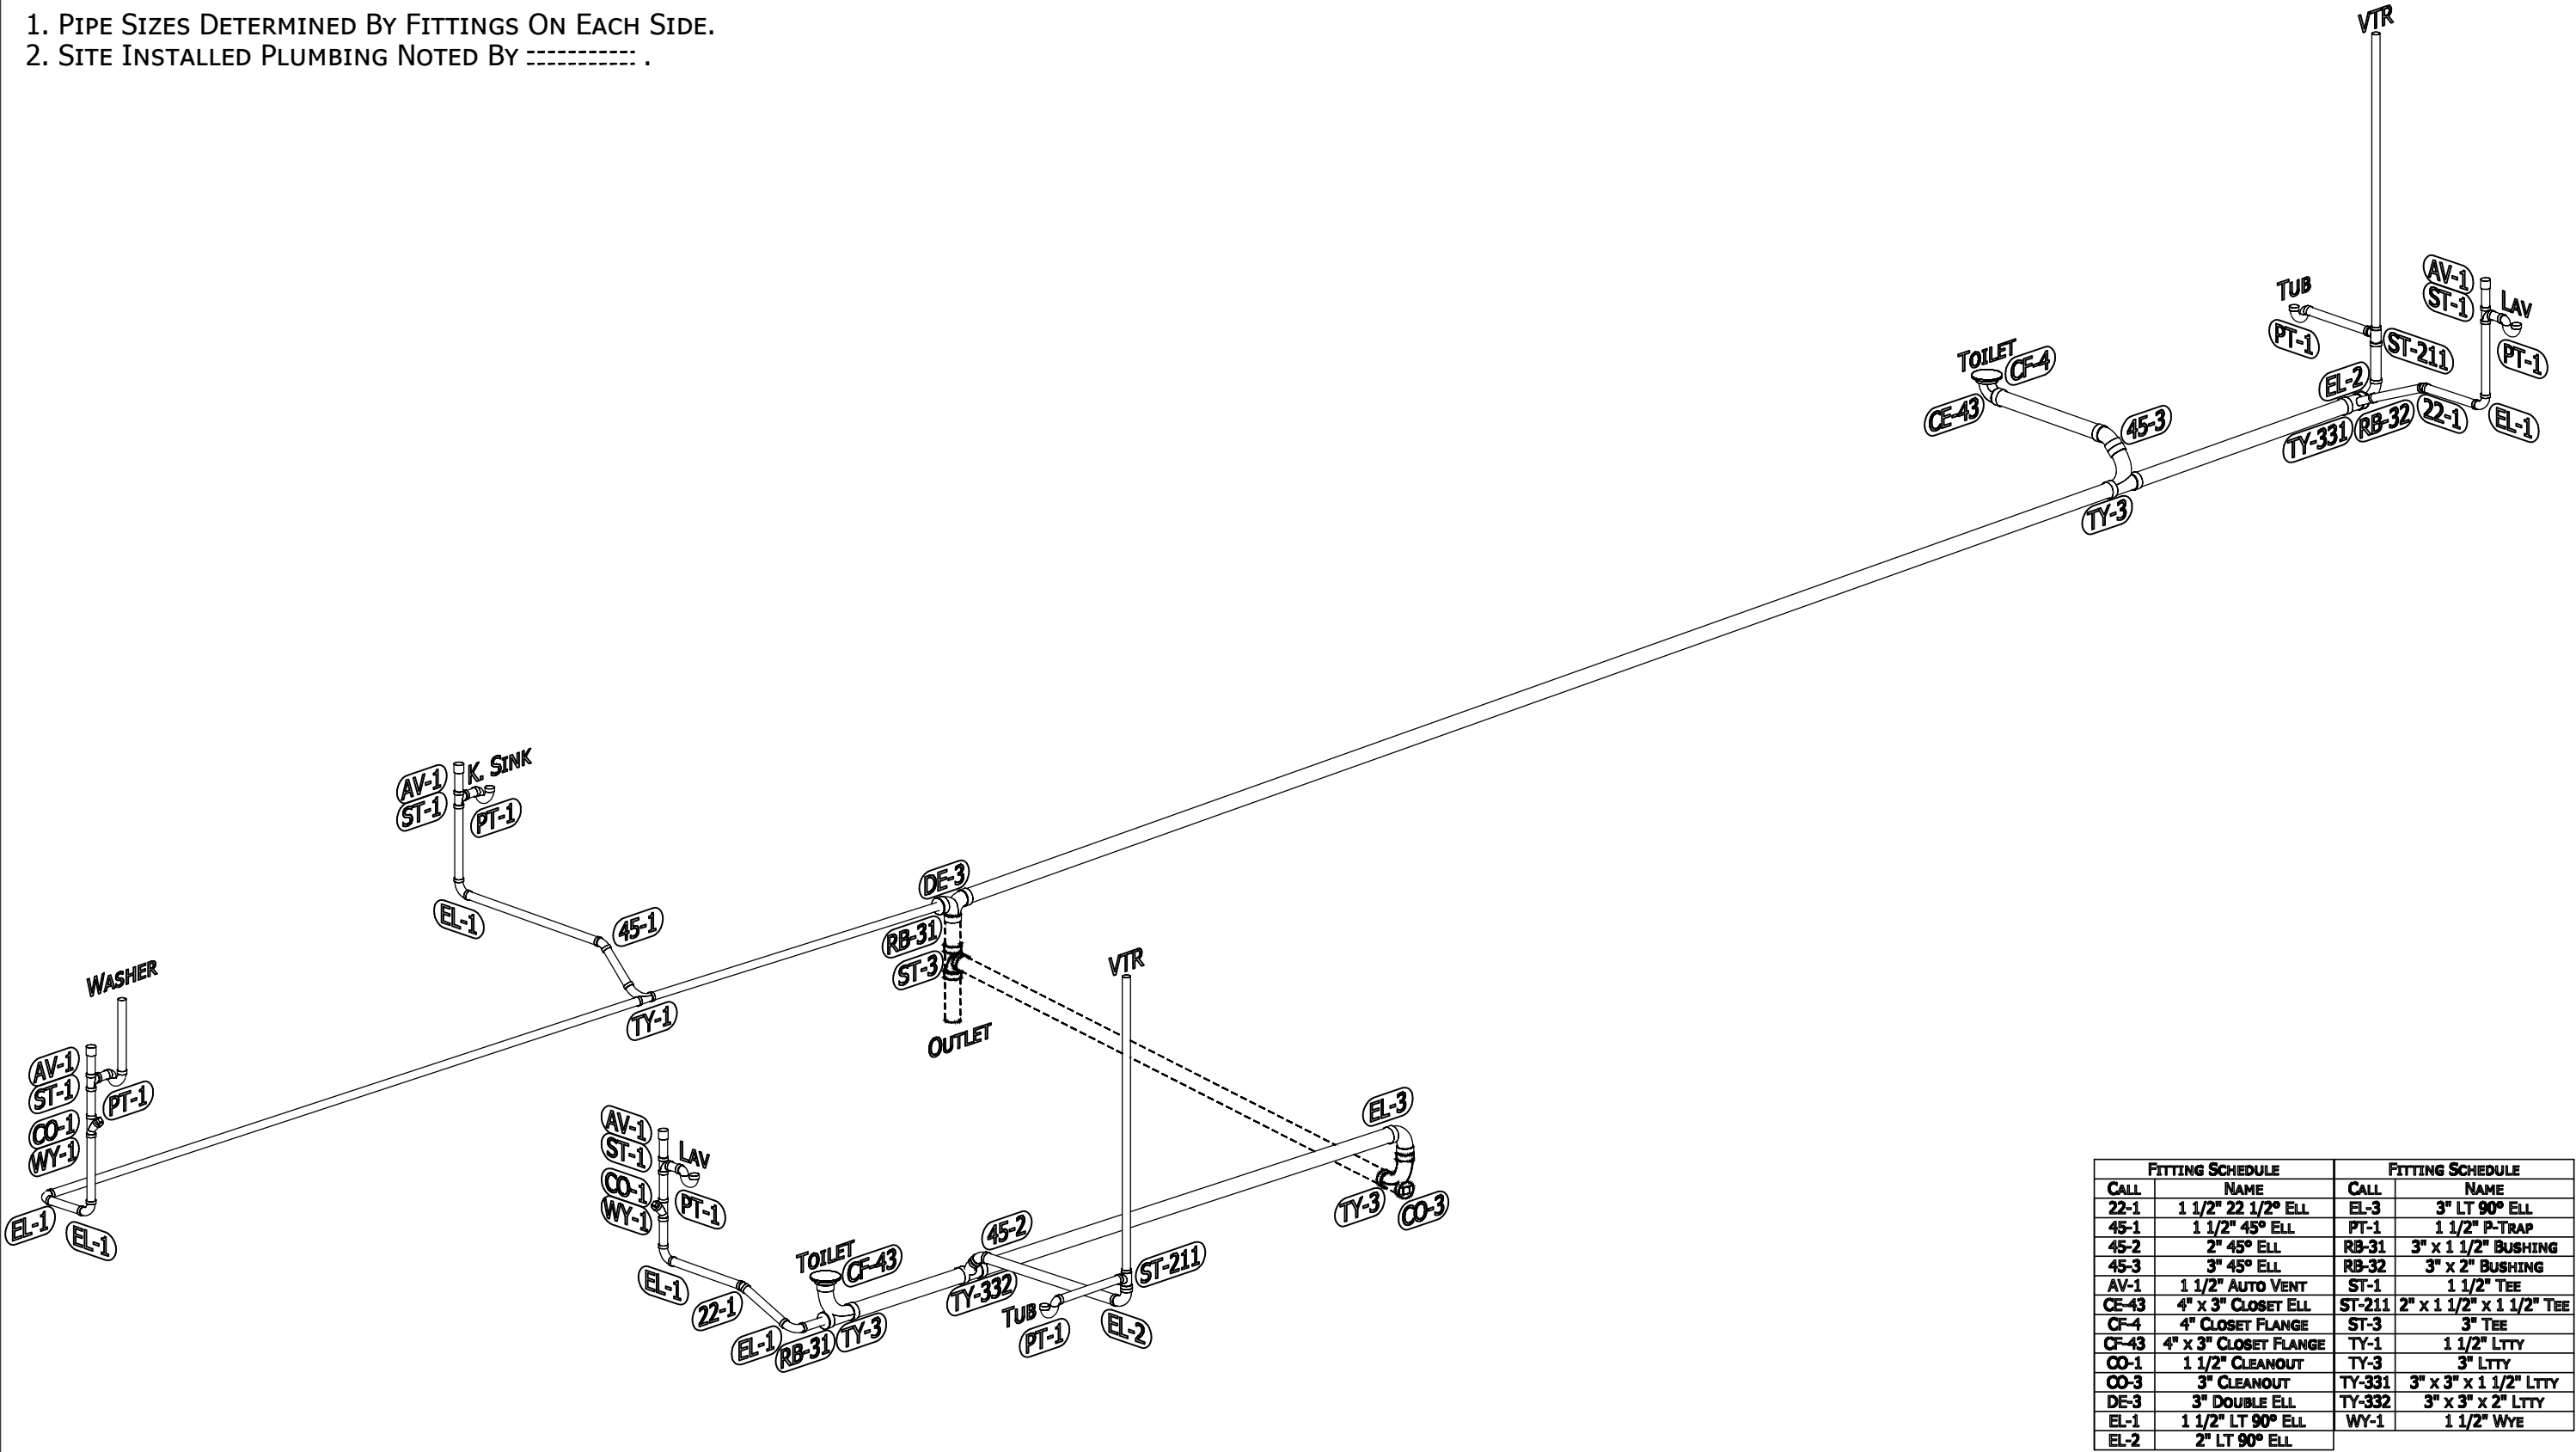

FITTING SCHEDULE		FITTING SCHEDULE	
CALL	NAME	CALL	NAME
22-1	1 1/2" 22 1/2° ELL	EL-3	3" LT 90° ELL
45-1	1 1/2" 45° ELL	PT-1	1 1/2" P-TRAP
45-2	2" 45° ELL	RB-31	3" x 1 1/2" BUSHING
45-3	3" 45° ELL	RB-32	3" x 2" BUSHING
AV-1	1 1/2" AUTO VENT	ST-1	1 1/2" TEE
CE-43	4" x 3" CLOSET ELL	ST-211	2" x 1 1/2" x 1 1/2" TEE
CF-4	4" CLOSET FLANGE	ST-3	3" TEE
CF-43	4" x 3" CLOSET FLANGE	TY-1	1 1/2" LT TY
CO-1	1 1/2" CLEANOUT	TY-3	3" LT TY
CO-3	3" CLEANOUT	TY-331	3" x 3" x 1 1/2" LT TY
DE-3	3" DOUBLE ELL	TY-332	3" x 3" x 2" LT TY
EL-1	1 1/2" LT 90° ELL	WY-1	1 1/2" WYE
EL-2	2" LT 90° ELL		

CHAMPION

HOME BUILDERS

755 W. BIG BEAVER ROAD, SUITE 1000 TROY, MI 48064
PHONE: 248-614-8200

PFS#23

Conforms to
HUD MHCSS
4/1/24

MODIFICATIONS

PROJECT:
112APB-2876H42180
76'-0" x 26'-8"
4BD 2BT

DRAWN BY: KG
DATE: 10-24-23
SCALE: 3/16" = 1'-0"

TITLE:
DRAIN LINE
PLAN



FILENAME: 112APB-2876H42180

SHEET:
D-101

PROPRIETARY AND CONFIDENTIAL
THESE DRAWINGS AND SPECIFICATIONS ARE ORIGINAL,
PROPRIETARY AND CONFIDENTIAL MATERIALS OF CHAMPION.
COPYRIGHT © 1976-2024 BY CHAMPION

NOTES:

- 1. PIPE SIZES DETERMINED BY FITTINGS ON EACH SIDE.
- 2. SITE INSTALLED PLUMBING NOTED BY ----- .

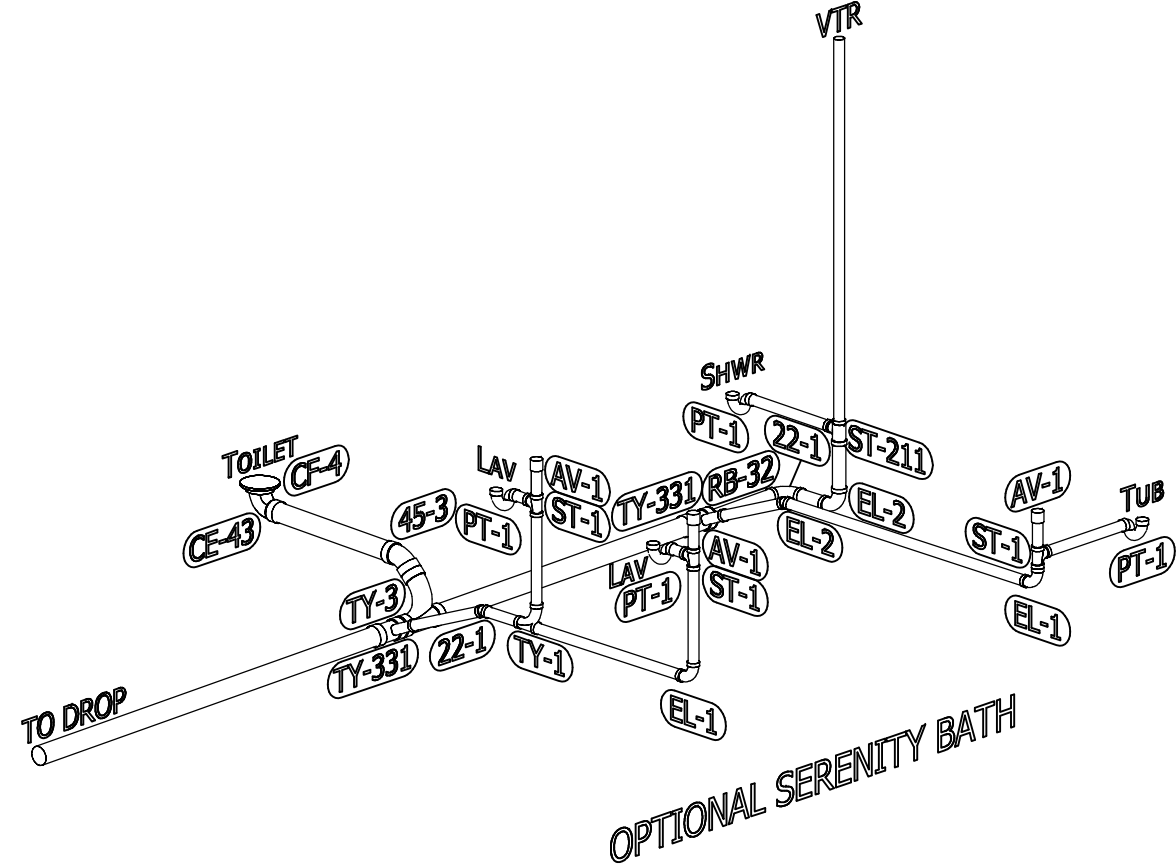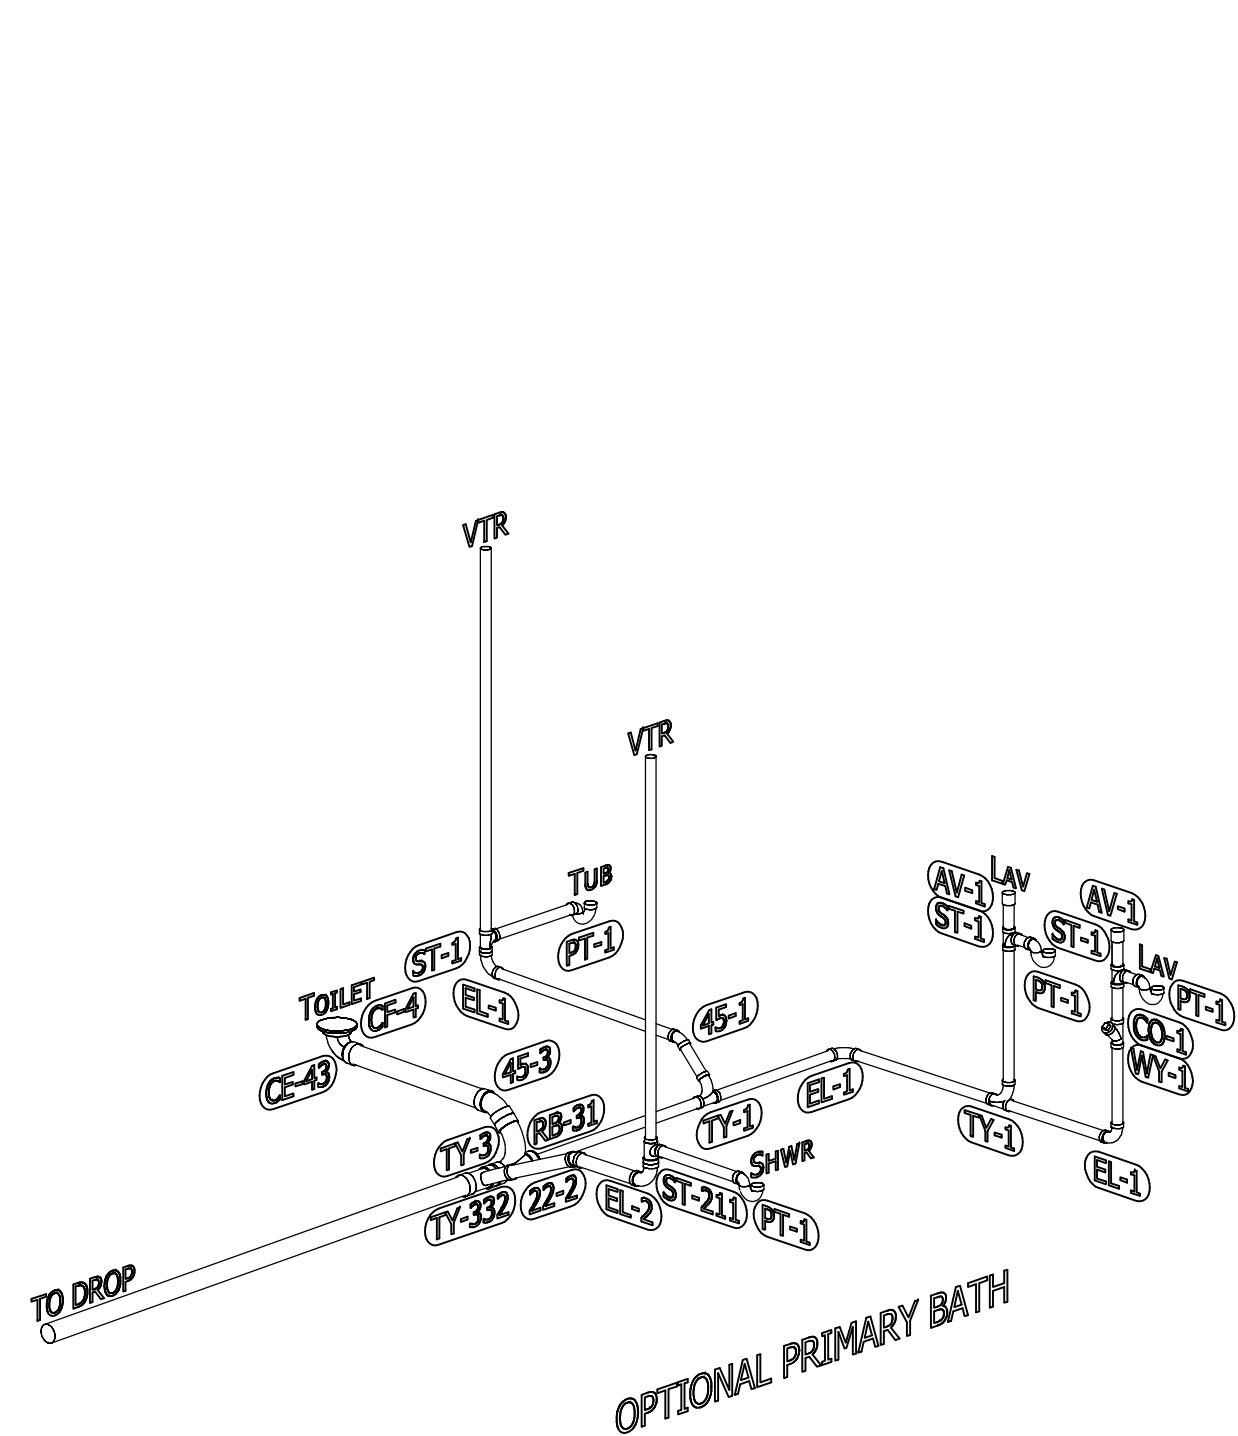

FITTING SCHEDULE		FITTING SCHEDULE	
CALL	NAME	CALL	NAME
22-1	1 1/2" 22 1/2° ELL	EL-3	3" LT 90° ELL
45-1	1 1/2" 45° ELL	PT-1	1 1/2" P-TRAP
45-2	2" 45° ELL	RB-31	3" x 1 1/2" BUSHING
45-3	3" 45° ELL	RB-32	3" x 2" BUSHING
AV-1	1 1/2" AUTO VENT	ST-1	1 1/2" TEE
CE-43	4" x 3" CLOSET ELL	ST-211	2" x 1 1/2" x 1 1/2" TEE
CF-4	4" CLOSET FLANGE	ST-3	3" TEE
CF-43	4" x 3" CLOSET FLANGE	TY-1	1 1/2" LT TY
CO-1	1 1/2" CLEANOUT	TY-3	3" LT TY
CO-3	3" CLEANOUT	TY-331	3" x 3" x 1 1/2" LT TY
DE-3	3" DOUBLE ELL	TY-332	3" x 3" x 2" LT TY
EL-1	1 1/2" LT 90° ELL	WY-1	1 1/2" WYE
EL-2	2" LT 90° ELL		

CHAMPION

HOME BUILDERS

755 W. BIG BEAVER ROAD, SUITE 1000 TROY, MI 48064
PHONE: 248-614-8200

PFS#23

Conforms to
HUD MHCSS
4/1/24

MODIFICATIONS

PROJECT:
112APB-2876H42180
76'-0" x 26'-8"
4BD 2BT

DRAWN BY: KG
DATE: 10-24-23
SCALE: 3/16" = 1'-0"

TITLE:
DRAIN LINE
PLAN
OPTIONS


FILENAME: 112APB-2876H42180

SHEET:
D-102

PROPRIETARY AND CONFIDENTIAL
THESE DRAWINGS AND SPECIFICATIONS ARE ORIGINAL,
PROPRIETARY AND CONFIDENTIAL MATERIALS OF CHAMPION.
COPYRIGHT © 1976-2024 BY CHAMPION

NOTES:

- 1. ALL PIPE SIZES 1/2" UNLESS OTHERWISE SPECIFIED
- 2. TOTAL BTU = 145,000(202,000 w/ OPTIONS)
- 3. COLUMN LENGTH = 20'-0"

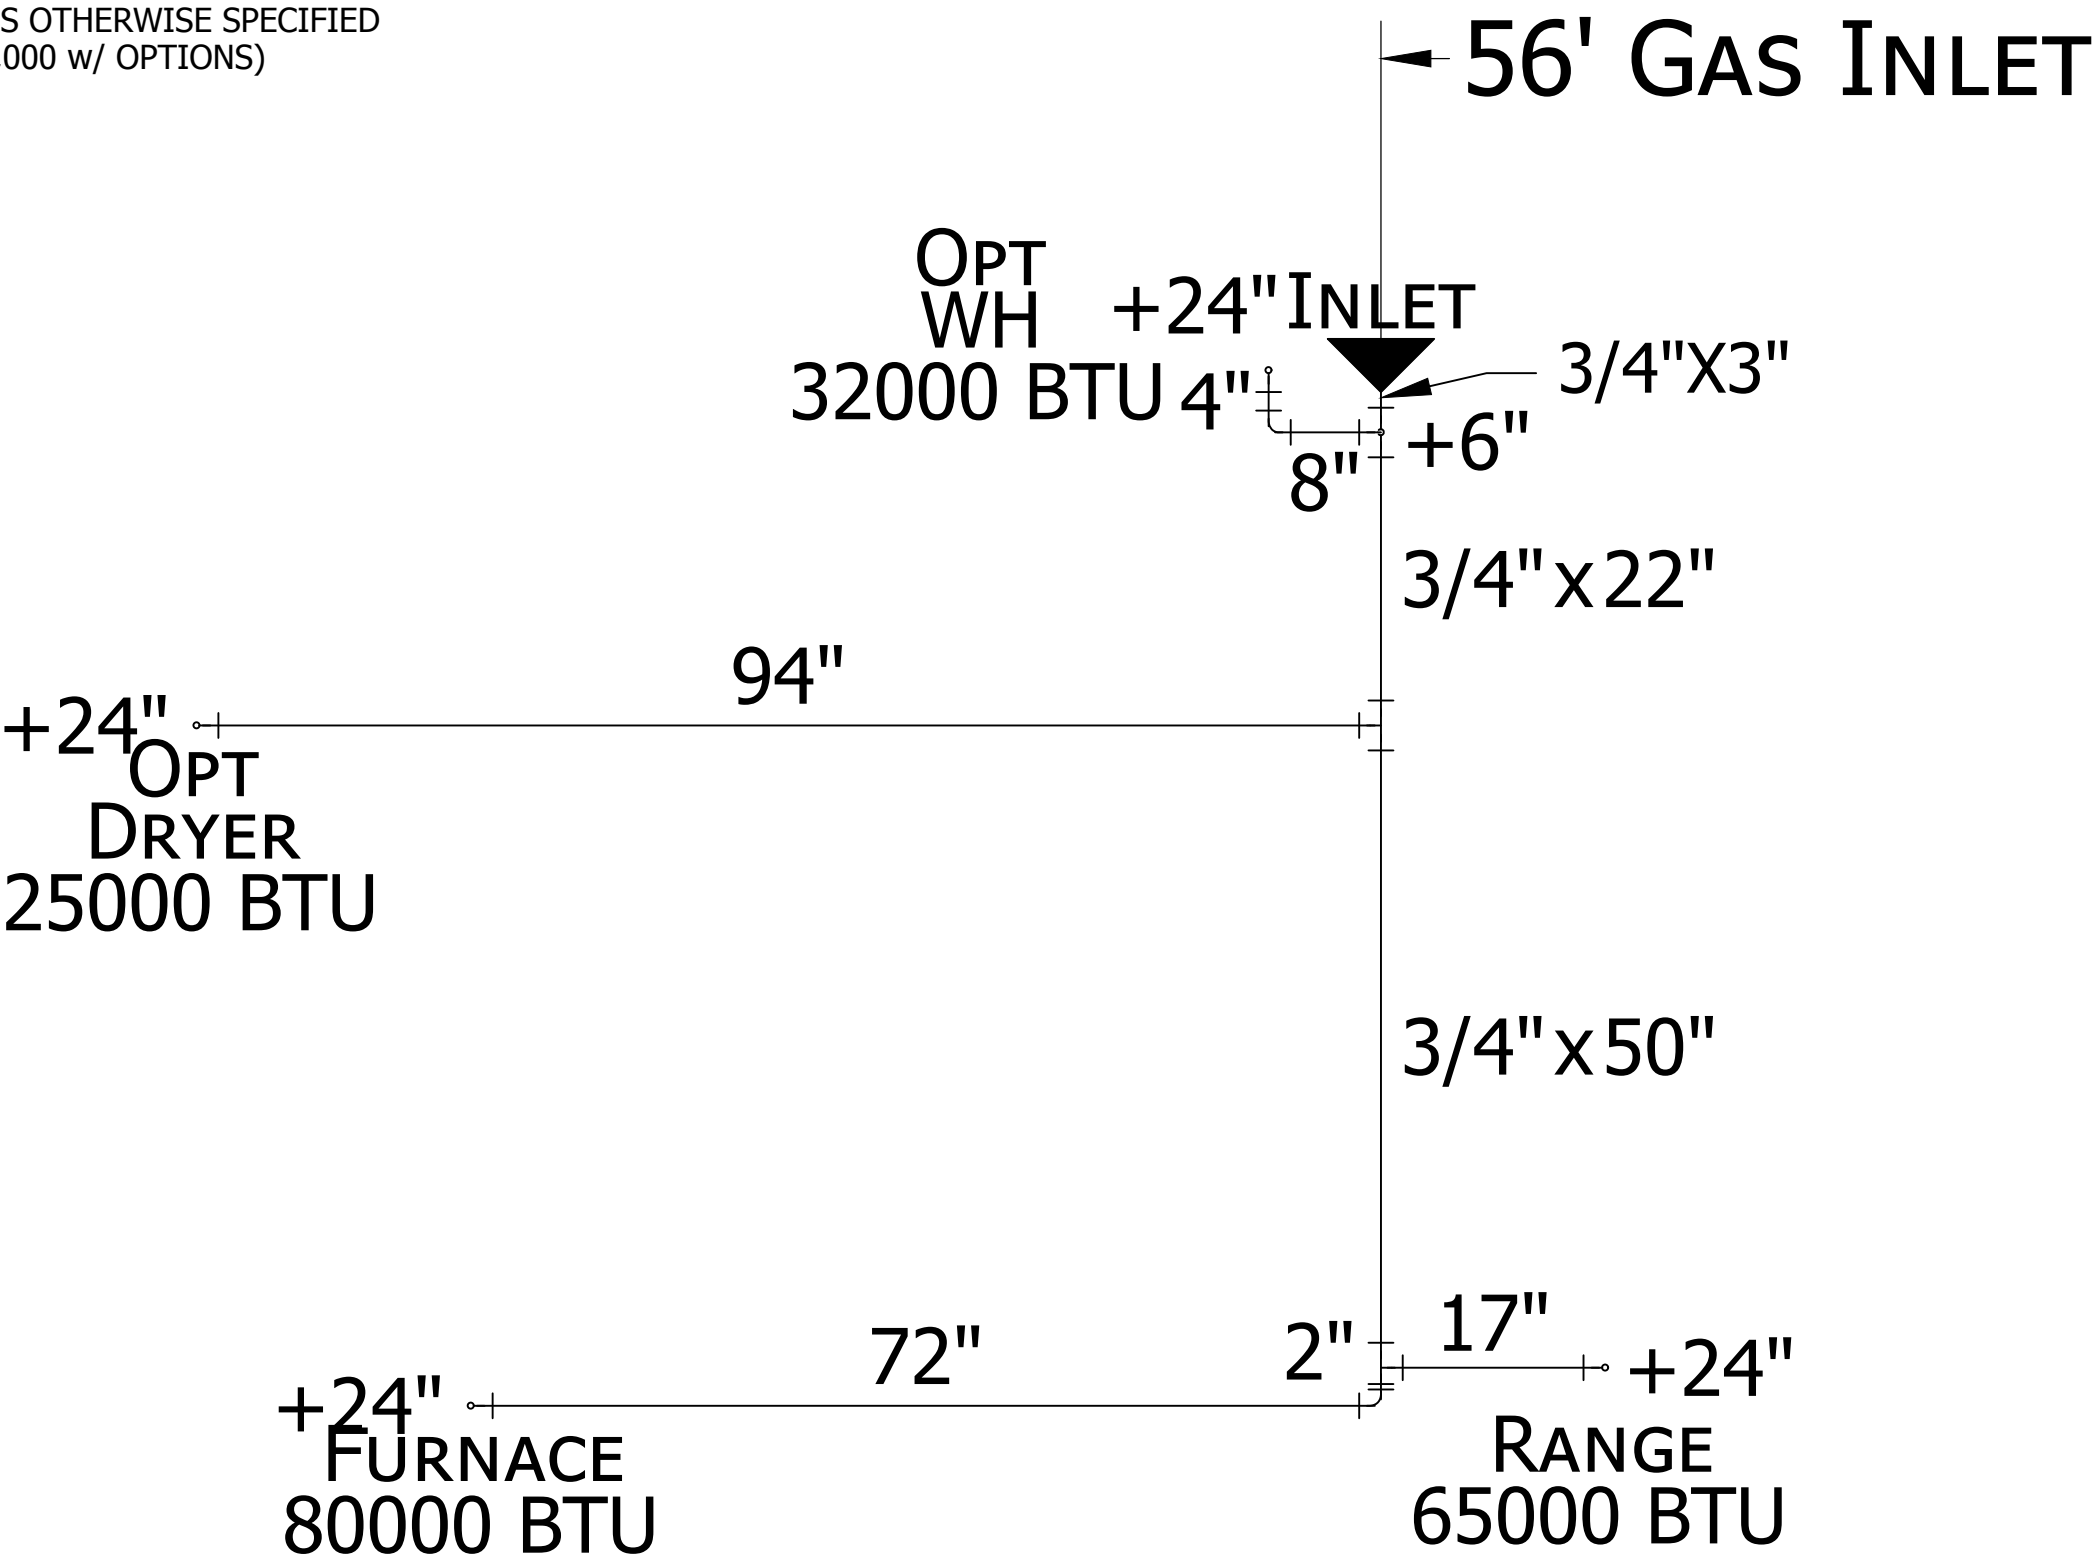

CHAMPION
HOME BUILDERS

755 W. BIG BEAVER ROAD, SUITE 1000 TROY, MI 48064
PHONE: 248-614-8200



MODIFICATIONS

PROJECT:
112APB-2876H42180
76'-0" x 26'-8"
4BD 2BT

DRAWN BY: KG
DATE: 10-24-23
SCALE: 3/16" = 1'-0"

TITLE:
GAS LINE
PLAN


FILENAME: 112APB-2876H42180

SHEET:
G-101

PROPRIETARY AND CONFIDENTIAL
THESE DRAWINGS AND SPECIFICATIONS ARE ORIGINAL,
PROPRIETARY AND CONFIDENTIAL MATERIALS OF CHAMPION.
COPYRIGHT © 1976-2024 BY CHAMPION

NOTES:

- 1. ALL PIPE SIZES 1/2" UNLESS OTHERWISE SPECIFIED
- 2. TOTAL BTU = 110,000(167,000 w/OPTIONS)
- 3. COLUMN LENGTH = 20'-0"

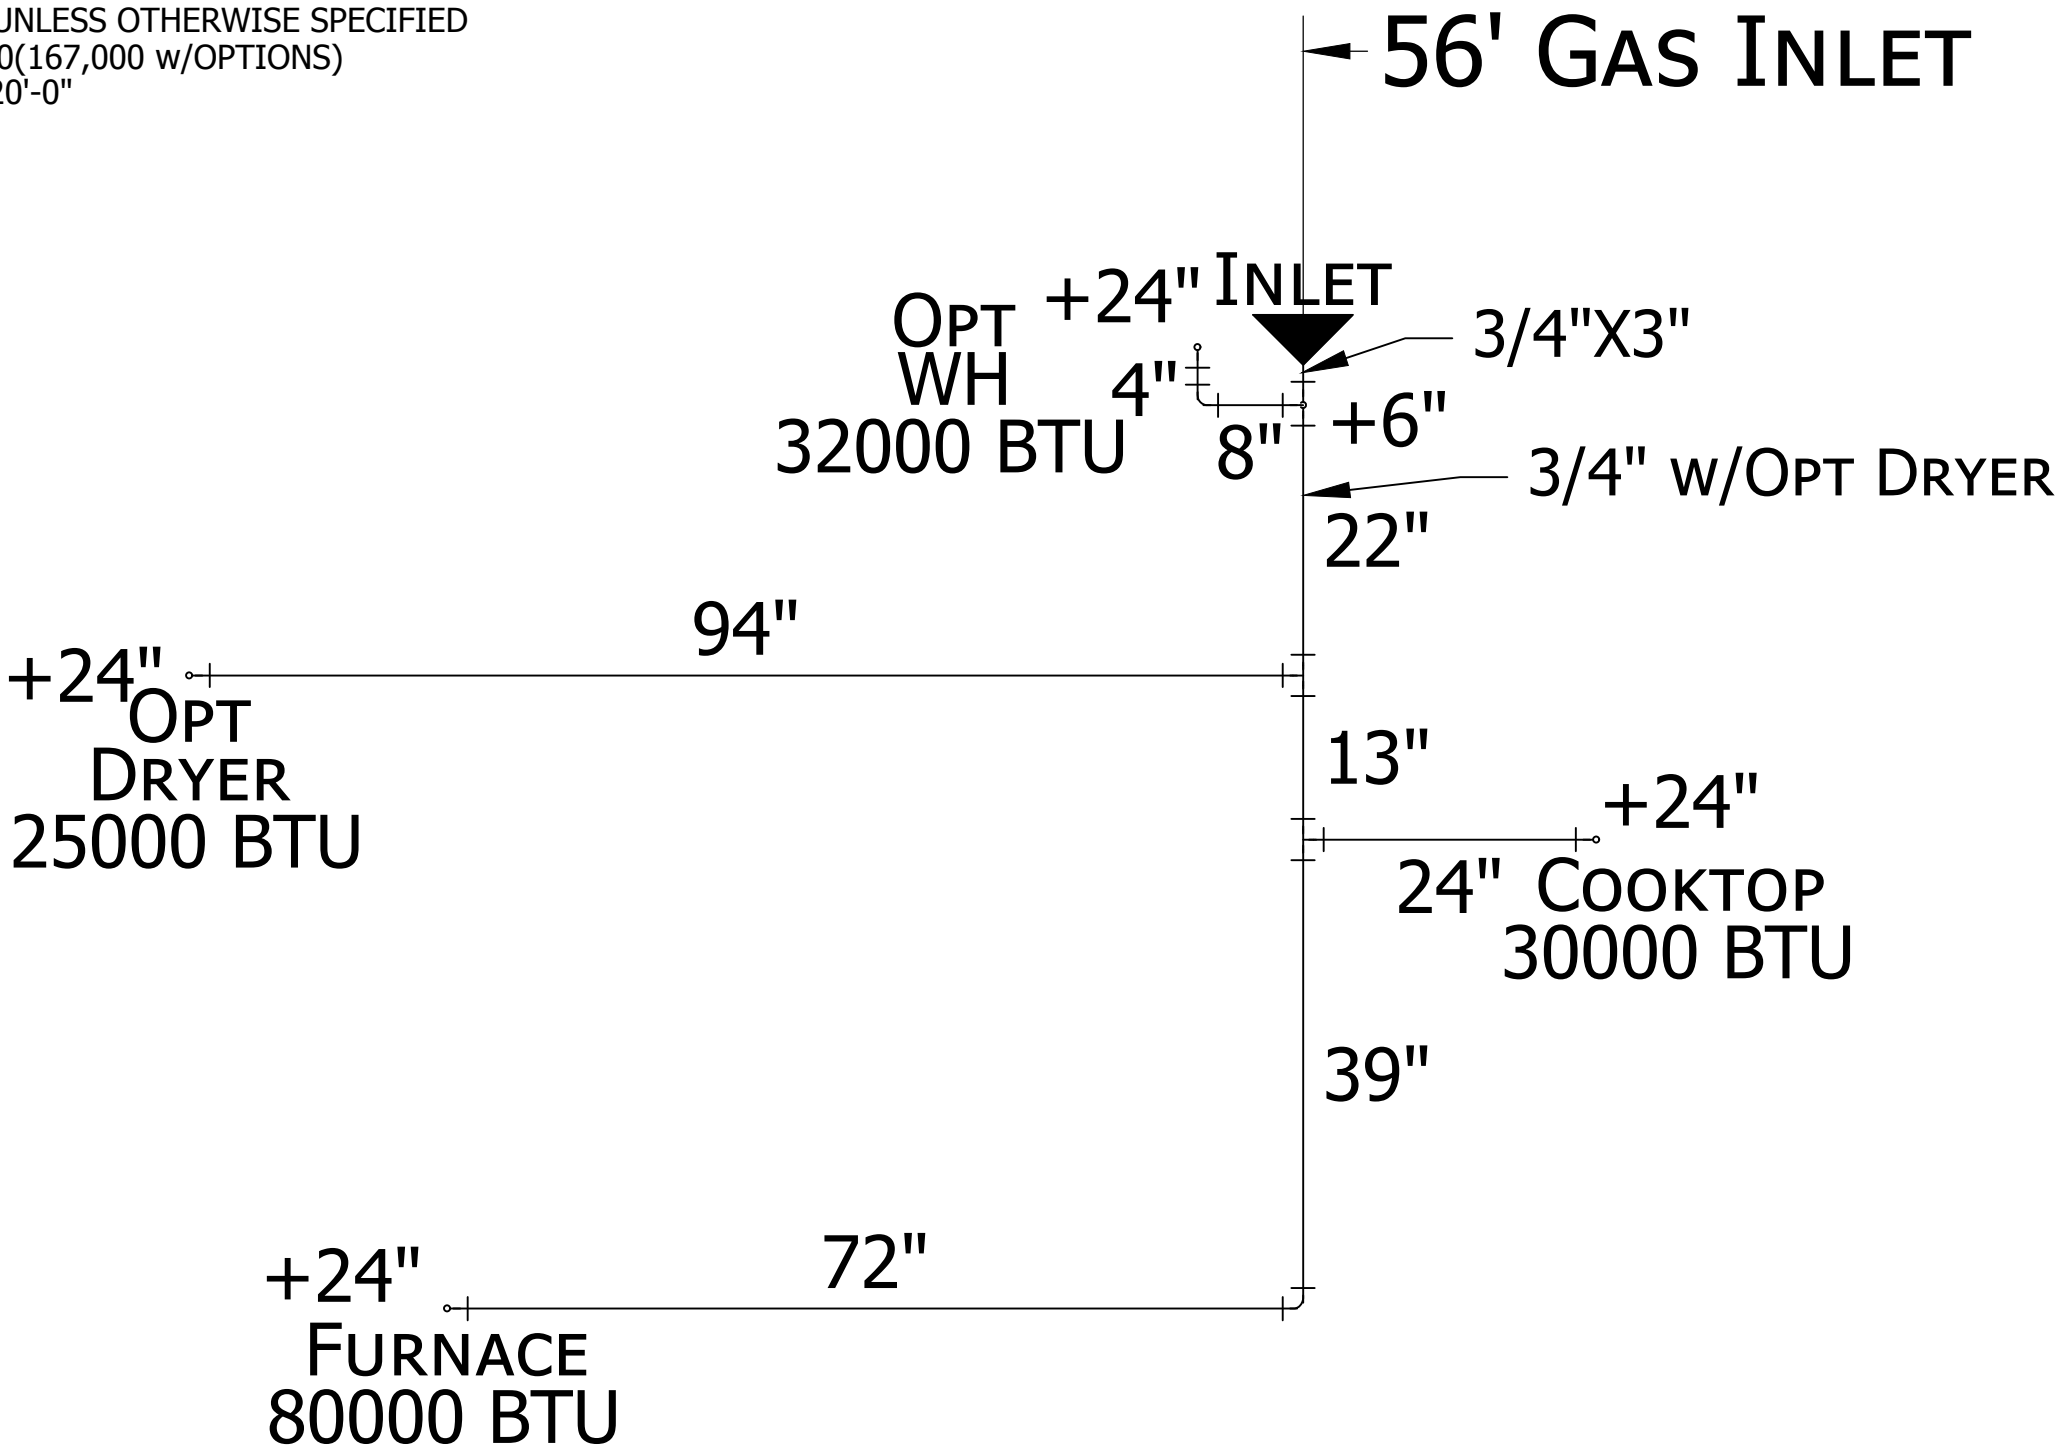

OPTIONAL ULTIMATE KITCHEN 2